

1 2 x Kozijn: stijl

S235, koker 40x40x2 · L = 2395 · zagen 90°/45° · 5,53 kg/st


Waar het stuk zit

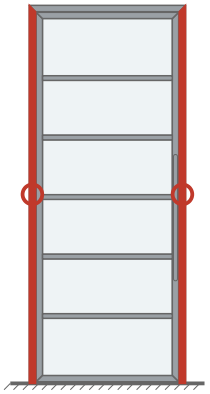

Aanzicht (1:20)

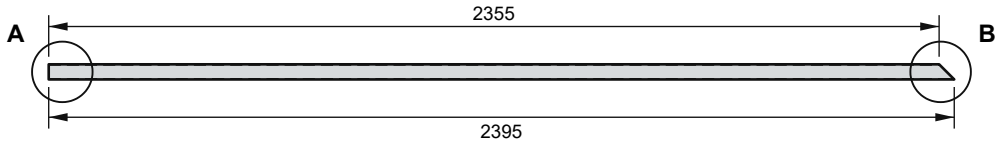


Detail A (1:1): linker uiteinde

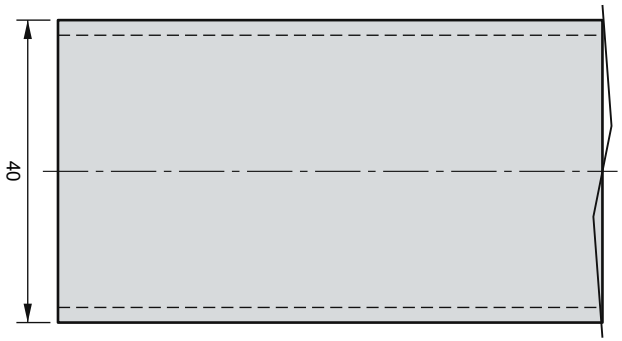


Recht afzagen (90°)

Detail B (1:1): rechter uiteinde

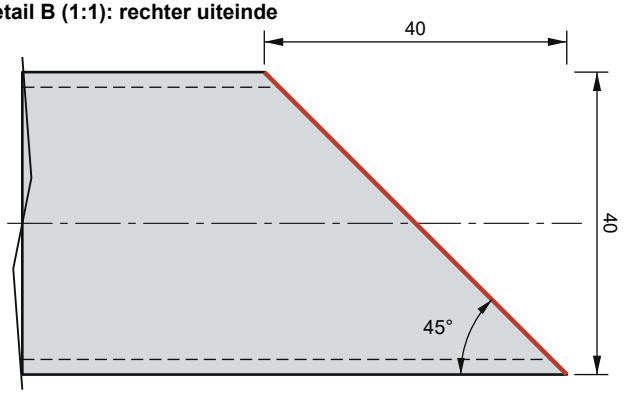

Verstek 45°: lange kant is 40 langer dan de korte

Doorsnede van het profiel

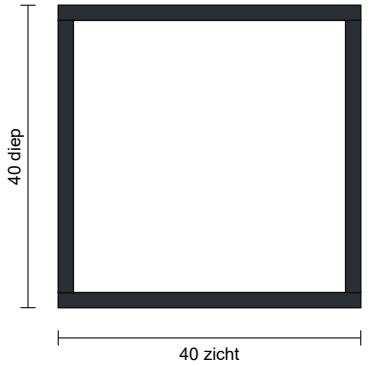

koker 40x40x2

1:1 · 40 x 40 · wand 2

Bewerking en verbindingen

Bewerking: recht · verstek 45°


V1: 2 x verstek 45° met pos 2 (Kozijn: bovenregel)

Titel: **Pos 1: Kozijn: stijl**			
Deur: Ladder · opening 1000 x 2400		Tekeningnummer: **TD-14-01**	
Maten en toleranties: mm · ISO 2768-m · eerste hoek	Opgesteld: Ian · laswerken	Uitgifte: 2026-11-10	Blad: 1 / 15


2 1 x Kozijn: bovenregel

S235, koker 40x40x2 · L = 990 · zagen 45°/45° · 2,29 kg/st


Aanzicht (1:10)

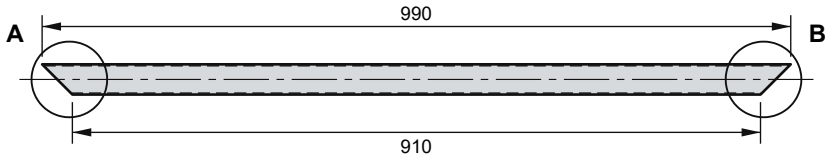

Waar het stuk zit

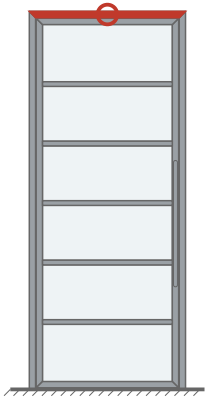


Detail A (1:1): linker uiteinde

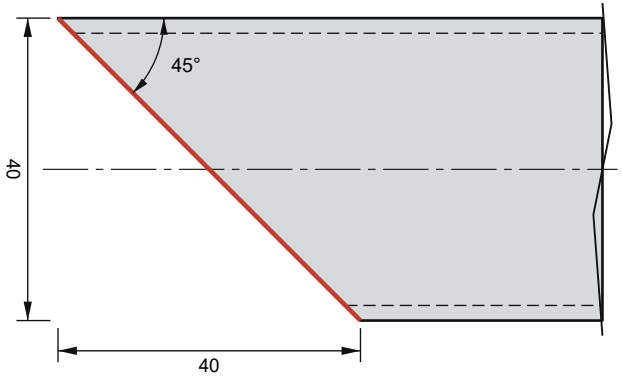


Verstek 45°: lange kant is 40 langer dan de korte

Detail B (1:1): rechter uiteinde

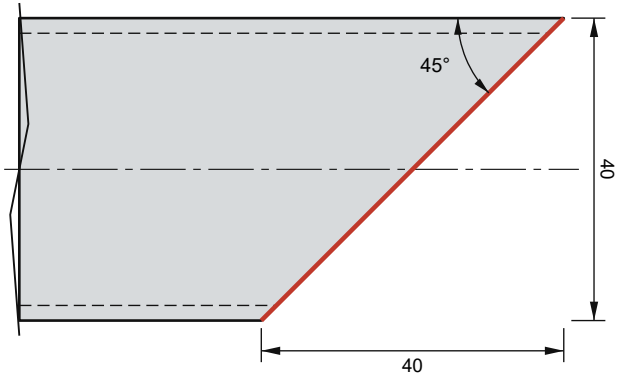

Verstek 45°: lange kant is 40 langer dan de korte

Doorsnede van het profiel

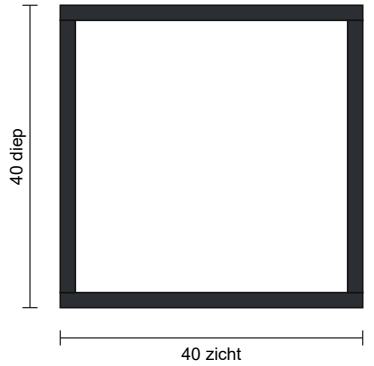

koker 40x40x2

1:1 · 40 x 40 · wand 2

Bewerking en verbindingen

Bewerking: verstek 45° · verstek 45°


V1: 2 x verstek 45° met pos 1 (Kozijn: stijl)

Titel: **Pos 2: Kozijn: bovenregel**			
Deur: Ladder · opening 1000 x 2400		Tekeningnummer: **TD-14-02**	
Maten en toleranties: mm · ISO 2768-m · eerste hoek	Opgesteld: lan · laswerken	Uitgifte: 2026-11-10	Blad: 2 / 15


3 2 x Kader: staander

S235, koker 40x40x2 · L = 2341 · zagen 45°/45° · 5,41 kg/st


Aanzicht (1:20)

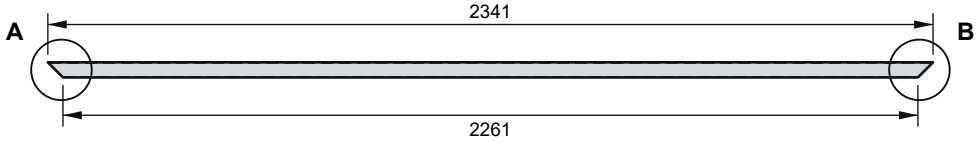

Waar het stuk zit

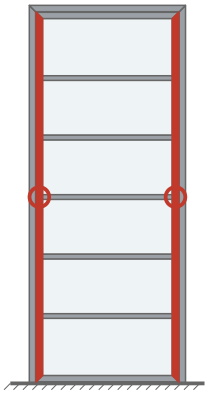


Detail A (1:1): linker uiteinde

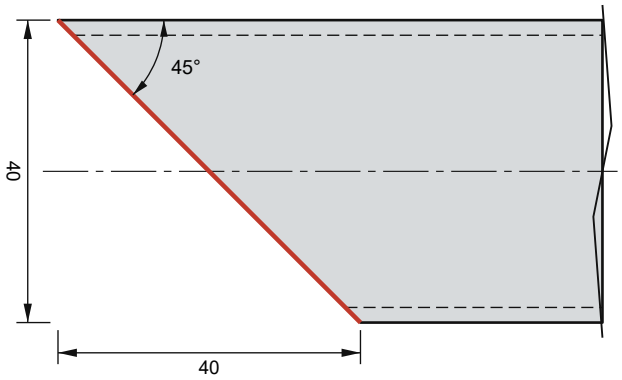


Verstek 45°: lange kant is 40 langer dan de korte

Detail B (1:1): rechter uiteinde

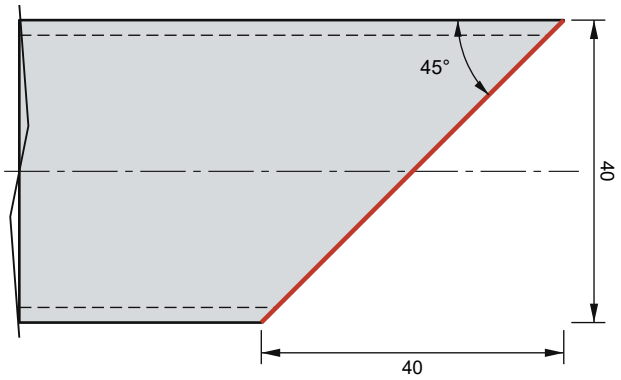

Verstek 45°: lange kant is 40 langer dan de korte

Doorsnede van het profiel

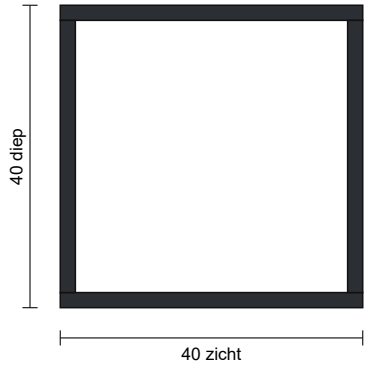

koker 40x40x2

1:1 · 40 x 40 · wand 2

Bewerking en verbindingen


Bewerking: verstek 45° · verstek 45°
V2: 4 x verstek 45° met pos 4 (Kader: regel)
T1: 10 x t-verbinding (stomp) met pos 5 (Roede horizontaal: kern)

Titel: **Pos 3: Kader: staander**			
Deur: Ladder · opening 1000 x 2400		Tekeningnummer: **TD-14-03**	
Maten en toleranties: mm · ISO 2768-m · eerste hoek	Opgesteld: Ian · laswerken	Uitgifte: 2026-11-10	Blad: 3 / 15


4 2 x Kader: regel

S235, koker 40x40x2 · L = 902 · zagen 45°/45° · 2,08 kg/st


Waar het stuk zit

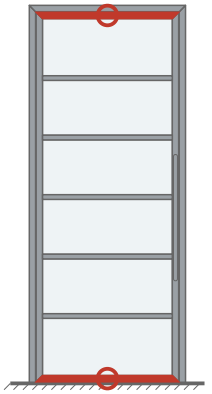

Aanzicht (1:10)

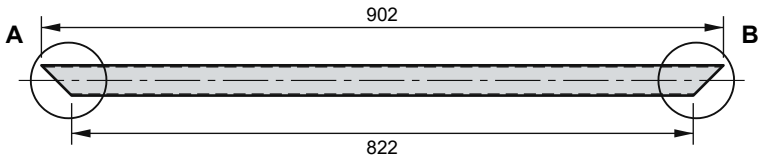


Detail A (1:1): linker uiteinde

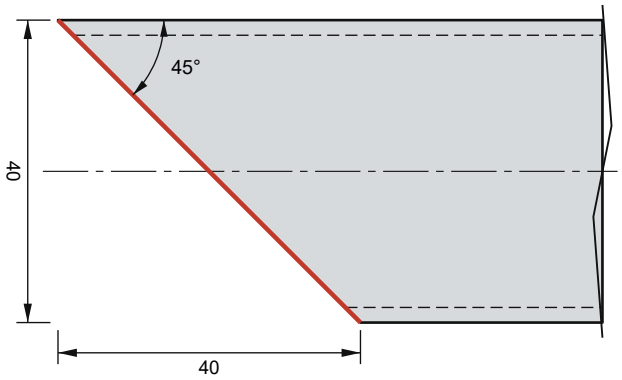


Verstek 45°: lange kant is 40 langer dan de korte

Detail B (1:1): rechter uiteinde

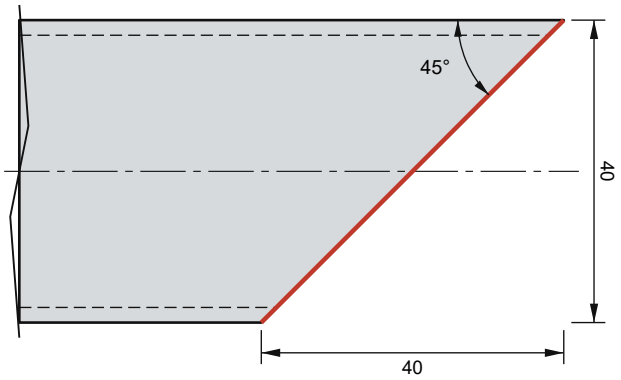

Verstek 45°: lange kant is 40 langer dan de korte

Doorsnede van het profiel

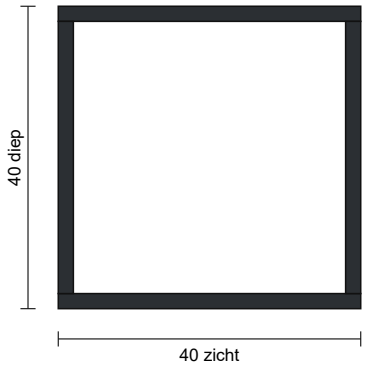

koker 40x40x2

1:1 · 40 x 40 · wand 2

Bewerking en verbindingen

Bewerking: verstek 45° · verstek 45°

V2: 4 x verstek 45° met pos 3 (Kader: staander)


Titel: **Pos 4: Kader: regel**			
Deur: Ladder · opening 1000 x 2400		Tekeningnummer: **TD-14-04**	
Maten en toleranties: mm · ISO 2768-m · eerste hoek	Opgesteld: Ian · laswerken	Uitgifte: 2026-11-10	Blad: 4 / 15

5 x Roede horizontaal: kern


5

S235, platstaal 20x10 · L = 822 · zagen 90°/90° · 1,29 kg/st


Aanzicht (1:5)

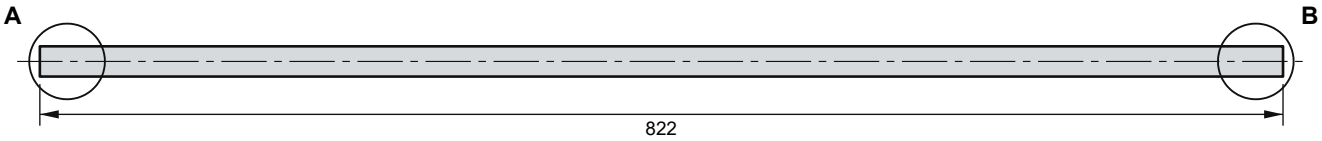

Waar het stuk zit

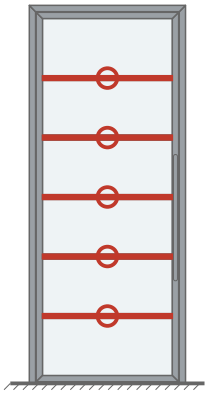


Detail A (2:1): linker uiteinde

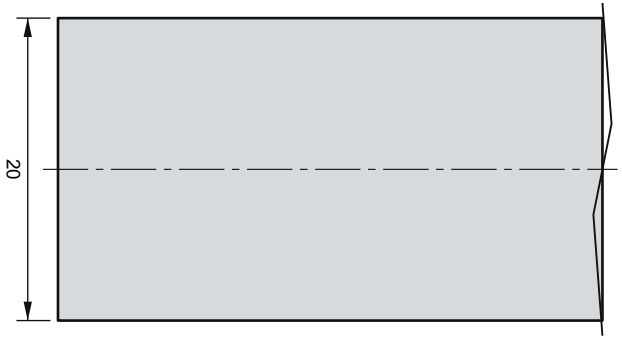


Recht afzagen (90°)

Detail B (2:1): rechter uiteinde

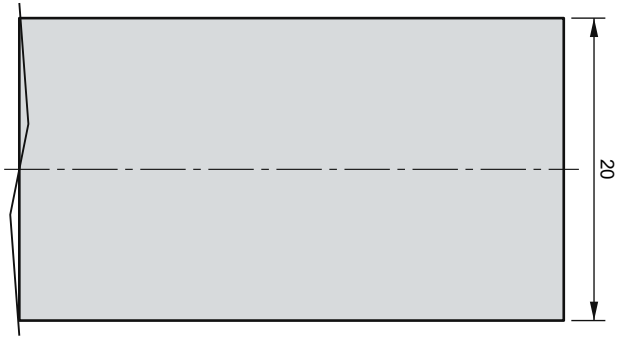

Recht afzagen (90°)

Doorsnede van het profiel

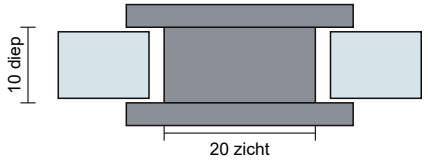

platstaal 20x10

1:1 · 20 x 10

Bewerking en verbindingen

Bewerking: recht · recht; M4 om de 250 aan de achterkant


T1: 10 x t-verbinding (stomp) met pos 3 (Kader: staander)

Titel: **Pos 5: Roede horizontaal: kern**			
Deur: Ladder · opening 1000 x 2400		Tekeningnummer: **TD-14-05**	
Maten en toleranties: mm · ISO 2768-m · eerste hoek	Opgesteld: Ian · laswerken	Uitgifte: 2026-11-10	Blad: 5 / 15


6 10 x Roede horizontaal: lat voor en achter

S235, platstaal 30x3 · L = 822 · zagen 90°/90° · 0,58 kg/st


Waar het stuk zit

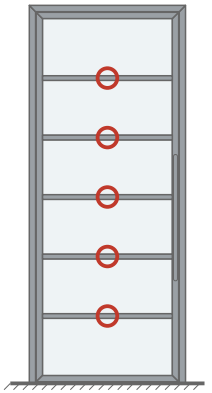

Aanzicht (1:5)

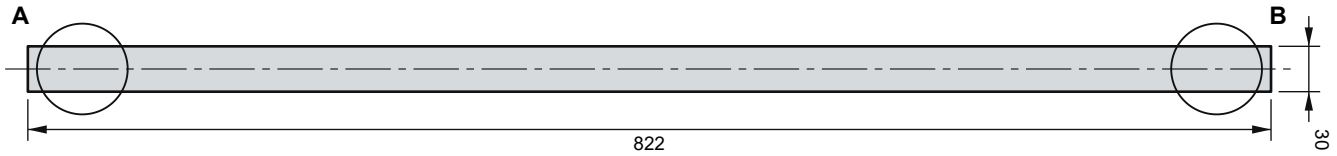


Detail A (1:1): linker uiteinde

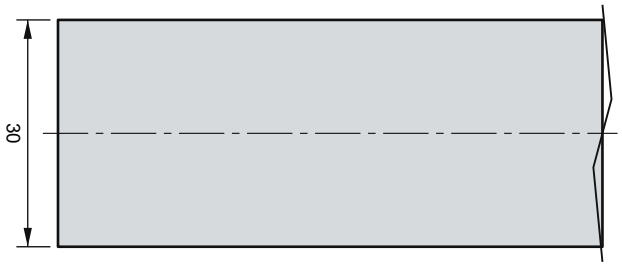


Recht afzagen (90°)

Detail B (1:1): rechter uiteinde

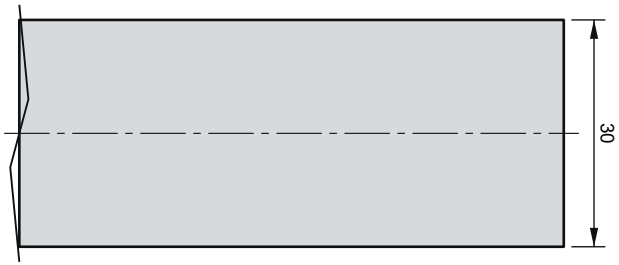

Recht afzagen (90°)

Doorsnede (arcering = materiaal)

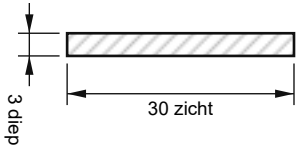

platstaal 30x3 (1:1)

boven = de kant met de greep

Bewerking en verbindingen

Bewerking: recht · recht; voor gelast, achter geschroefd

Hechten om de 150 en lassen (voor) of M4 verzonken om de 250 (achter): zie de werkwijze

Titel: **Pos 6: Roede horizontaal: lat voor en achter**			
Deur: Ladder · opening 1000 x 2400		Tekeningnummer: **TD-14-06**	
Maten en toleranties: mm · ISO 2768-m · eerste hoek	Opgesteld: Ian · laswerken	Uitgifte: 2026-11-10	Blad: 6 / 15


7 4 x Glaslat

S235, platstaal 15x4 · L = 822 · 0,39 kg/st


Aanzicht (1:5)



Waar het stuk zit

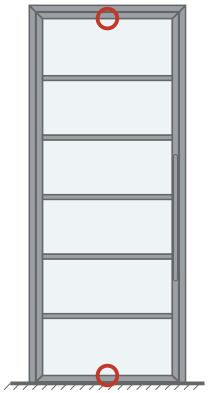


Detail A (2:1): linker uiteinde

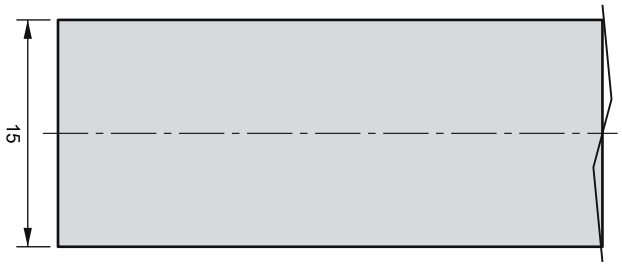

Recht afzagen (90°)

Detail B (2:1): rechter uiteinde

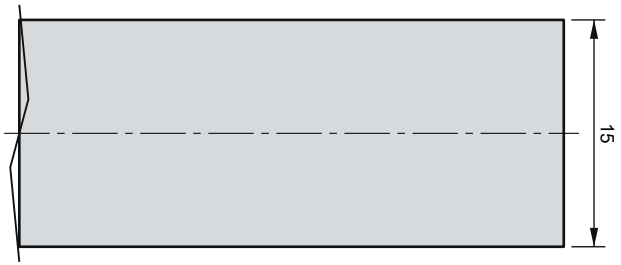

Recht afzagen (90°)

Doorsnede van het profiel



platstaal 15x4

3:1 · 15 x 4

Bewerking en verbindingen

Bewerking: recht; voor gelast, achter geschroefd (M4 verzonken om de 250)
Hechten om de 150 en lassen (voor) of M4 verzonken om de 250 (achter): zie de werkwijze

Titel: **Pos 7: Glaslat**			
Deur: Ladder · opening 1000 x 2400		Tekeningnummer: **TD-14-07**	
Maten en toleranties: mm · ISO 2768-m · eerste hoek	Opgesteld: Ian · laswerken	Uitgifte: 2026-11-10	Blad: 7 / 15


8 x Glaslat

S235, platstaal 15x4 · L = 362 · 0,17 kg/st


Aanzicht (1:5)



Waar het stuk zit

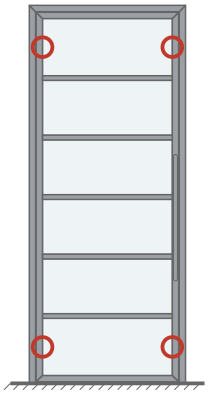


Detail A (2:1): linker uiteinde

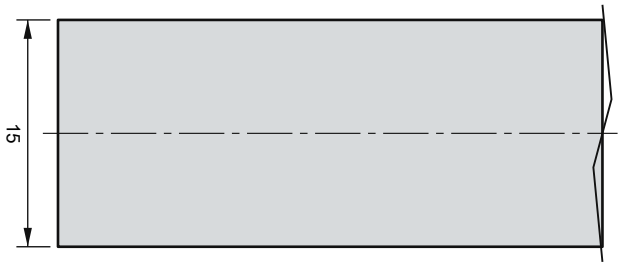

Recht afzagen (90°)

Detail B (2:1): rechter uiteinde

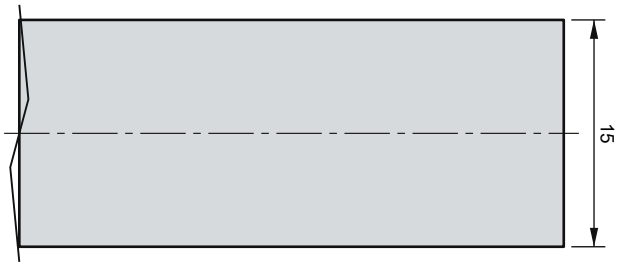

Recht afzagen (90°)

Doorsnede van het profiel



platstaal 15x4

3:1 · 15 x 4

Bewerking en verbindingen


Bewerking: recht; voor gelast, achter geschroefd (M4 verzonken om de 250)
Hechten om de 150 en lassen (voor) of M4 verzonken om de 250 (achter): zie de werkwijze

Titel: **Pos 8: Glaslat**			
Deur: Ladder · opening 1000 x 2400		Tekeningnummer: **TD-14-08**	
Maten en toleranties: mm · ISO 2768-m · eerste hoek	Opgesteld: Ian · laswerken	Uitgifte: 2026-11-10	Blad: 8 / 15


9 16 x Glaslat

S235, platstaal 15x4 · L = 347 · 0,16 kg/st


Aanzicht (1:2)

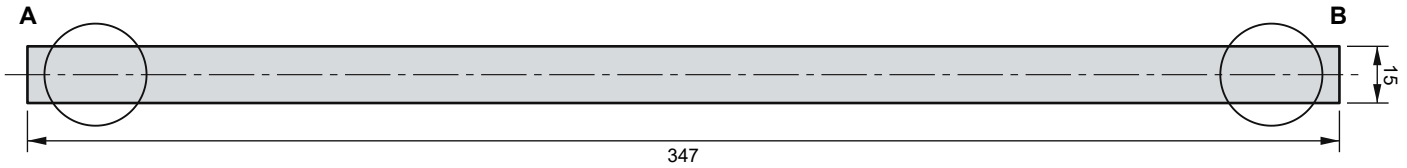

Waar het stuk zit

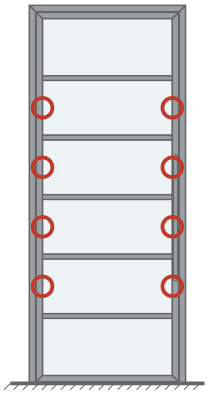


Detail A (2:1): linker uiteinde

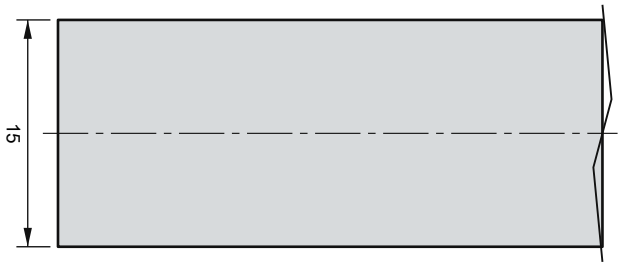

Recht afzagen (90°)

Detail B (2:1): rechter uiteinde

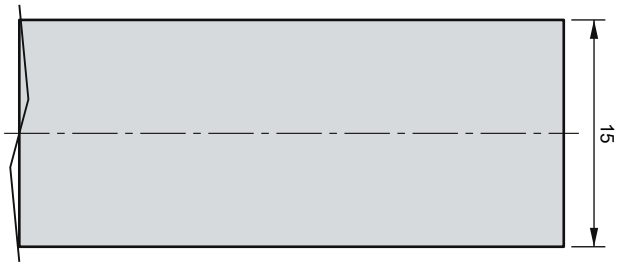

Recht afzagen (90°)

Doorsnede van het profiel



platstaal 15x4

3:1 · 15 x 4

Bewerking en verbindingen

Bewerking: recht; voor gelast, achter geschroefd (M4 verzonken om de 250)


Hechten om de 150 en lassen (voor) of M4 verzonken om de 250 (achter): zie de werkwijze

Titel: **Pos 9: Glaslat**			
Deur: Ladder · opening 1000 x 2400		Tekeningnummer: **TD-14-09**	
Maten en toleranties: mm · ISO 2768-m · eerste hoek	Opgesteld: Ian · laswerken	Uitgifte: 2026-11-10	Blad: 9 / 15


10 2 x Greep (voor en achter)

S235, rond Ø25 · L = 800 · 3,08 kg/st


Waar het stuk zit

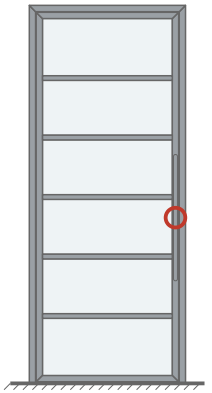

Aanzicht (1:5)

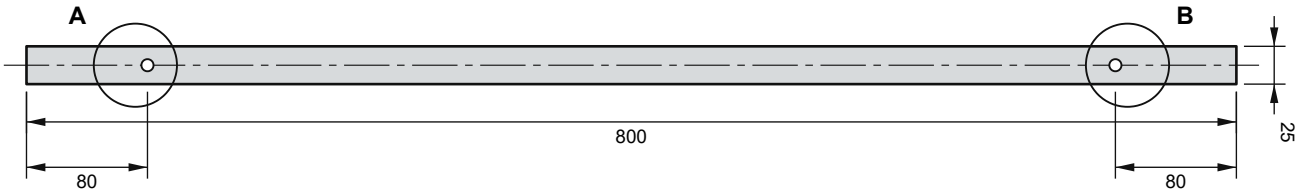


Detail A (1:2): linker uiteinde

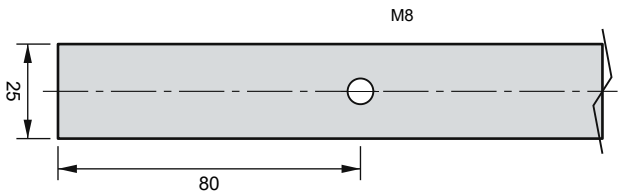


Recht afzagen (90°)

Detail B (1:2): rechter uiteinde

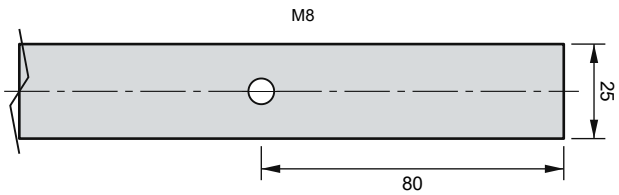

Recht afzagen (90°)

Doorsnede (arcering = materiaal)

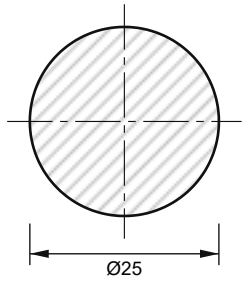

rond Ø25 (1:1)

Bewerking en verbindingen


Bewerking: uiteinden rond slijpen; 2 x M8 op 80 van de uiteinden

Titel: **Pos 10: Greep (voor en achter)**			
Deur: Ladder · opening 1000 x 2400		Tekeningnummer: **TD-14-10**	
Maten en toleranties: mm · ISO 2768-m · eerste hoek	Opgesteld: Ian · laswerken	Uitgifte: 2026-11-10	Blad: 10 / 15


11 1 x Taatsplaat onder

S235, plaat 8 mm · 36 x 220 · 0,5 kg/st

Aanzicht (1:2)

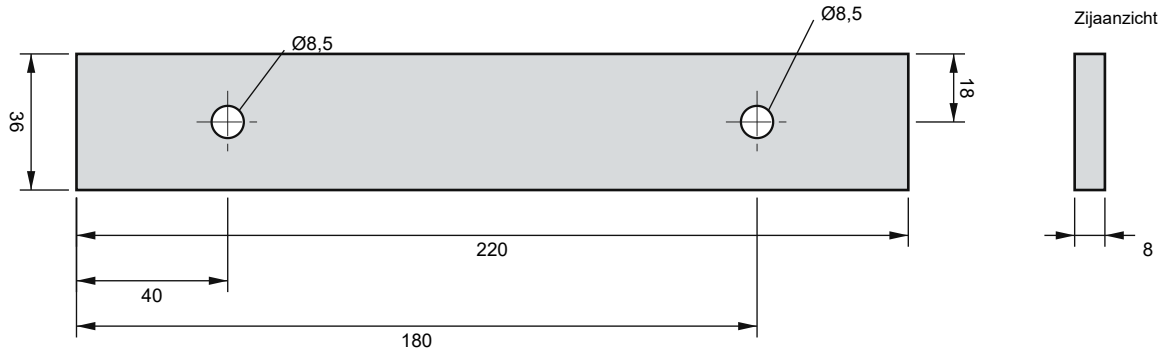

Waar het stuk zit

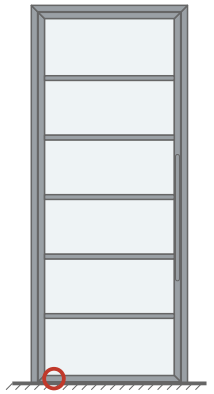

Plaat

S235, plaat 8 mm

36 x 220 x 8 mm

Lasersnijden op de DXF; braam eraf

Bewerking en verbindingen


Bewerking: 2 x Ø8,5 voor het scharnier; in de onderregel gelast

Titel: **Pos 11: Taatsplaat onder**			
Deur: Ladder · opening 1000 x 2400		Tekeningnummer: **TD-14-11**	
Maten en toleranties: mm · ISO 2768-m · eerste hoek	Opgesteld: Ian · laswerken	Uitgifte: 2026-11-10	Blad: 11 / 15

12 1 x Taatsplaat boven

S235, plaat 8 mm · 36 x 140 · 0,32 kg/st

Aanzicht (1:1)

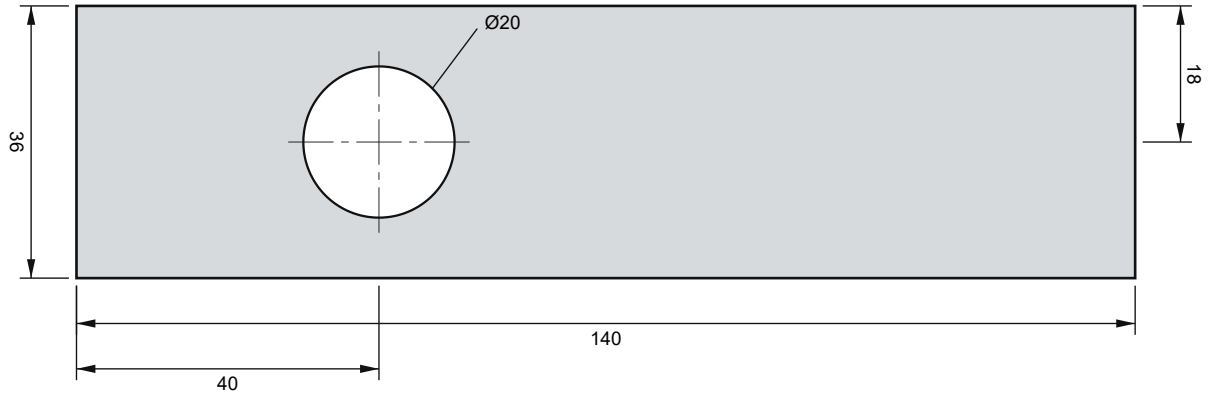

Zijaanzicht




Plaat

S235, plaat 8 mm

36 x 140 x 8 mm

Lasersnijden op de DXF; braam eraf

Waar het stuk zit

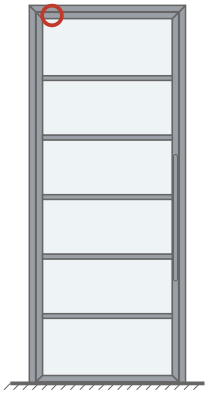

Bewerking en verbindingen


Bewerking: Ø20 voor de bovenpen; in de bovenregel gelast

Titel: **Pos 12: Taatsplaat boven**			
Deur: Ladder · opening 1000 x 2400		Tekeningnummer: **TD-14-12**	
Maten en toleranties: mm · ISO 2768-m · eerste hoek	Opgesteld: Ian · laswerken	Uitgifte: 2026-11-10	Blad: 12 / 15


13 2 x Greephouder

S235, plaat 10 mm · 25 x 40 · 0,08 kg/st


Aanzicht (2:1)

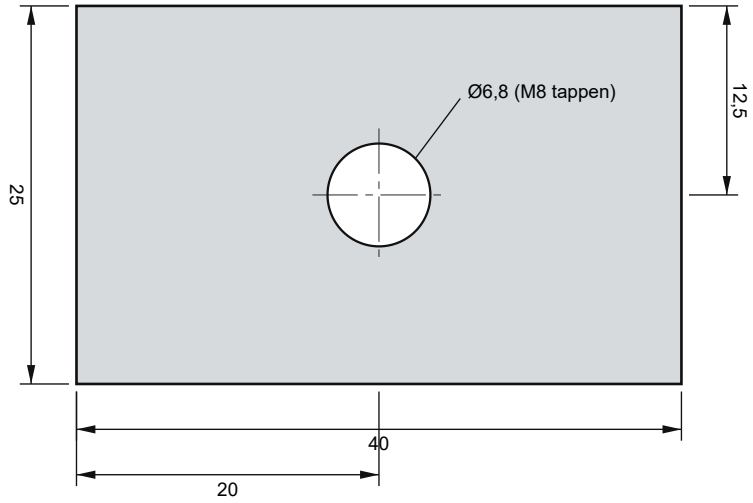

Zijaanzicht

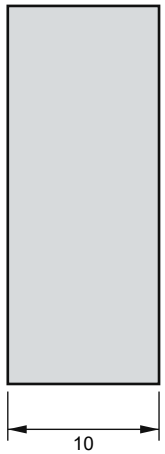

Waar het stuk zit

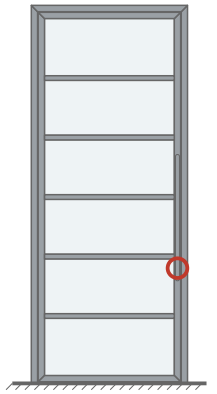

Plaat

S235, plaat 10 mm

25 x 40 x 10 mm

Lasersnijden op de DXF; braam eraf

Bewerking en verbindingen


Bewerking: M8 tappen (boor Ø6,8); op de staander gelast

Titel: **Pos 13: Greephouder**			
Deur: Ladder · opening 1000 x 2400		Tekeningnummer: **TD-14-13**	
Maten en toleranties: mm · ISO 2768-m · eerste hoek	Opgesteld: Ian · laswerken	Uitgifte: 2026-11-10	Blad: 13 / 15


14 2 x Ruit

gelaagd 44.2 helder · 830 x 370 · 6,38 kg/st

Aanzicht (1:10): daglicht, de ruit is 4 mm groter rondom

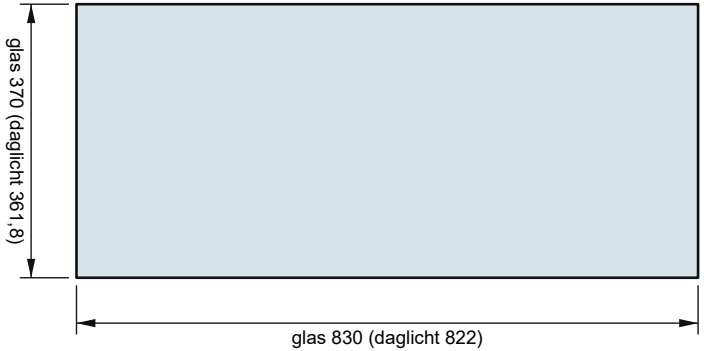

Waar het stuk zit

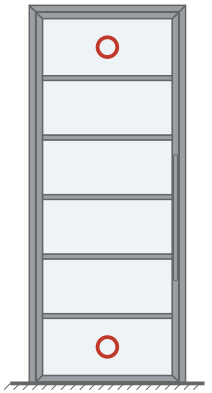

Opbouw (2:1)



gelaagd 44.2 helder

altijd veiligheidsglas (EN 12543 / EN 12150)

Bewerking en verbindingen

Bewerking: veiligheidsglas; glasmaat = daglicht + 4 rondom


Titel: **Pos 14: Ruit**			
Deur: Ladder · opening 1000 x 2400		Tekeningnummer: **TD-14-14**	
Maten en toleranties: mm · ISO 2768-m · eerste hoek	Opgesteld: Ian · laswerken	Uitgifte: 2026-11-10	Blad: 14 / 15

15


4 x Ruit

gelaagd 44.2 helder · 830 x 355 · 6,12 kg/st

Aanzicht (1:10): daglicht, de ruit is 4 mm groter rondom

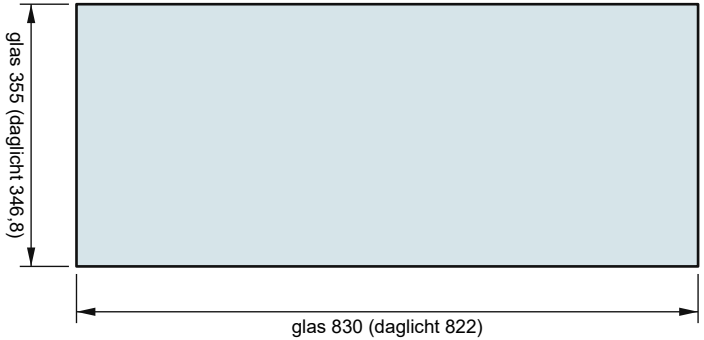

Waar het stuk zit

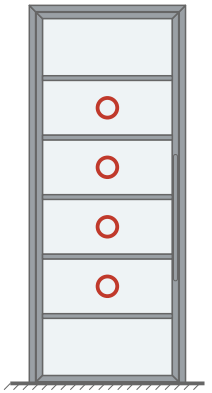

Opbouw (2:1)



gelaagd 44.2 helder

altijd veiligheidsglas (EN 12543 / EN 12150)

Bewerking en verbindingen

Bewerking: veiligheidsglas; glasmaat = daglicht + 4 rondom

Titel: **Pos 15: Ruit**			
Deur: Ladder · opening 1000 x 2400		Tekeningnummer: **TD-14-15**	
Maten en toleranties: mm · ISO 2768-m · eerste hoek	Opgesteld: Ian · laswerken	Uitgifte: 2026-11-10	Blad: 15 / 15