
Vooraanzicht (schaal 1:15), van de kant met de greep

Rode streep-punt: hart taatsas. Maten in mm; roedehoogtes op het hart, vanaf de onderkant van de vleugel.

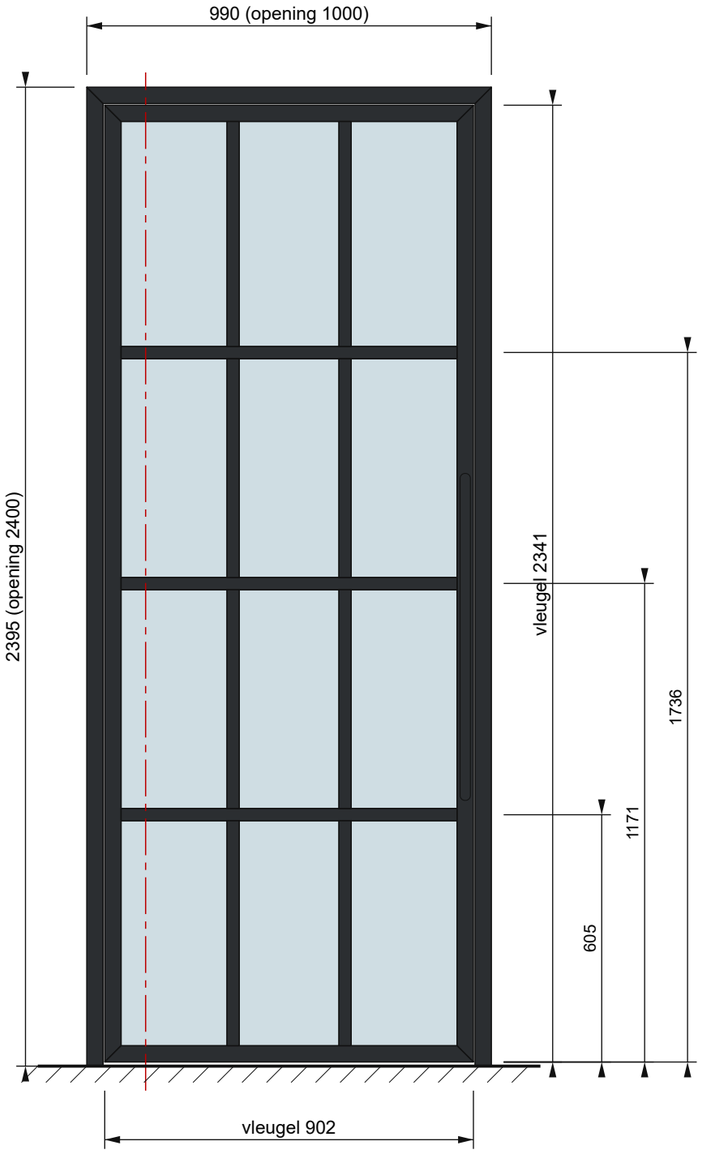

Zaaglijst (staven)

Zaaglijst	Staaf	Lengte	n	Bewerking
kozijn: stijl	koker40x40x2	2395	2	onder recht (op de vloer), boven verstek
kozijn: regel	koker40x40x2	990	1	verstek of stomp tegen de stijl
vleugel: staander	koker40x40x2	2341	2	verstek 45° aan beide kanten
vleugel: regel	koker40x40x2	902	2	verstek 45° aan beide kanten
vleugel: roede	plat20x10	822	3	recht, tussen kader en roeden
vleugel: lat op de roede	plat30x3	822	6	voor gelast, achter geschroefd
vleugel: roede	plat20x10	550	4	recht, tussen kader en roeden
vleugel: lat op de roede	plat30x3	550	8	voor gelast, achter geschroefd
vleugel: roede	plat20x10	535	4	recht, tussen kader en roeden
vleugel: lat op de roede	plat30x3	535	8	voor gelast, achter geschroefd
vleugel: glaslatten in het kader (voor en achter)	plat15x4	6166	2	in stukken op maat zagen bij het glazen
greep voor en achter	rond25	800	2	uiteinden rond slijpen; 2 gaten M8 per greep


Laserlijst (DXF bij de configurator)

Lasergesneden	Maat	n	Plaat / opmerking
taatsplaat onder (in de onderregel)	36 x 220	1	S235, plaat 8 mm; 2 gaten M8 voor het scharnier
taatsplaat boven (in de bovenregel)	36 x 140	1	S235, plaat 8 mm; boring Ø20 voor de bovenpen
greephouder (afstandsstuk)	25 x 40	2	S235, plaat 10 mm; boring M8 voor de greep

Glaslijst (glasmaat = daglicht + 4 mm rondom)

Glas	Vorm	Breedte	Hoogte	m²	n
vleugel	rechthoek	267	558	0,15	4
vleugel	rechthoek	252	558	0,14	2
vleugel	rechthoek	267	543	0,14	4
vleugel	rechthoek	252	543	0,14	2

Doorsnede A-A (1:2): kader, veiligheidsglas, glaslatten, roede

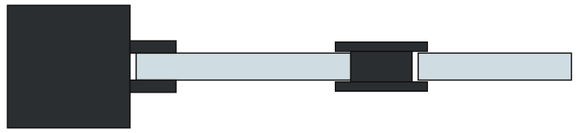


koker 40x40x2, hoeken in verstek (45°); kern platstaal 20x10 met voor en achter een lat 30x3 over het glas

Kostprijs	€
Materiaal	1139
Arbeid (23,11 u)	1040
Totaal (excl. btw)	2179

Eigenaar **Ian · laswerken**	Bibliotheek Stalen deuren		
Titel **Deur Raster twaalf · opening 1000 x 2400**			
Systeem Koker en strip	Tekeningnummer **TD-22**	Rev. 1	Uitgifte 2026-11-10
Maten en toleranties mm · ISO 2768-m · lassen ISO 5817-C	Schaal 1:15 (A3)	Opgesteld Ian · laswerken	Blad 1 / 9


Opengewerkte tekening: de stalen delen uit elkaar, gezien van de kant met de greep

Rood: verstek 45° (zagen in verstek). Stippellijn: deze twee stukken komen hier aan elkaar; de code staat in de tabel rechts.

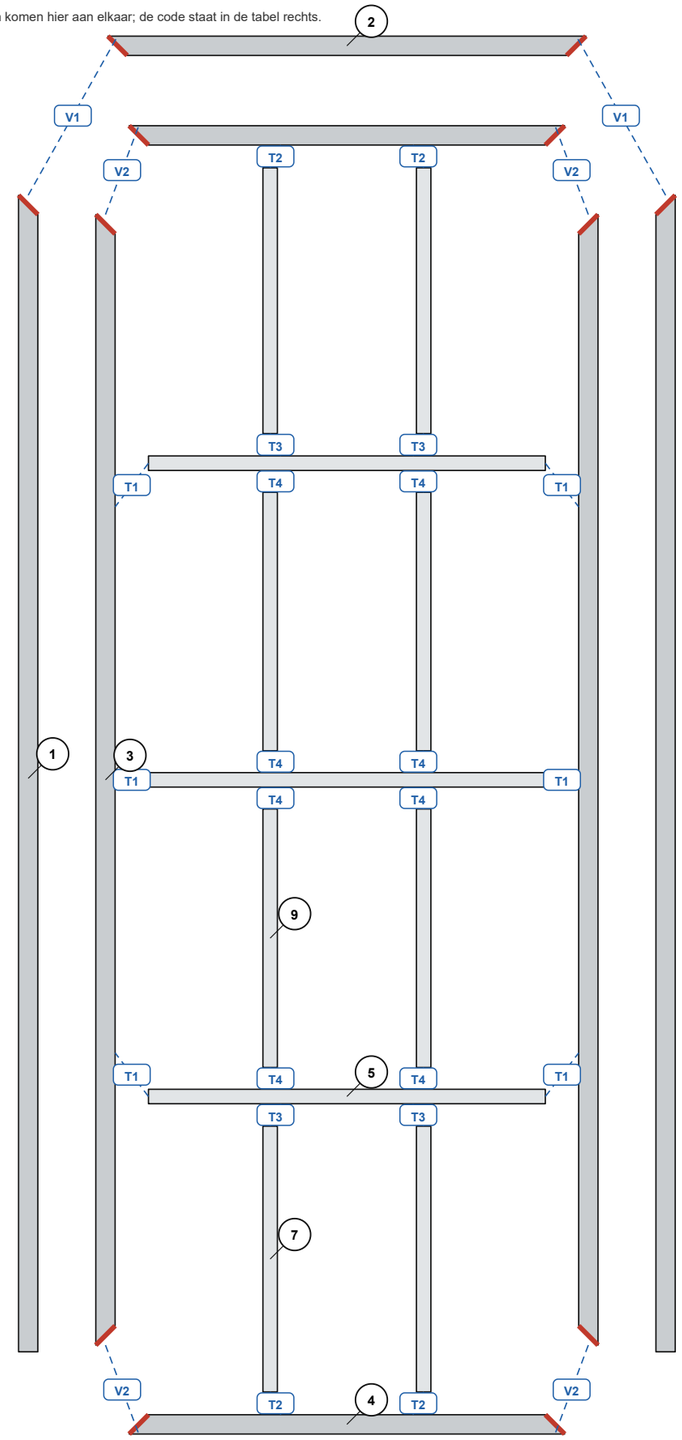


Verbindingen

Code	n	Stuk	tegen stuk	Soort
V1	2	1 Kozijn: stijl	2 Kozijn: bovenregel	Verstek 45°
V2	4	3 Kader: staander	4 Kader: regel	Verstek 45°
T1	6	3 Kader: staander	5 Roede horizontaal: kern	T-verbinding (stomp)
T2	4	4 Kader: regel	7 Roede verticaal: kern	T-verbinding (stomp)
T3	4	5 Roede horizontaal: kern	7 Roede verticaal: kern	T-verbinding (stomp)
T4	8	5 Roede horizontaal: kern	9 Roede verticaal: kern	T-verbinding (stomp)

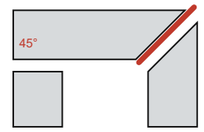

Verstek 45°

Hechten binnen en buiten; de zichtkant doorlassen met TIG (ER70S-6 Ø1,6, 90-110 A), de binnenkant MIG (G3Si1 Ø0,8); zichtkant vlak slijpen. Beurtelings lassen, diagonalen meten.

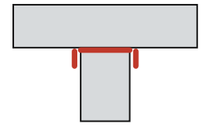

T-verbinding (stomp)

Stomp tegen het kader, het kozijn of de roede; hoeklas a3 rondom, TIG aan de zichtkant, MIG binnen; zichtkant vlak slijpen.

Latten op de roeden (30x3): voor gehecht om de 150 en gelast, achter geschroefd met M4 verzonken om de 250.


Eigenaar **Ian · laswerken**	Bibliotheek Stalen deuren		
Titel **Opengewerkte tekening Raster twaalf · opening 1000 x 2400**			
Systeem Koker en strip	Tekeningnummer **TD-22**	Rev. 1	Uitgifte 2026-11-10
Maten en toleranties mm · ISO 2768-m · lassen ISO 5817-C	Schaal schets	Opgesteld Ian · laswerken	Blad 2 / 9

Deurprofielen: Koker en strip

Eigen staven uit de staalhandel. Voor = de kant met de greep (boven in de doorsnede).

Kozijn


koker 40x40x2

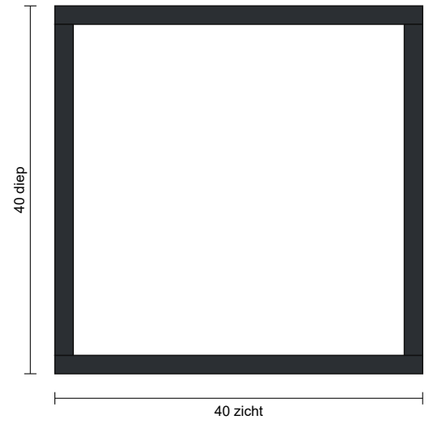

Doorsnede 1.5:1 · 40 x 40 · wand 2
2,31 kg/m · staven van 6 m (staalhandel)
3 stukken: pos 1, 2
zagen 90°/45°, 45°/45°

Vleugel (kader)


koker 40x40x2

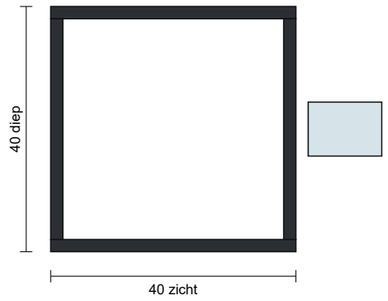

Doorsnede 1:1 · 40 x 40 · wand 2
2,31 kg/m · staven van 6 m (staalhandel)
4 stukken: pos 3, 4
zagen 45°/45°

Roede

platstaal 20x10

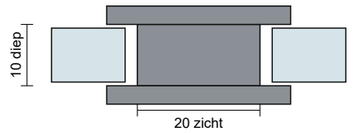

Doorsnede 1:1 · 20 x 10
1,57 kg/m · staven van 6 m (staalhandel)
11 stukken: pos 5, 7, 9
zagen 90°/90°

Glaslat


platstaal 15x4



Doorsnede 2:1 · 15 x 4
0,47 kg/m · staven van 6 m (staalhandel)
28 stukken: pos 11, 12, 13, 14


Hoe de stukken samenkomen (vooraanzicht 1:2; rood = zaagsnede in verstek 45°, stippellijn = wand achter de zichtkant)

Hoek van de vleugel: verstek

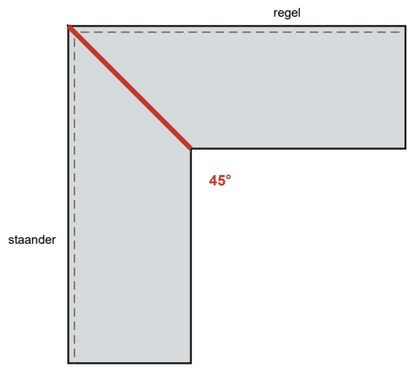


Beide stukken 45° zagen (pos 3, 4).
TIG zichtkant, MIG binnen; vlak slijpen.
Diagonalen gelijk (± 1 mm) voor je last.

Roede tegen het kader: stomp (T)

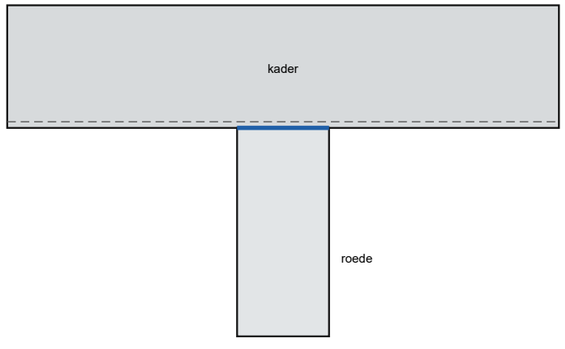

Roede recht zagen op de daglichtmaat.
Kern op afstandsblokjes in het midden van de diepte.
Hoeklas rondom (blauw), vlak slijpen.


Kozijn: boven verstek, onder recht

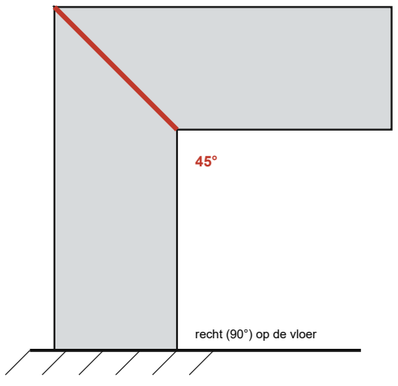

Bovenregel en stijlen boven 45° (pos 1, 2, 27).
De stijlen staan onderaan recht op de vloer.
Taatspot in de vloer, bovenpen in de bovenregel.

Eigenaar: **Ian · laswerken**	Bibliotheek: Stalen deuren		
Titel: **Deurprofielen Raster twaalf · opening 1000 x 2400**			
Systeem: Koker en strip	Tekeningnummer: **TD-22**	Rev.: 1	Uitgifte: 2026-11-10
Maten en toleranties: mm · ISO 2768-m · lassen ISO 5817-C	Schaal: zie bij de tekening	Opgesteld: Ian · laswerken	Blad: 3 / 9

Samenstelling (vooraanzicht van de kant met de greep)

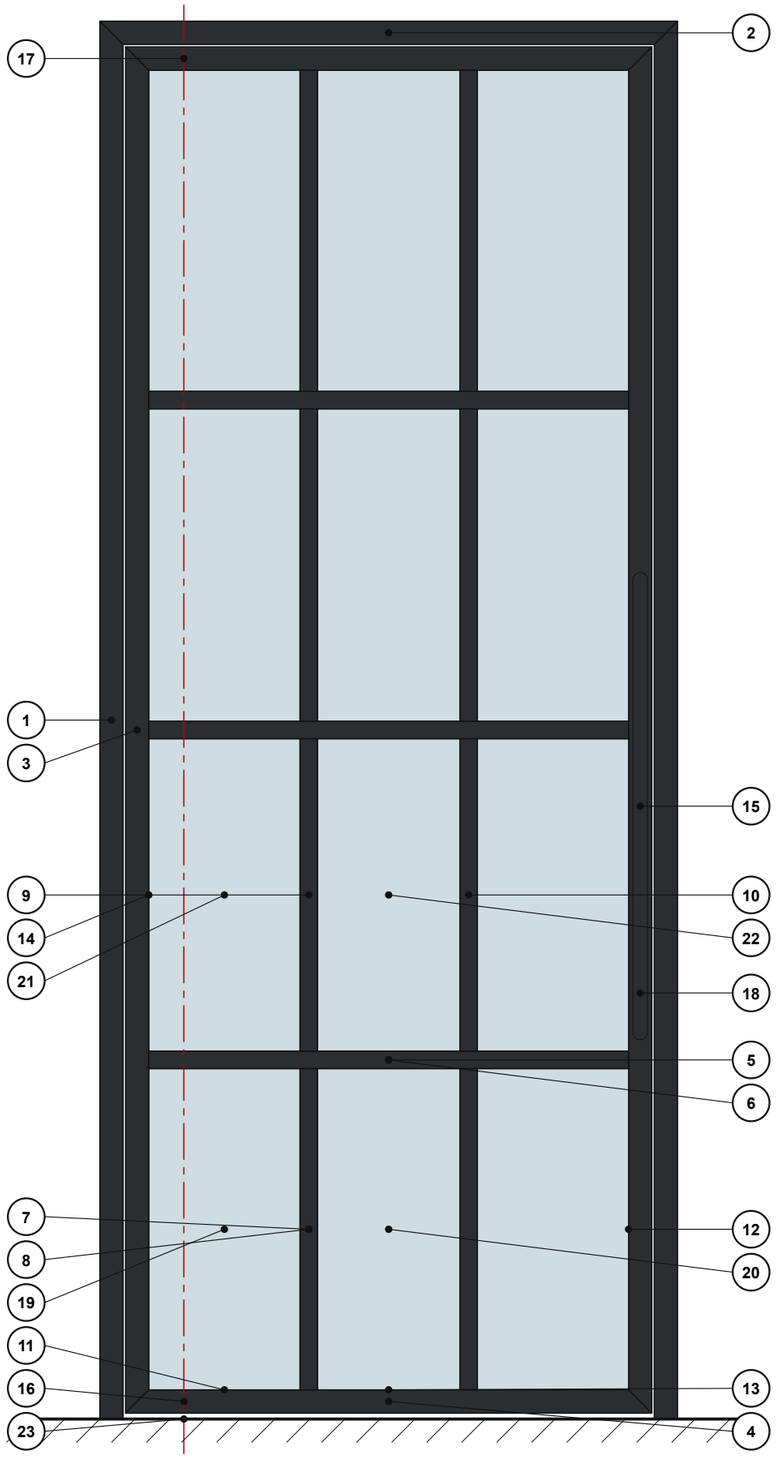

Stuklijst (ISO 7573) · Zagen: hoek van beide uiteinden tegen de as (90° = recht, 45° = verstek)

Pos	n	Benaming	Materiaal, profiel	Maat	Zagen	kg/st	kg
1	2	Kozijn: stijl	S235, koker 40x40x2	L = 2395	90°/45°	5,53	11,1
2	1	Kozijn: bovenregel	S235, koker 40x40x2	L = 990	45°/45°	2,29	2,3
3	2	Kader: staander	S235, koker 40x40x2	L = 2341	45°/45°	5,41	10,8
4	2	Kader: regel	S235, koker 40x40x2	L = 902	45°/45°	2,08	4,2
5	3	Roede horizontaal: kern	S235, platstaal 20x10	L = 822	90°/90°	1,29	3,9
6	6	Roede horizontaal: lat voor en achter	S235, platstaal 30x3	L = 822	90°/90°	0,58	3,5
7	4	Roede verticaal: kern	S235, platstaal 20x10	L = 550	90°/90°	0,86	3,5
8	8	Roede verticaal: lat voor en achter	S235, platstaal 30x3	L = 550	90°/90°	0,39	3,1
9	4	Roede verticaal: kern	S235, platstaal 20x10	L = 535	90°/90°	0,84	3,4
10	8	Roede verticaal: lat voor en achter	S235, platstaal 30x3	L = 535	90°/90°	0,38	3
11	8	Glaslat	S235, platstaal 15x4	L = 259		0,12	1
12	8	Glaslat	S235, platstaal 15x4	L = 550		0,26	2,1
13	4	Glaslat	S235, platstaal 15x4	L = 244		0,11	0,5
14	8	Glaslat	S235, platstaal 15x4	L = 535		0,25	2
15	2	Greep (voor en achter)	S235, rond Ø25	L = 800		3,08	6,2
16	1	Taatsplaat onder	S235, plaat 8 mm	36 x 220		0,5	0,5
17	1	Taatsplaat boven	S235, plaat 8 mm	36 x 140		0,32	0,3
18	2	Greephouder	S235, plaat 10 mm	25 x 40		0,08	0,2
19	4	Ruit	gelaagd 44.2 helder	267 x 558		3,1	12,4
20	2	Ruit	gelaagd 44.2 helder	252 x 558		2,92	5,8
21	4	Ruit	gelaagd 44.2 helder	267 x 543		3,02	12,1
22	2	Ruit	gelaagd 44.2 helder	252 x 543		2,85	5,7
23	1	Taatsscharnier Argenta Pivotica Pro 150 (pot, as en bovenpen)	inkoop				
24	52	Schroef M4 x 12 verzonken, RVS (ISO 10642)	A2				
25	24	Glasblokje 3 mm	kunststof				
26	3	Glaskit transparant (koker 310 ml)	MS-polymeer				
27	6	Kozijnanker Ø8	verzinkt				
		Totaal staal en glas					97,3


Eigenaar **Ian · laswerken**	Bibliotheek Stalen deuren		
Titel **Stuklijst Raster twaalf · opening 1000 x 2400**			
Systeem Koker en strip	Tekeningnummer **TD-22**	Rev. 1	Uitgifte 2026-11-10
Maten en toleranties mm · ISO 2768-m · lassen ISO 5817-C	Schaal 1:11 (A3)	Opgesteld Ian · laswerken	Blad 4 / 9


Onderdelen (schetsen, niet op schaal; maten in mm)

1 2 x Kozijn: stijl

5,53 kg/st

S235, koker 40x40x2 · L = 2395

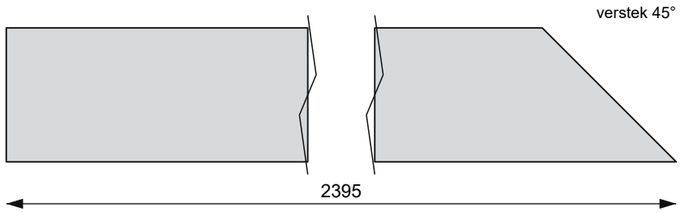

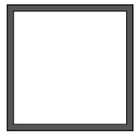



recht · verstek 45°

2 1 x Kozijn: bovenregel

2,29 kg/st

S235, koker 40x40x2 · L = 990

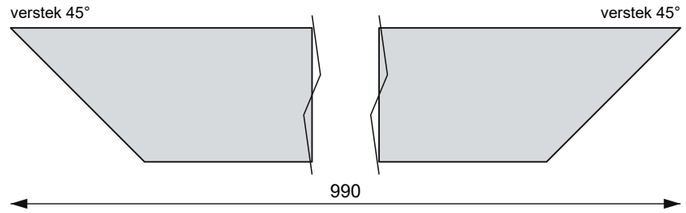

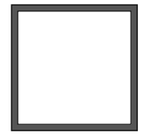



verstek 45° · verstek 45°

3 2 x Kader: staander

5,41 kg/st

S235, koker 40x40x2 · L = 2341

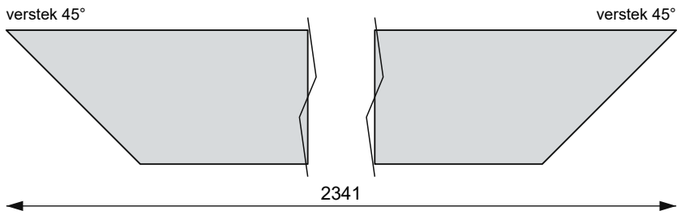

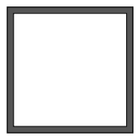



verstek 45° · verstek 45°

4 2 x Kader: regel

2,08 kg/st

S235, koker 40x40x2 · L = 902

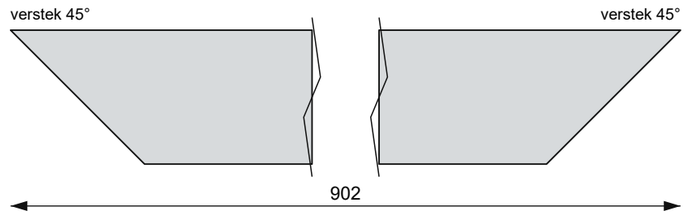

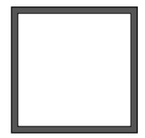


verstek 45° · verstek 45°

5 3 x Roede horizontaal: kern

1,29 kg/st

S235, platstaal 20x10 · L = 822

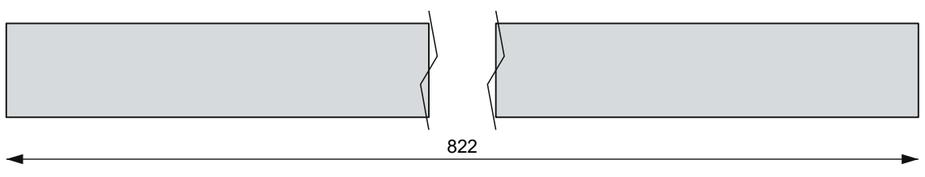




recht · recht; M4 om de 250 aan de achterkant

6 6 x Roede horizontaal: lat voor en achter

0,58 kg/st

S235, platstaal 30x3 · L = 822

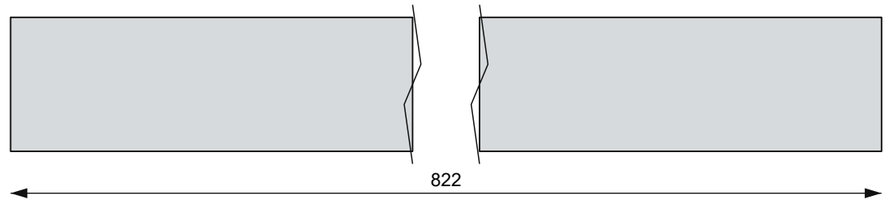



recht · recht; voor gelast, achter geschroefd


Eigenaar **Ian · laswerken**	Bibliotheek Stalen deuren		
Titel **Onderdelen Raster twaalf · opening 1000 x 2400**			
Systeem Koker en strip	Tekeningnummer **TD-22**	Rev. 1	Uitgifte 2026-11-10
Maten en toleranties mm · ISO 2768-m · lassen ISO 5817-C	Schaal schetsen	Opgesteld Ian · laswerken	Blad 5 / 9

Onderdelen (schetsen, niet op schaal; maten in mm) (vervolg 2)

7 4 x Roede verticaal: kern

0,86 kg/st

S235, platstaal 20x10 · L = 550

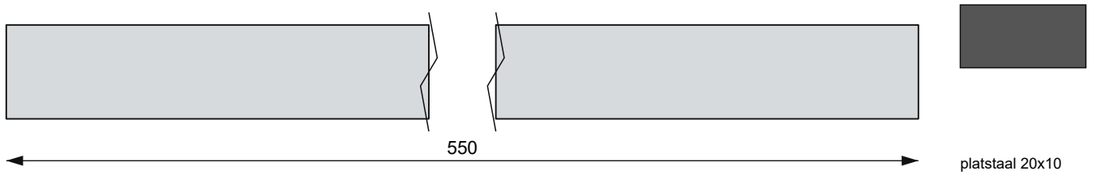


recht · recht; M4 om de 250 aan de achterkant

8 8 x Roede verticaal: lat voor en achter

0,39 kg/st

S235, platstaal 30x3 · L = 550

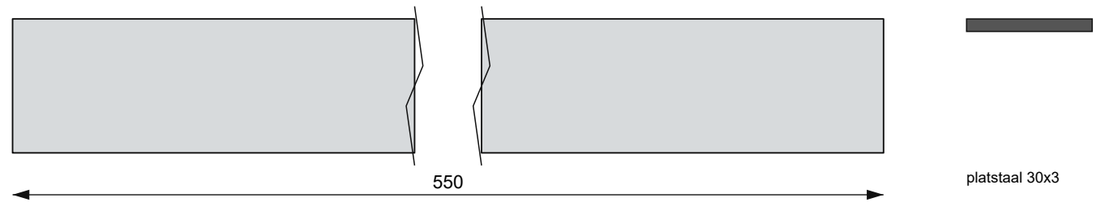


recht · recht; voor gelast, achter geschroefd

9 4 x Roede verticaal: kern

0,84 kg/st

S235, platstaal 20x10 · L = 535

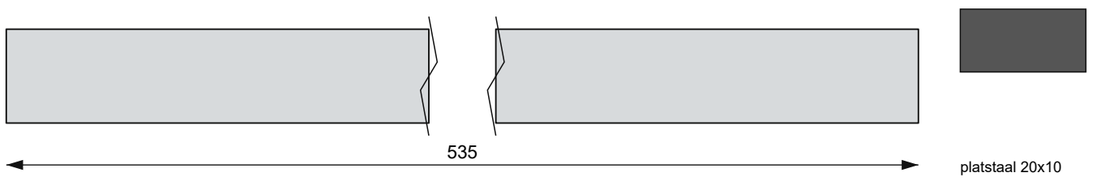


recht · recht; M4 om de 250 aan de achterkant

10 8 x Roede verticaal: lat voor en achter

0,38 kg/st

S235, platstaal 30x3 · L = 535

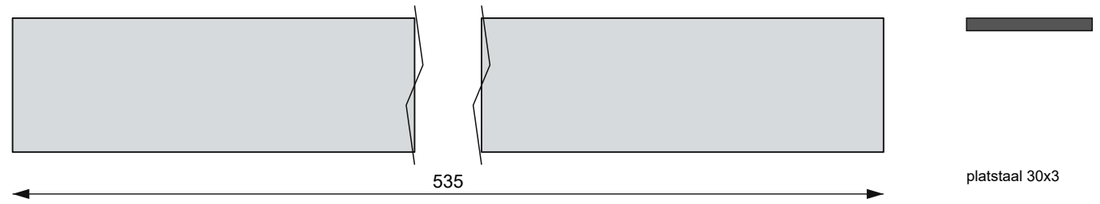


recht · recht; voor gelast, achter geschroefd

11 8 x Glaslat

0,12 kg/st

S235, platstaal 15x4 · L = 259

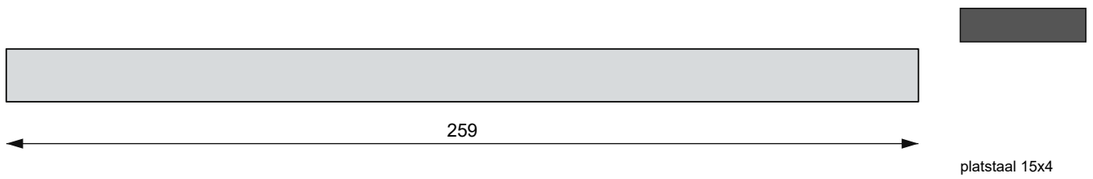


recht; voor gelast, achter geschroefd (M4 verzonken om de 250)

12 8 x Glaslat

0,26 kg/st

S235, platstaal 15x4 · L = 550

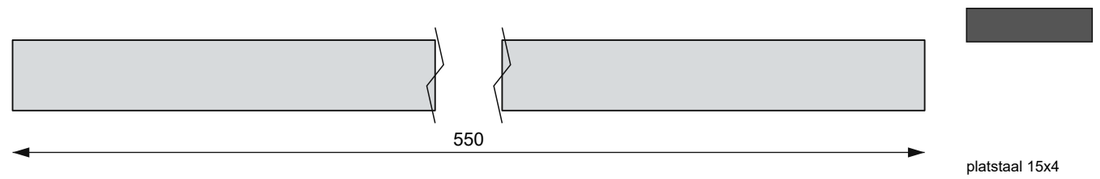

recht; voor gelast, achter geschroefd (M4 verzonken om de 250)


Eigenaar **Ian · laswerken**	Bibliotheek Stalen deuren		
Titel **Onderdelen Raster twaalf · opening 1000 x 2400**			
Systeem Koker en strip	Tekeningnummer **TD-22**	Rev. 1	Uitgifte 2026-11-10
Maten en toleranties mm · ISO 2768-m · lassen ISO 5817-C	Schaal schetsen	Opgesteld Ian · laswerken	Blad 6 / 9

Onderdelen (schetsen, niet op schaal; maten in mm) (vervolg 3)

13 4 x Glaslat

0,11 kg/st

S235, platstaal 15x4 · L = 244

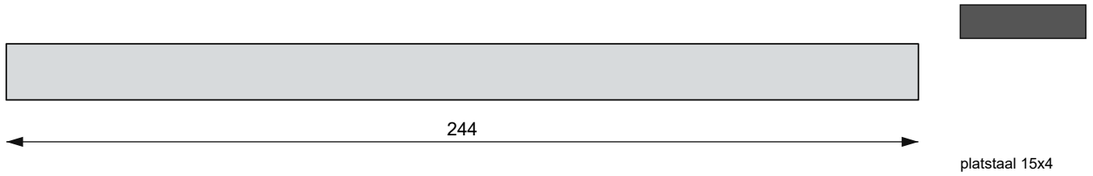


recht; voor gelast, achter geschroefd (M4 verzonken om de 250)

14 8 x Glaslat

0,25 kg/st

S235, platstaal 15x4 · L = 535

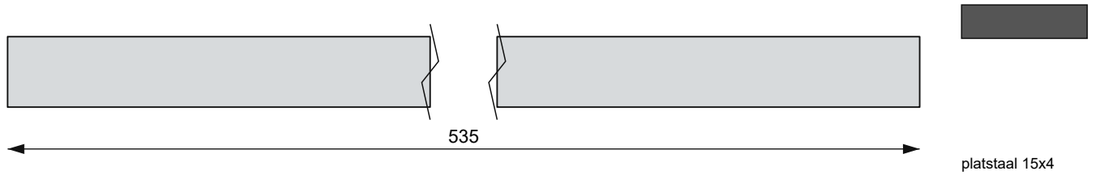


recht; voor gelast, achter geschroefd (M4 verzonken om de 250)

15 2 x Greep (voor en achter)

3,08 kg/st

S235, rond Ø25 · L = 800

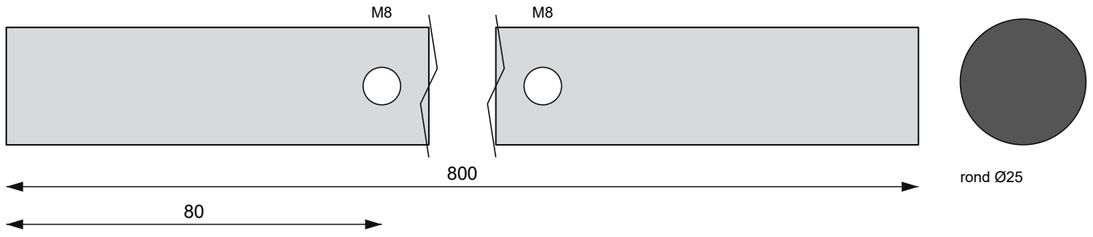


uiteinden rond slijpen; 2 x M8 op 80 van de uiteinden

16 1 x Taatsplaat onder

0,5 kg/st

S235, plaat 8 mm · 36 x 220

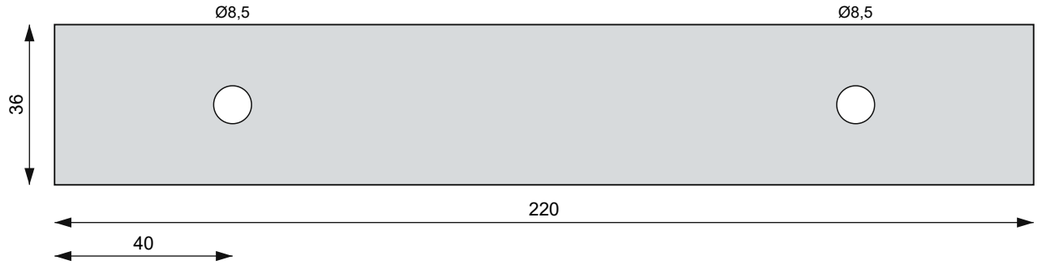


2 x Ø8,5 voor het scharnier; in de onderregel gelast

17 1 x Taatsplaat boven

0,32 kg/st

S235, plaat 8 mm · 36 x 140

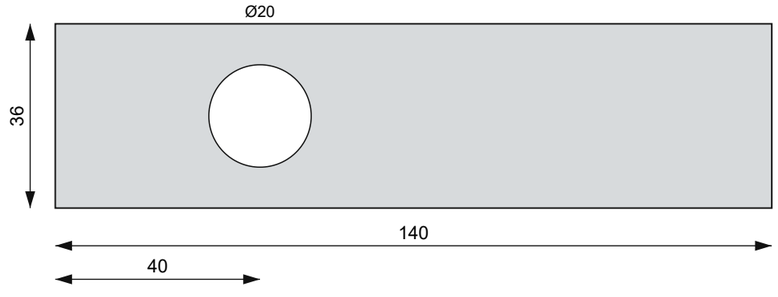


Ø20 voor de bovenpen; in de bovenregel gelast

18 2 x Greephouder

0,08 kg/st

S235, plaat 10 mm · 25 x 40

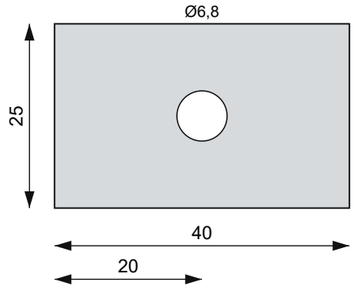


M8 tappen (boor Ø6,8); op de staander gelast

Eigenaar: **Ian · laswerken**	Bibliotheek: Stalen deuren		
Titel: **Onderdelen Raster twaalf · opening 1000 x 2400**			
Systeem: Koker en strip	Tekeningnummer: **TD-22**	Rev.: 1	Uitgifte: 2026-11-10
Maten en toleranties: mm · ISO 2768-m · lassen ISO 5817-C	Schaal: schetsen	Opgesteld: Ian · laswerken	Blad: 7 / 9

Onderdelen (schetsen, niet op schaal; maten in mm) (vervolg 4)

19 **4 x Ruit** 3,1 kg/st


gelaagd 44.2 helder · 267 x 558

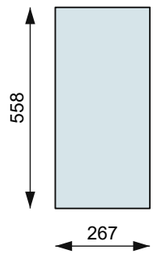

veiligheidsglas; glasmaat = daglicht + 4 rondom

20 **2 x Ruit** 2,92 kg/st

gelaagd 44.2 helder · 252 x 558

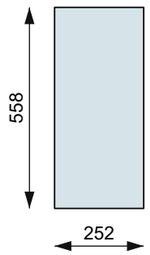

veiligheidsglas; glasmaat = daglicht + 4 rondom

21 **4 x Ruit** 3,02 kg/st

gelaagd 44.2 helder · 267 x 543

veiligheidsglas; glasmaat = daglicht + 4 rondom

22 **2 x Ruit** 2,85 kg/st

gelaagd 44.2 helder · 252 x 543

veiligheidsglas; glasmaat = daglicht + 4 rondom

Eigenaar **Ian · laswerken**	Bibliotheek Stalen deuren		
Titel **Onderdelen Raster twaalf · opening 1000 x 2400**			
Systeem Koker en strip	Tekeningnummer **TD-22**	Rev. 1	Uitgifte 2026-11-10
Maten en toleranties mm · ISO 2768-m · lassen ISO 5817-C	Schaal schetsen	Opgesteld Ian · laswerken	Blad 8 / 9


Bestellijst (staven van de handel)

Artikel	Profiel	Bestellen	m	nodig m	rest	€/m	€
–	koker 40x40x2	3 x 6 m	18	12,3	32 %	10,13	182
–	platstaal 30x3	3 x 6 m	18	13,6	24 %	3,9	70
–	platstaal 15x4	3 x 6 m	18	11,7	35 %	2,6	47
–	platstaal 20x10	2 x 6 m	12	6,8	43 %	8,64	104
–	rond Ø25	1 x 6 m	6	1,6	73 %	21,2	127
	Totaal profielen (excl. btw)						530


Zaagsnede 4 mm per stuk; lengtes = buitenmaat van het stuk (verstek inbegrepen). Prijzen: zie de bron per profiel op de pagina Werkplaats.

Zaagplan: elke balk is één staaf; de nummers zijn de posities uit de stuklijst


koker 40x40x2

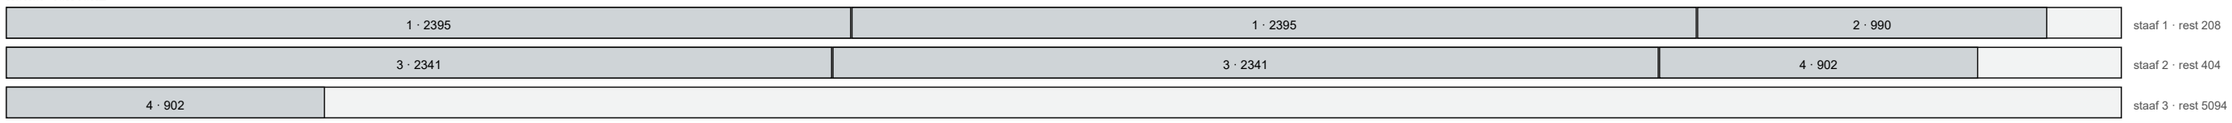


platstaal 30x3

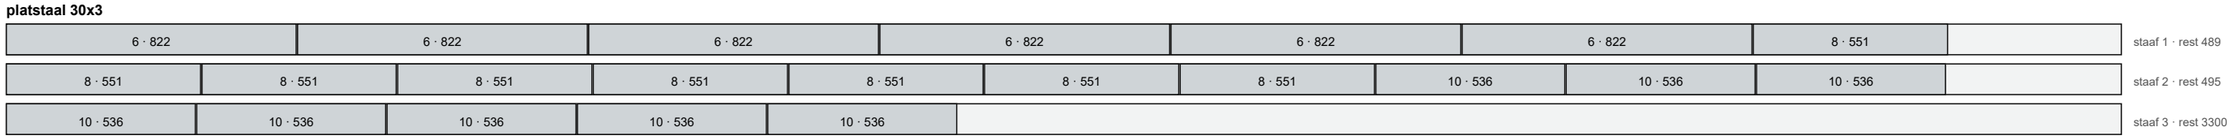

platstaal 15x4

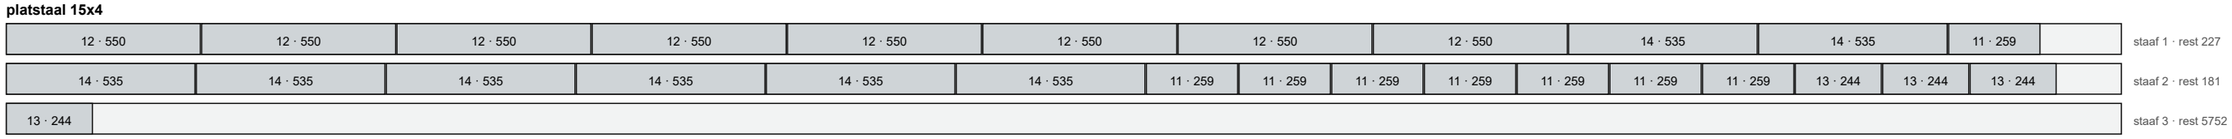

platstaal 20x10

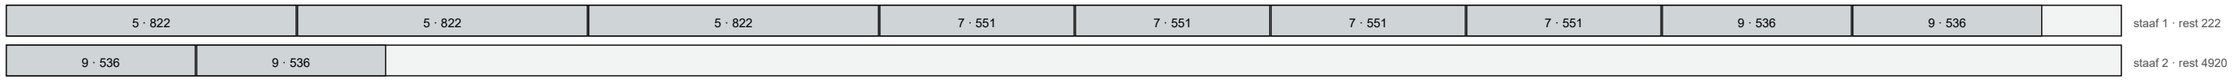

rond Ø25



Eigenaar **Ian · laswerken**	Bibliotheek Stalen deuren		
Titel **Bestellijst en zaagplan Raster twaalf · opening 1000 x 2400**			
Systeem Koker en strip	Tekeningnummer **TD-22**	Rev. 1	Uitgifte 2026-11-10
Maten en toleranties mm · ISO 2768-m · lassen ISO 5817-C	Schaal	Opgesteld Ian · laswerken	Blad 9 / 9

Taatsdeur Raster twaalf opening 1000 x 2400 mm · Koker en strip

Twee verticale en drie horizontale roeden: twaalf vakken.

Kostprijs (excl. btw)

Wat	Bedrag	Bron
Staven (zaaglijst, + 10 % zaagverlies)	€ 332,34	metallshopper.de en schattingen per staaf
Lasersnijden (0.97 kg, 4 delen)	€ 16,37	schatting (geen publieke prijs gevonden): plaat S235 + snijden
Glas: gelaagd 44.2 helder (12 ruiten)	€ 184,18	glasopmaat.be
Scharnier: Pivot: Argenta Pivotica Pro 150 x 1	€ 242,37	beslist.be
Stralen en poedercoaten RAL 9005 Gitzwart (3.89 m²)	€ 253,13	structuurlak, 1 laag, per m²: https://www.betuwe-poedercoating.nl/prijzen
Lasdraad, gas, TIG-draad	€ 75,92	G3Si1 Ø0,8, 15 kg € 61,50: https://www.weldingshop.nl/en/products/lasdraad-mig-staal-d300-sg2-0-8mm-15kg; K15 20 l (± 4000 l gas) € 49 incl. btw: https://www.weld-toorts.be/category/55/Gasfless en
Kit, blokjes, schroeven, schijven	€ 35,00	schatting
Materiaal	**€ 1.139,31**	
Arbeid: 23,11 uur x € 45,00	€ 1.039,95	uren uit de werkwijze hieronder (instelbaar)
Kostprijs	**€ 2.179,26**	
Verkoopprijs met 35 % marge	**€ 2.942,00**	**incl. btw: € 3.559,82**

Gewicht: staal 62 kg, glas 36 kg; per vleugel 84 kg. Pivot: Argenta Pivotica Pro 150: draagt dat ruim. Oppervlak voor de coating 3,89 m².

Werkwijze

1. **Voorbereiden en zagen** 3,14 u
   Zaag de 44 stukken volgens de zaaglijst; kader en kozijn in verstek 45°, roeden recht. Ontbramen en elk stuk merken. Laat de taatsplaten en greephouders lasersnijden of zaag ze uit platstaal.
2. **Kader opspannen op de lastafel** 0,6 u
   Leg de kaderdelen op de lastafel en zet ze vast met haakse aanslagen en klemmen in het Ø28-raster. Meet de diagonalen (gelijk tot 1 mm) voor je hecht.
3. **Kader hechten en lassen** 1,8 u · TIG zichtkant · MIG binnen
   6 verstekhoeken: hecht binnen en buiten, las de zichtkant met TIG (ER70S-6 Ø1,6, 90-110 A) en de binnenkant met MIG/MAG (G3Si1 Ø0,8, 18 V, Ar/CO_2). Las beurtelings tegenover elkaar, zodat het kader vlak blijft. Slijp de zichtkant vlak (korrel 80, daarna een fiberschijf 120).
4. **Roeden plaatsen** 3,3 u · TIG
   11 roeden: leg de kern 20x10 op afstandsblokken zodat ze in het midden van de diepte ligt (glas in het midden). Hecht ze en las ze rondom met TIG; slijp ze vlak.
5. **Taatsplaten en greephouders** 0,6 u · MIG
   Las de taatsplaat onder in de onderregel en de taatsplaat boven in de bovenregel. Leg ze op het hart van de taatsas: 100 mm uit de scharnierkant. Boor en tap de gaten volgens het scharnier. Las 2 greephouders op de staander aan de sluitkant (hart 20 uit de rand).
6. **Glaslatten en latten op de roeden** 4,67 u · TIG punten
   Hecht de vaste latten aan de voorkant om de 150 mm (25,9 m lat). Boor de losse latten aan de achterkant Ø3,3 en verzink ze. Tap in de kern en het kader M4 om de 250 mm (52 gaten).
7. **Richten en nameten** 0,5 u
   Meet de vlakheid op de lastafel (ten hoogste 2 mm over de hoogte) en de diagonalen. Richt zo nodig koud of met een kleine vlam. Breek alle randen.

8. **Klaarmaken voor de coater** 0,8 u
   Ontvetten, de getapte gaten afstoppen (siliconenpluggen), merken. Laten stralen (SA 2½) en poedercoaten in RAL 9005 structuur.
9. **Glazen** 4,7 u
   12 ruiten veiligheidsglas. Leg glasblokjes (3 mm) onder elke ruit, kit tegen de vaste lat (transparante glaskit), zet de losse latten met M4 verzonken RVS.
10. **Plaatsen** 3 u
    Stel het kozijn waterpas en loodrecht in de opening en veranker het (6 x 8 mm). Boor de taatspot in de vloer op het hart van de as, monteer de bovenpen in het kozijn, en hang en stel de deur. Budgetscharnier: de stelschroef op 1-2 mm speling onder de deur.

Ter vergelijking, verkoopprijzen in BE/NL: Zelfbouwmarkt.be: pivoterende stalen deur 3W Tirza 880 x 2040 (4 mm glas) € 899,00; Zelfbouwmarkt.be: op maat tot 1200 x 2300, vanaf € 1.200,00; Stalen Deuren Centrum (NL): enkele taatsdeur vanaf (incl. btw, zonder plaatsen; plaatsen € 450) € 1.350,00; De Rooy Steel Doors: taatsdeur met FritsJurgens, geplaatst, vanaf € 2.195,00.