
1


2 x Kozijn: stijl

S235, koker 40x40x2 · L = 2395 · zagen 90°/45° · 5,53 kg/st


Aanzicht (1:20)

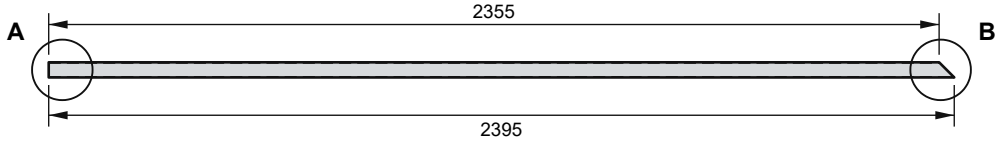

Waar het stuk zit

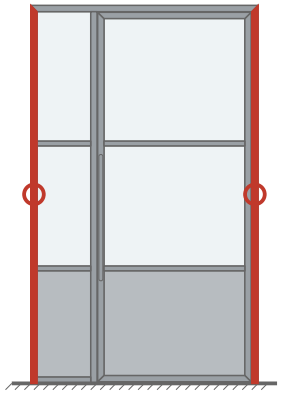


Detail A (1:1): linker uiteinde

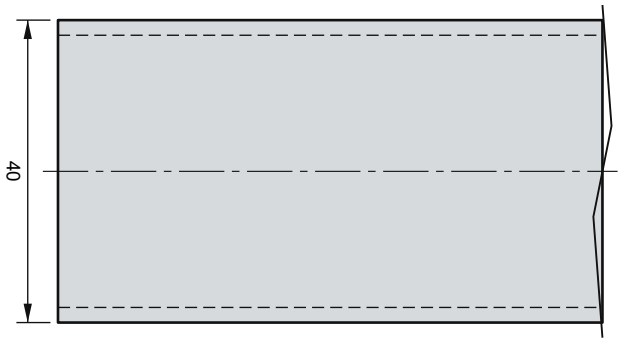


Recht afzagen (90°)

Detail B (1:1): rechter uiteinde

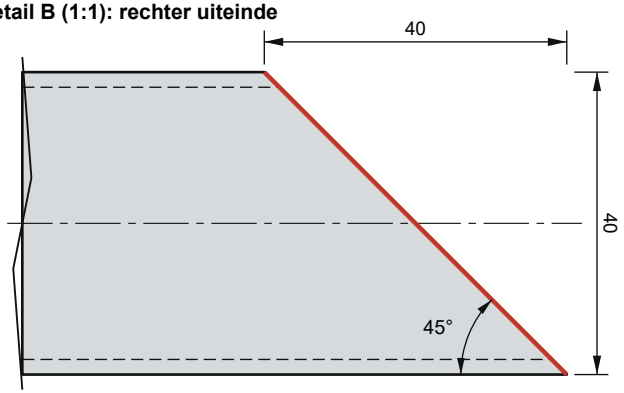

Verstek 45°: lange kant is 40 langer dan de korte

Doorsnede van het profiel

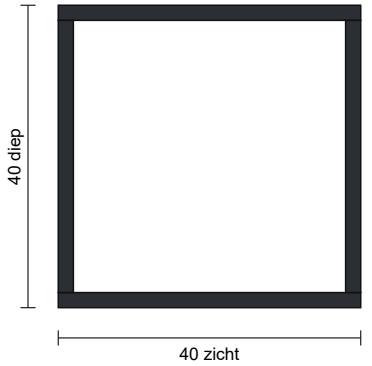

koker 40x40x2

1:1 · 40 x 40 · wand 2

Bewerking en verbindingen


Bewerking: recht · verstek 45°
V1: 2 x verstek 45° met pos 2 (Kozijn: bovenregel)
T1: 1 x t-verbinding (stomp) met pos 4 (Kozijn: onderregel zijlicht)
T2: 2 x t-verbinding (stomp) met pos 9 (Roede zijlicht horizontaal: kern)

Titel: **Pos 1: Kozijn: stijl**			
Deur: Zijlicht met paneel · opening 1450 x 2400		Tekeningnummer: **TD-50-01**	
Maten en toleranties: mm · ISO 2768-m · eerste hoek	Opgesteld: Ian · laswerken	Uitgifte: 2026-11-10	Blad: 1 / 25


2 1 x Kozijn: bovenregel

S235, koker 40x40x2 · L = 1440 · zagen 45°/45° · 3,33 kg/st


Aanzicht (1:10)

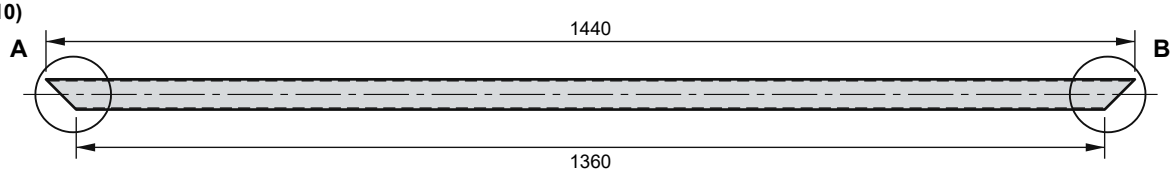

Waar het stuk zit

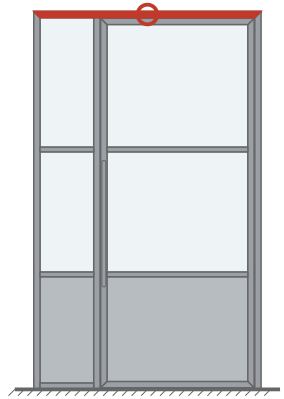


Detail A (1:1): linker uiteinde

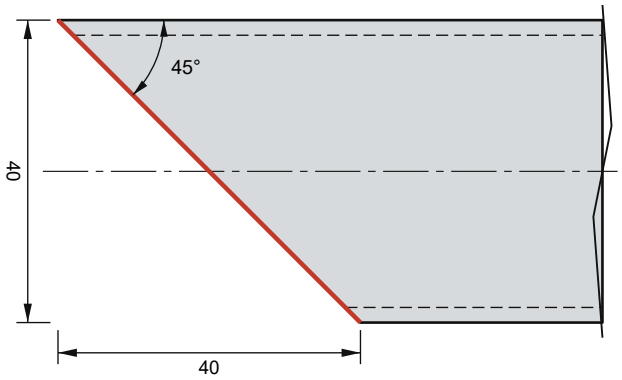


Verstek 45°: lange kant is 40 langer dan de korte

Detail B (1:1): rechter uiteinde

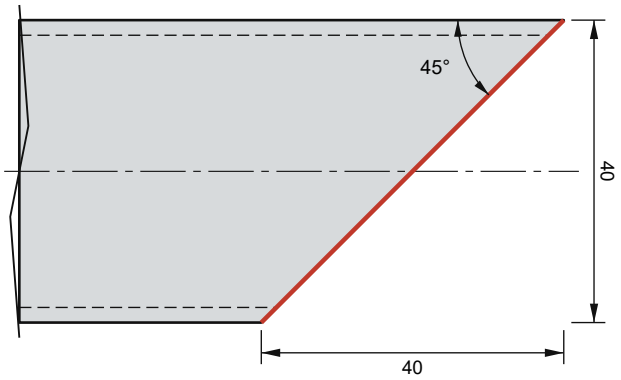

Verstek 45°: lange kant is 40 langer dan de korte

Doorsnede van het profiel

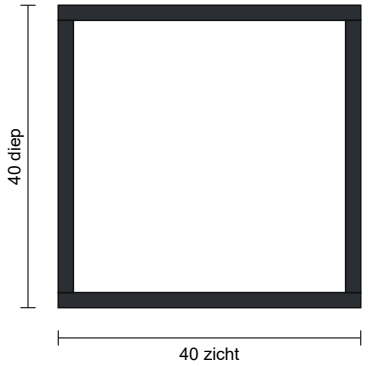

koker 40x40x2

1:1 · 40 x 40 · wand 2

Bewerking en verbindingen

Bewerking: verstek 45° · verstek 45°

V1: 2 x verstek 45° met pos 1 (Kozijn: stijl)

T3: 1 x t-verbinding (stomp) met pos 3 (Kozijn: tussenstijl)

Titel: **Pos 2: Kozijn: bovenregel**			
Deur: Zijlicht met paneel · opening 1450 x 2400		Tekeningnummer: **TD-50-02**	
Maten en toleranties: mm · ISO 2768-m · eerste hoek	Opgesteld: Ian · laswerken	Uitgifte: 2026-11-10	Blad: 2 / 25


3 1 x Kozijn: tussenstijl

S235, koker 40x40x2 · L = 2355 · zagen 90°/90° · 5,44 kg/st


Aanzicht (1:20)



Waar het stuk zit

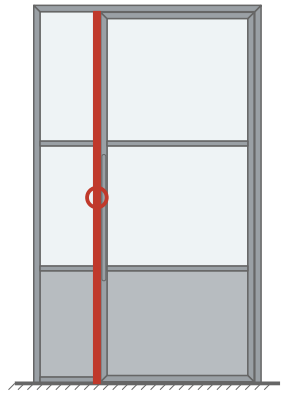


Detail A (1:1): linker uiteinde

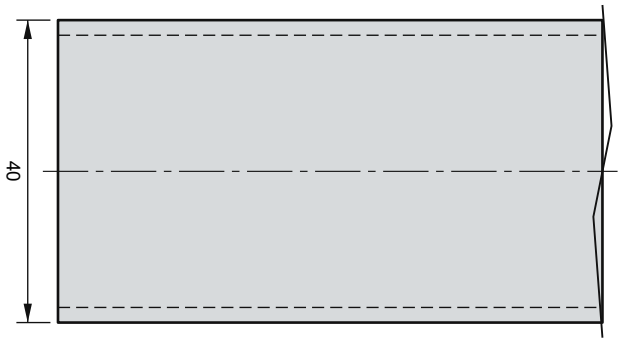


Recht afzagen (90°)

Detail B (1:1): rechter uiteinde

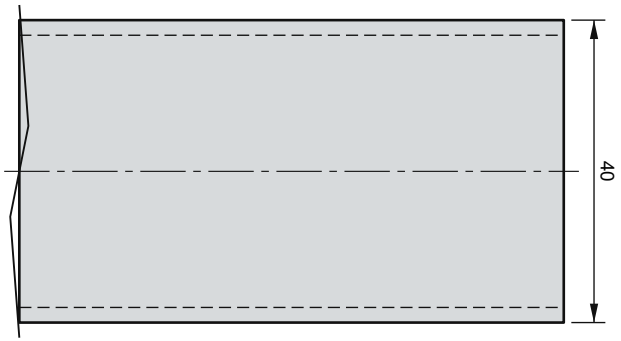

Recht afzagen (90°)

Doorsnede van het profiel

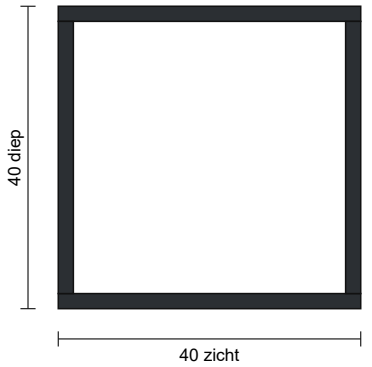

koker 40x40x2

1:1 · 40 x 40 · wand 2

Bewerking en verbindingen

Bewerking: recht · recht

T3: 1 x t-verbinding (stomp) met pos 2 (Kozijn: bovenregel)

T4: 1 x t-verbinding (stomp) met pos 4 (Kozijn: onderregel zijlicht)


T5: 2 x t-verbinding (stomp) met pos 9 (Roede zijlicht horizontaal: kern)

Titel: **Pos 3: Kozijn: tussenstijl**			
Deur: Zijlicht met paneel · opening 1450 x 2400		Tekeningnummer: **TD-50-03**	
Maten en toleranties: mm · ISO 2768-m · eerste hoek	Opgesteld: Ian · laswerken	Uitgifte: 2026-11-10	Blad: 3 / 25


4 1 x Kozijn: onderregel zijlicht

S235, koker 40x40x2 · L = 340 · zagen 90°/90° · 0,79 kg/st


Aanzicht (1:5)

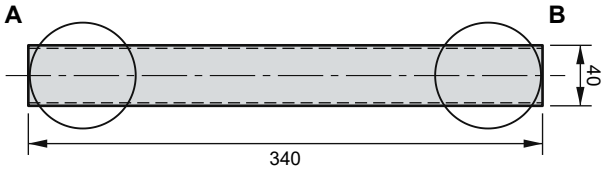

Waar het stuk zit

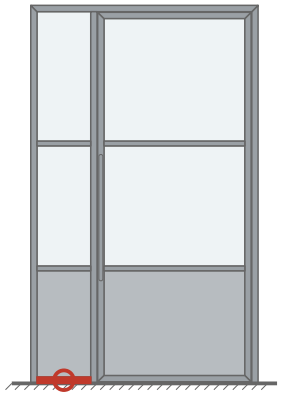


Detail A (1:1): linker uiteinde

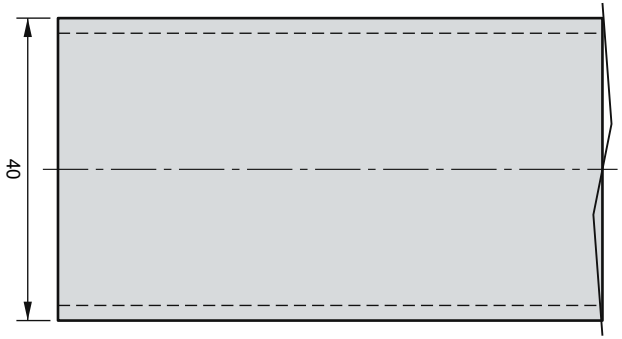


Recht afzagen (90°)

Detail B (1:1): rechter uiteinde

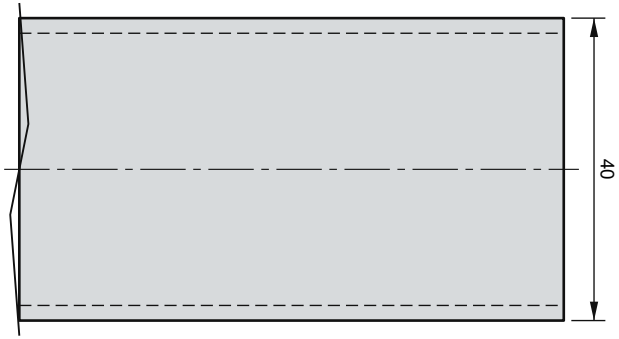

Recht afzagen (90°)

Doorsnede van het profiel

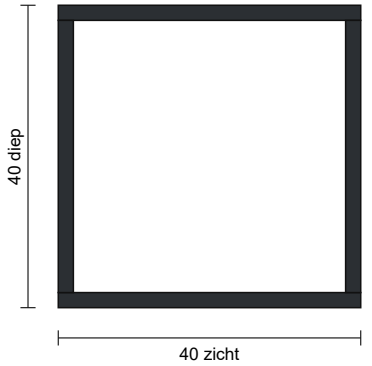

koker 40x40x2

1:1 · 40 x 40 · wand 2

Bewerking en verbindingen

Bewerking: recht · recht

T1: 1 x t-verbinding (stomp) met pos 1 (Kozijn: stijl)

T4: 1 x t-verbinding (stomp) met pos 3 (Kozijn: tussenstijl)

Titel: **Pos 4: Kozijn: onderregel zijlicht**			
Deur: Zijlicht met paneel · opening 1450 x 2400		Tekeningnummer: **TD-50-04**	
Maten en toleranties: mm · ISO 2768-m · eerste hoek	Opgesteld: Ian · laswerken	Uitgifte: 2026-11-10	Blad: 4 / 25


5 2 x Kader: staander

S235, koker 40x40x2 · L = 2341 · zagen 45°/45° · 5,41 kg/st


Aanzicht (1:20)



Waar het stuk zit

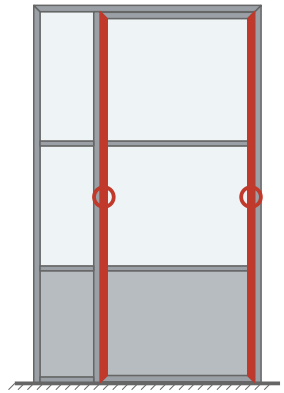


Detail A (1:1): linker uiteinde

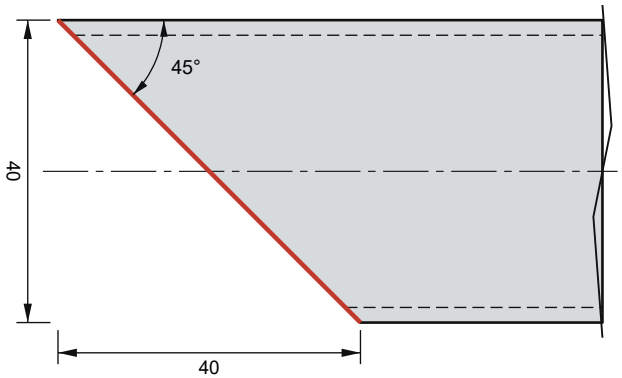


Verstek 45°: lange kant is 40 langer dan de korte

Detail B (1:1): rechter uiteinde

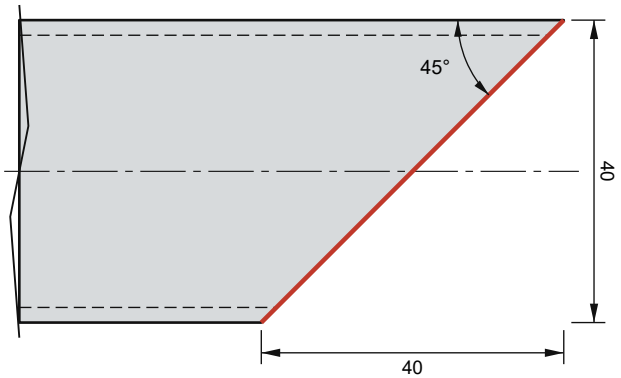

Verstek 45°: lange kant is 40 langer dan de korte

Doorsnede van het profiel

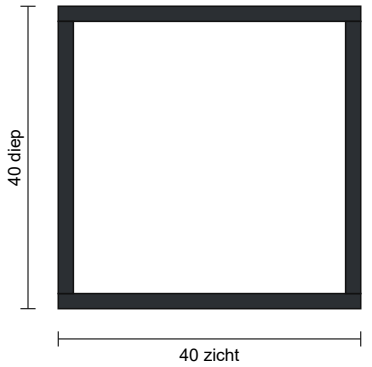

koker 40x40x2

1:1 · 40 x 40 · wand 2

Bewerking en verbindingen


Bewerking: verstek 45° · verstek 45°
V2: 4 x verstek 45° met pos 6 (Kader: regel)
T6: 4 x t-verbinding (stomp) met pos 7 (Roede horizontaal: kern)

Titel: **Pos 5: Kader: staander**			
Deur: Zijlicht met paneel · opening 1450 x 2400		Tekeningnummer: **TD-50-05**	
Maten en toleranties: mm · ISO 2768-m · eerste hoek	Opgesteld: Ian · laswerken	Uitgifte: 2026-11-10	Blad: 5 / 25


6 2 x Kader: regel

S235, koker 40x40x2 · L = 972 · zagen 45°/45° · 2,25 kg/st


Aanzicht (1:10)

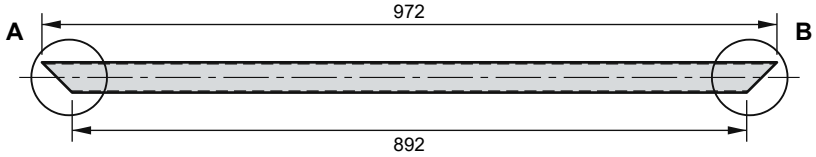

Waar het stuk zit

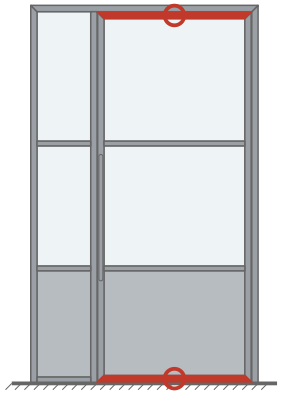


Detail A (1:1): linker uiteinde

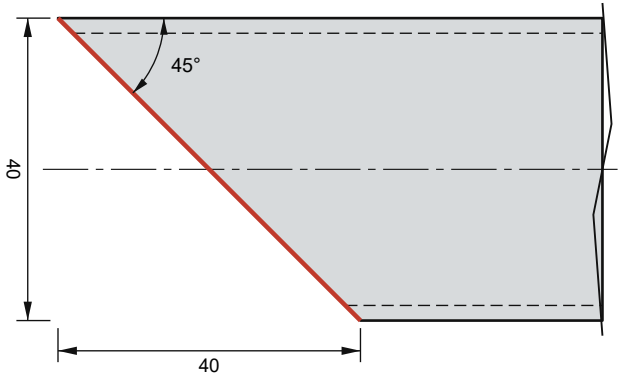


Verstek 45°: lange kant is 40 langer dan de korte

Detail B (1:1): rechter uiteinde

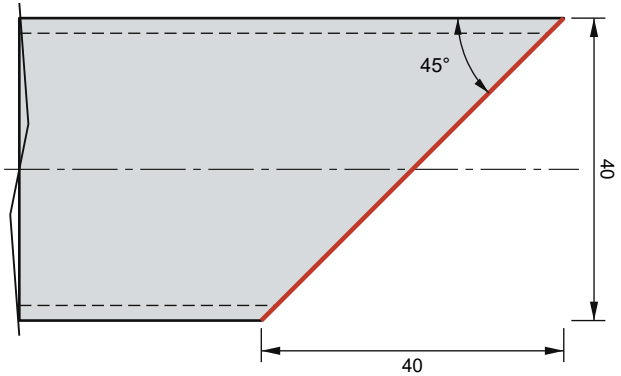

Verstek 45°: lange kant is 40 langer dan de korte

Doorsnede van het profiel

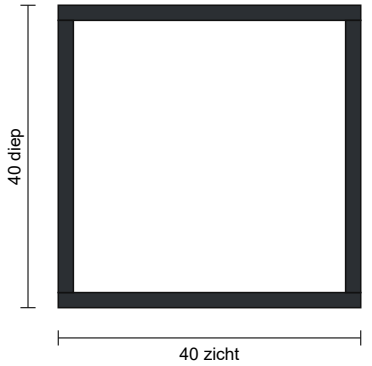

koker 40x40x2

1:1 · 40 x 40 · wand 2

Bewerking en verbindingen

Bewerking: verstek 45° · verstek 45°


V2: 4 x verstek 45° met pos 5 (Kader: staander)

Titel: **Pos 6: Kader: regel**			
Deur: Zijlicht met paneel · opening 1450 x 2400		Tekeningnummer: **TD-50-06**	
Maten en toleranties: mm · ISO 2768-m · eerste hoek	Opgesteld: Ian · laswerken	Uitgifte: 2026-11-10	Blad: 6 / 25


7 2 x Roede horizontaal: kern

S235, platstaal 20x10 · L = 892 · zagen 90°/90° · 1,4 kg/st


Waar het stuk zit

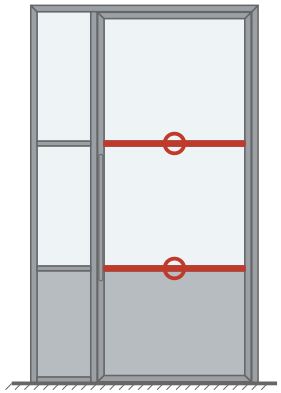

Aanzicht (1:5)

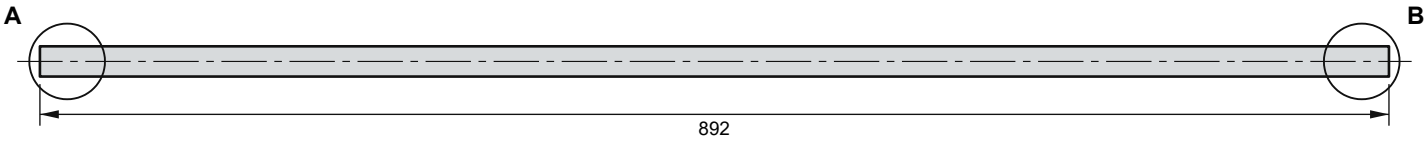


Detail A (2:1): linker uiteinde

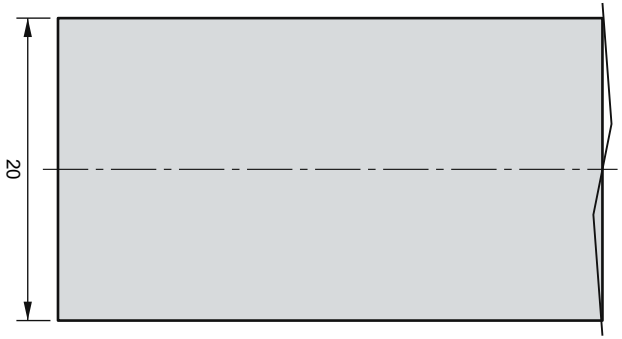


Recht afzagen (90°)

Detail B (2:1): rechter uiteinde

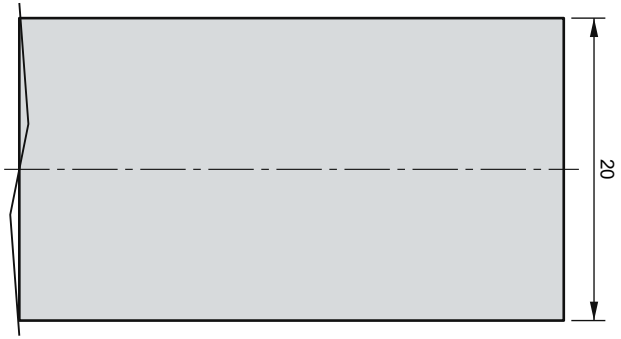

Recht afzagen (90°)

Doorsnede van het profiel

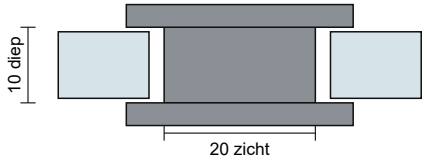

platstaal 20x10

1:1 · 20 x 10

Bewerking en verbindingen

Bewerking: recht · recht; M4 om de 250 aan de achterkant


T6: 4 x t-verbinding (stomp) met pos 5 (Kader: staander)

Titel: **Pos 7: Roede horizontaal: kern**			
Deur: Zijlicht met paneel · opening 1450 x 2400		Tekeningnummer: **TD-50-07**	
Maten en toleranties: mm · ISO 2768-m · eerste hoek	Opgesteld: Ian · laswerken	Uitgifte: 2026-11-10	Blad: 7 / 25


8 4 x Roede horizontaal: lat voor en achter

S235, platstaal 30x3 · L = 892 · zagen 90°/90° · 0,63 kg/st


Aanzicht (1:5)

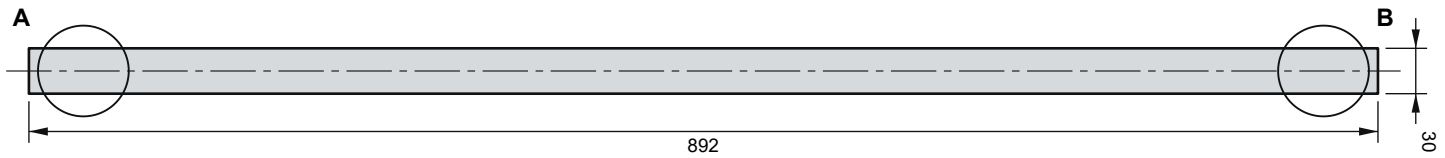

Waar het stuk zit

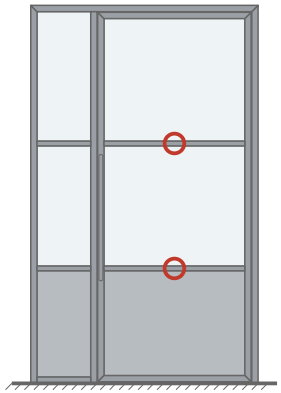


Detail A (1:1): linker uiteinde

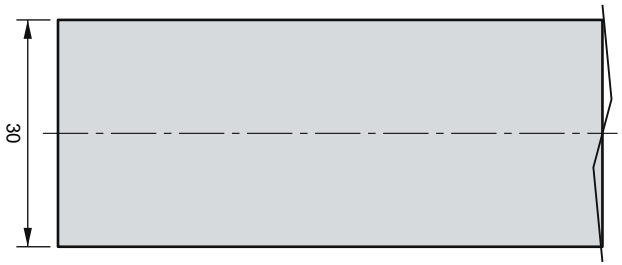


Recht afzagen (90°)

Detail B (1:1): rechter uiteinde

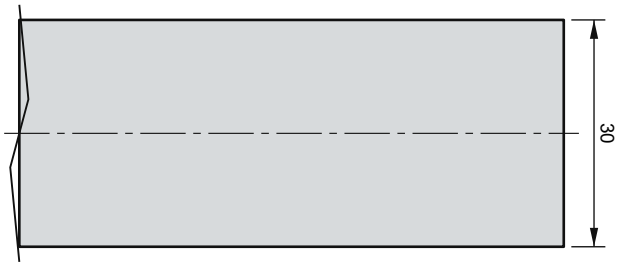

Recht afzagen (90°)

Doorsnede (arcering = materiaal)

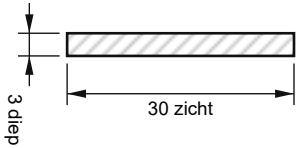

platstaal 30x3 (1:1)

boven = de kant met de greep

Bewerking en verbindingen

Bewerking: recht · recht; voor gelast, achter geschroefd


Hechten om de 150 en lassen (voor) of M4 verzonken om de 250 (achter): zie de werkwijze

Titel: **Pos 8: Roede horizontaal: lat voor en achter**			
Deur: Zijlicht met paneel · opening 1450 x 2400		Tekeningnummer: **TD-50-08**	
Maten en toleranties: mm · ISO 2768-m · eerste hoek	Opgesteld: Ian · laswerken	Uitgifte: 2026-11-10	Blad: 8 / 25


9 2 x Roede zijlicht horizontaal: kern

S235, platstaal 20x10 · L = 340 · zagen 90°/90° · 0,53 kg/st


Waar het stuk zit

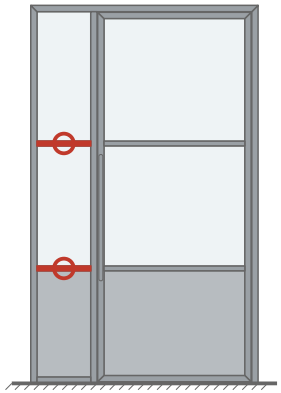

Aanzicht (1:2)

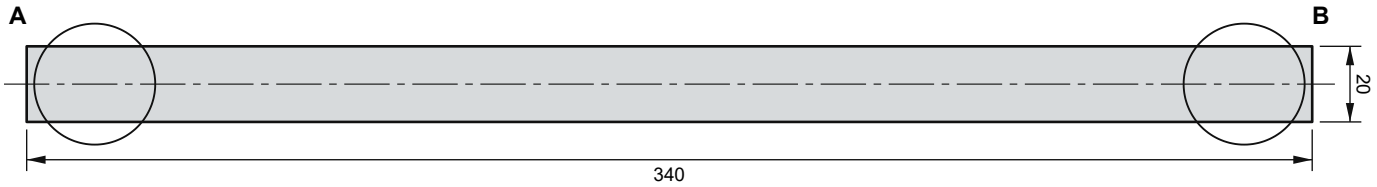


Detail A (2:1): linker uiteinde

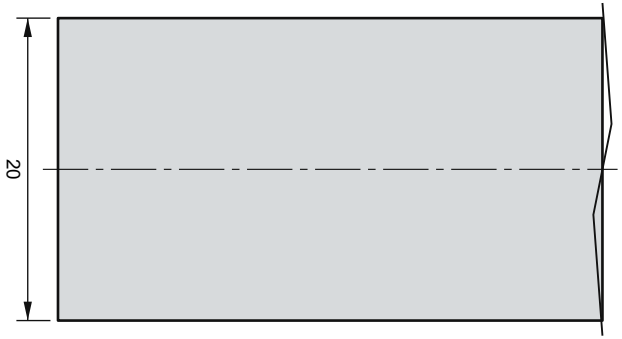


Recht afzagen (90°)

Detail B (2:1): rechter uiteinde

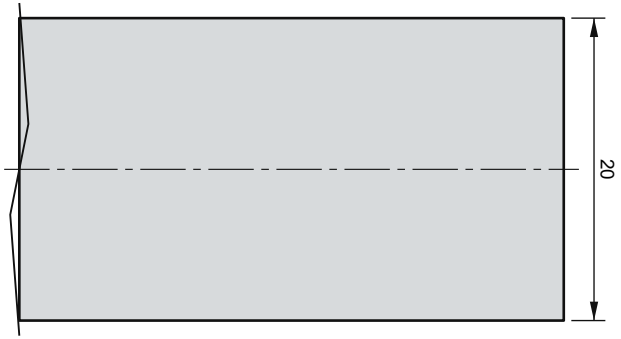

Recht afzagen (90°)

Doorsnede van het profiel

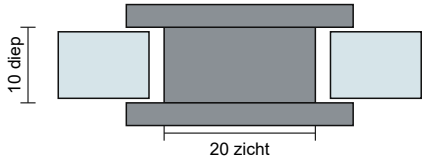

platstaal 20x10

1:1 · 20 x 10

Bewerking en verbindingen


Bewerking: recht · recht; M4 om de 250 aan de achterkant
T2: 2 x t-verbinding (stomp) met pos 1 (Kozijn: stijl)
T5: 2 x t-verbinding (stomp) met pos 3 (Kozijn: tussenstijl)

Titel: **Pos 9: Roede zijlicht horizontaal: kern**			
Deur: Zijlicht met paneel · opening 1450 x 2400		Tekeningnummer: **TD-50-09**	
Maten en toleranties: mm · ISO 2768-m · eerste hoek	Opgesteld: Ian · laswerken	Uitgifte: 2026-11-10	Blad: 9 / 25


10 4 x Roede zijlicht horizontaal: lat voor en achter

S235, platstaal 30x3 · L = 340 · zagen 90°/90° · 0,24 kg/st


Waar het stuk zit

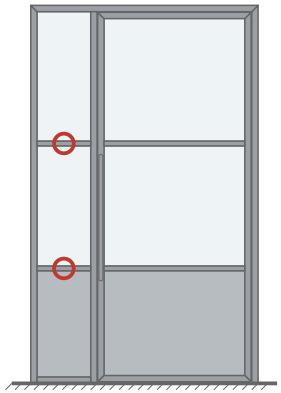

Aanzicht (1:2)

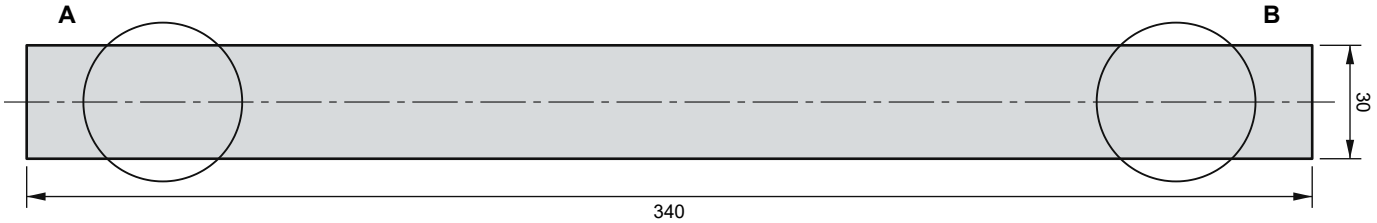


Detail A (1:1): linker uiteinde

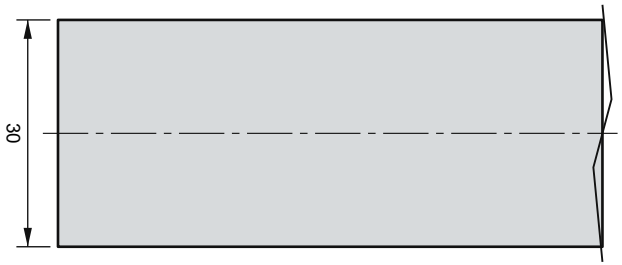


Recht afzagen (90°)

Detail B (1:1): rechter uiteinde

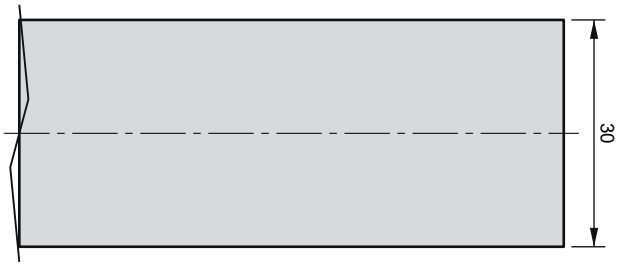

Recht afzagen (90°)

Doorsnede (arcering = materiaal)

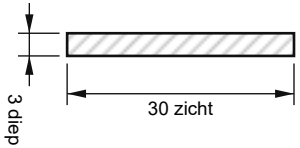

platstaal 30x3 (1:1)

boven = de kant met de greep

Bewerking en verbindingen

Bewerking: recht · recht; voor gelast, achter geschroefd


Hechten om de 150 en lassen (voor) of M4 verzonken om de 250 (achter): zie de werkwijze

Titel: **Pos 10: Roede zijlicht horizontaal: lat voor en achter**			
Deur: Zijlicht met paneel · opening 1450 x 2400		Tekeningnummer: **TD-50-10**	
Maten en toleranties: mm · ISO 2768-m · eerste hoek	Opgesteld: Ian · laswerken	Uitgifte: 2026-11-10	Blad: 10 / 25


11 8 x Glaslat

S235, platstaal 15x4 · L = 761 · 0,36 kg/st


Aanzicht (1:5)

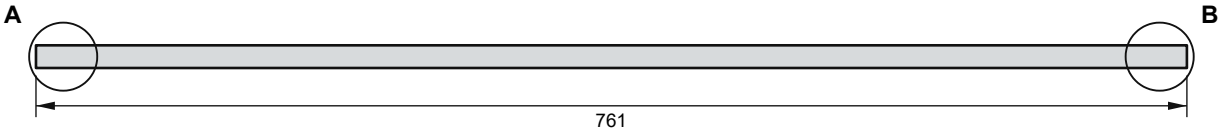

Waar het stuk zit

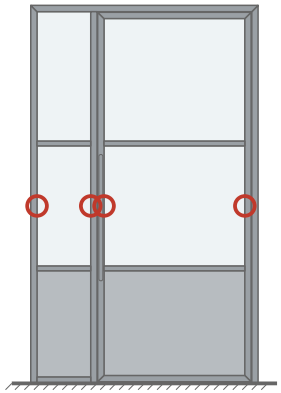


Detail A (2:1): linker uiteinde

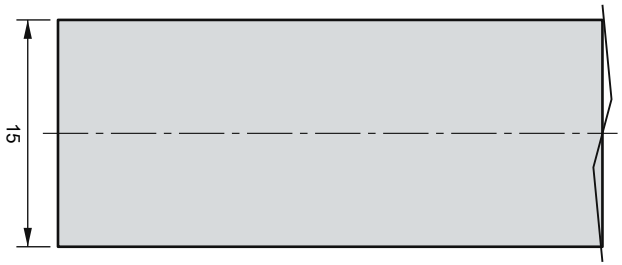

Recht afzagen (90°)

Detail B (2:1): rechter uiteinde

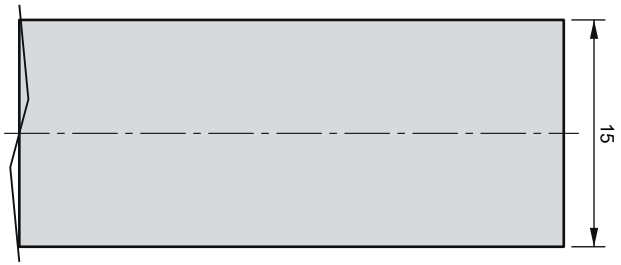

Recht afzagen (90°)

Doorsnede van het profiel



platstaal 15x4

3:1 · 15 x 4

Bewerking en verbindingen

Bewerking: recht; voor gelast, achter geschroefd (M4 verzonken om de 250)

Hechten om de 150 en lassen (voor) of M4 verzonken om de 250 (achter): zie de werkwijze

Titel: **Pos 11: Glaslat**			
Deur: Zijlicht met paneel · opening 1450 x 2400		Tekeningnummer: **TD-50-11**	
Maten en toleranties: mm · ISO 2768-m · eerste hoek	Opgesteld: Ian · laswerken	Uitgifte: 2026-11-10	Blad: 11 / 25


12 4 x Glaslat

S235, platstaal 15x4 · L = 776 · 0,36 kg/st


Aanzicht (1:5)



Waar het stuk zit

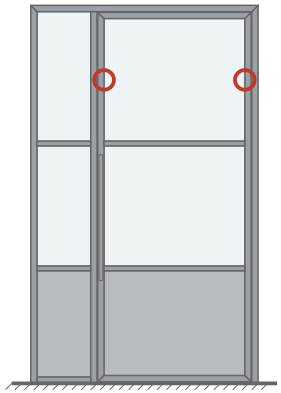


Detail A (2:1): linker uiteinde

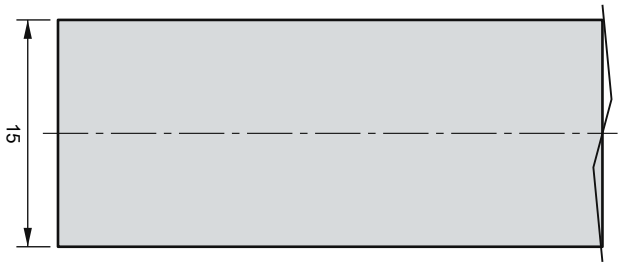

Recht afzagen (90°)

Detail B (2:1): rechter uiteinde

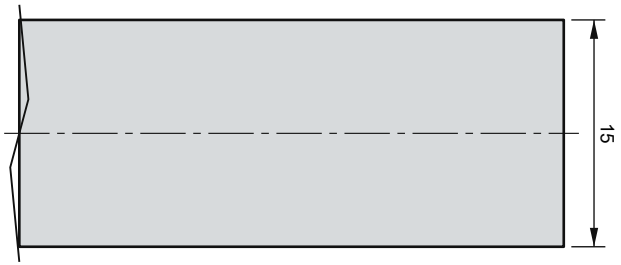

Recht afzagen (90°)

Doorsnede van het profiel



platstaal 15x4

3:1 · 15 x 4

Bewerking en verbindingen

Bewerking: recht; voor gelast, achter geschroefd (M4 verzonken om de 250)


Hechten om de 150 en lassen (voor) of M4 verzonken om de 250 (achter): zie de werkwijze

Titel: **Pos 12: Glaslat**			
Deur: Zijlicht met paneel · opening 1450 x 2400		Tekeningnummer: **TD-50-12**	
Maten en toleranties: mm · ISO 2768-m · eerste hoek	Opgesteld: Ian · laswerken	Uitgifte: 2026-11-10	Blad: 12 / 25


13 2 x Glaslat

S235, platstaal 15x4 · L = 892 · 0,42 kg/st


Aanzicht (1:5)

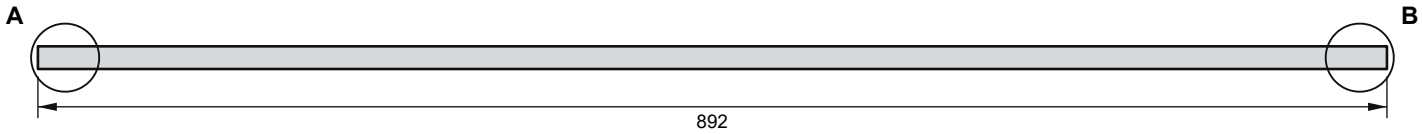

Waar het stuk zit

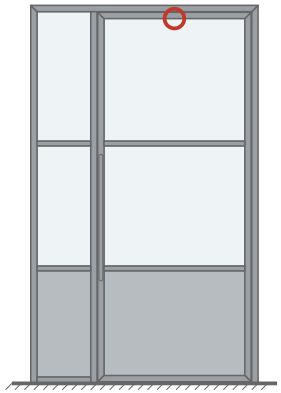


Detail A (2:1): linker uiteinde

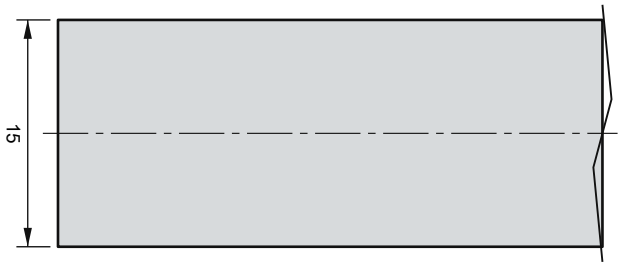

Recht afzagen (90°)

Detail B (2:1): rechter uiteinde

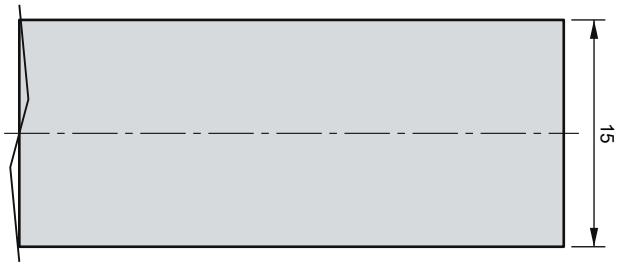

Recht afzagen (90°)

Doorsnede van het profiel



platstaal 15x4

3:1 · 15 x 4

Bewerking en verbindingen

Bewerking: recht; voor gelast, achter geschroefd (M4 verzonken om de 250)


Hechten om de 150 en lassen (voor) of M4 verzonken om de 250 (achter): zie de werkwijze

Titel: **Pos 13: Glaslat**			
Deur: Zijlicht met paneel · opening 1450 x 2400		Tekeningnummer: **TD-50-13**	
Maten en toleranties: mm · ISO 2768-m · eerste hoek	Opgesteld: Ian · laswerken	Uitgifte: 2026-11-10	Blad: 13 / 25


14 4 x Glaslat

S235, platstaal 15x4 · L = 820 · 0,39 kg/st


Aanzicht (1:5)

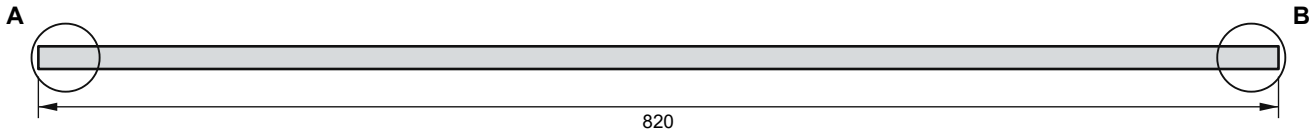

Waar het stuk zit

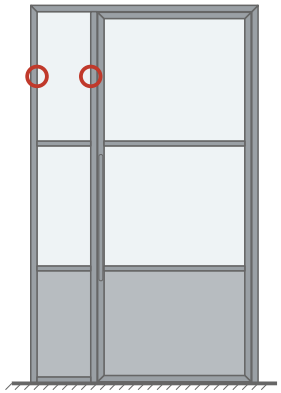


Detail A (2:1): linker uiteinde

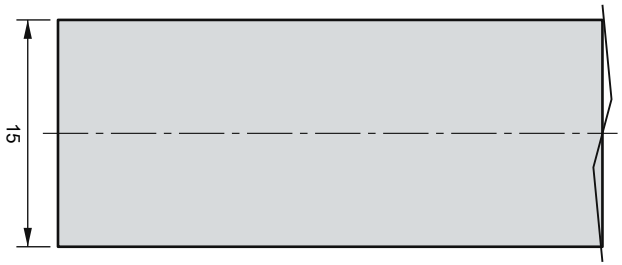

Recht afzagen (90°)

Detail B (2:1): rechter uiteinde

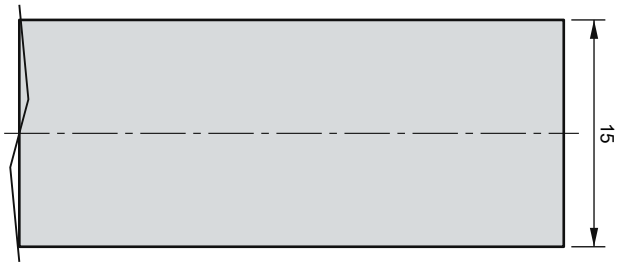

Recht afzagen (90°)

Doorsnede van het profiel



platstaal 15x4

3:1 · 15 x 4

Bewerking en verbindingen


Bewerking: recht; voor gelast, achter geschroefd (M4 verzonken om de 250)
Hechten om de 150 en lassen (voor) of M4 verzonken om de 250 (achter): zie de werkwijze

Titel: **Pos 14: Glaslat**			
Deur: Zijlicht met paneel · opening 1450 x 2400		Tekeningnummer: **TD-50-14**	
Maten en toleranties: mm · ISO 2768-m · eerste hoek	Opgesteld: Ian · laswerken	Uitgifte: 2026-11-10	Blad: 14 / 25


15 2 x Glaslat

S235, platstaal 15x4 · L = 340 · 0,16 kg/st


Aanzicht (1:2)

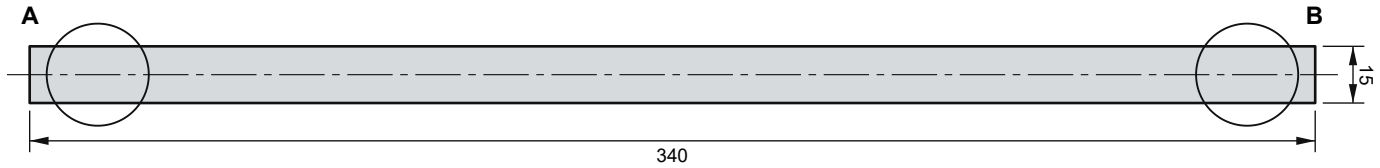

Waar het stuk zit

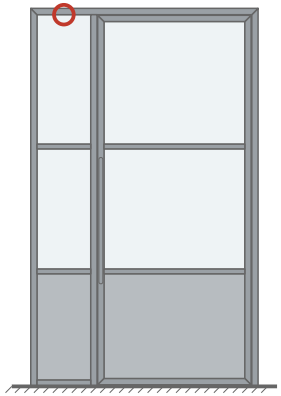


Detail A (2:1): linker uiteinde

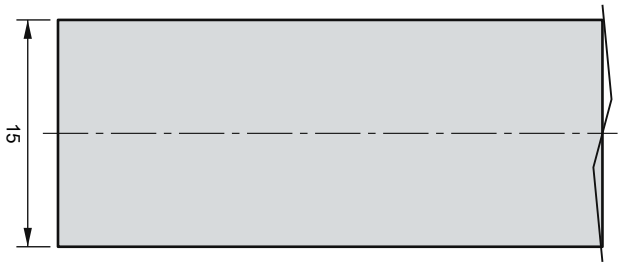

Recht afzagen (90°)

Detail B (2:1): rechter uiteinde

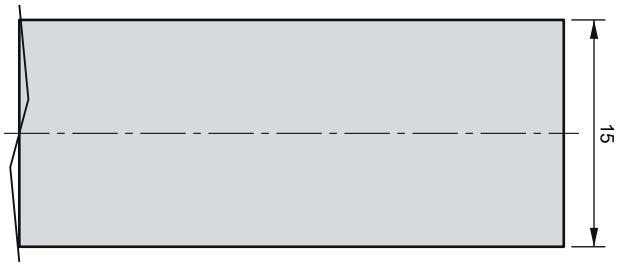

Recht afzagen (90°)

Doorsnede van het profiel



platstaal 15x4

3:1 · 15 x 4

Bewerking en verbindingen

Bewerking: recht; voor gelast, achter geschroefd (M4 verzonken om de 250)


Hechten om de 150 en lassen (voor) of M4 verzonken om de 250 (achter): zie de werkwijze

Titel: **Pos 15: Glaslat**			
Deur: Zijlicht met paneel · opening 1450 x 2400		Tekeningnummer: **TD-50-15**	
Maten en toleranties: mm · ISO 2768-m · eerste hoek	Opgesteld: Ian · laswerken	Uitgifte: 2026-11-10	Blad: 15 / 25


16 2 x Greep (voor en achter)

S235, rond Ø25 · L = 800 · 3,08 kg/st


Aanzicht (1:5)

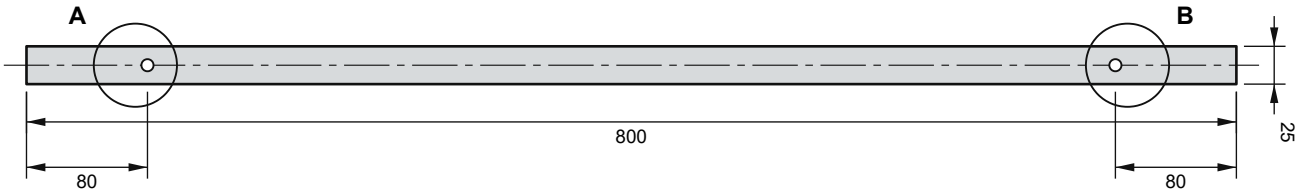

Waar het stuk zit

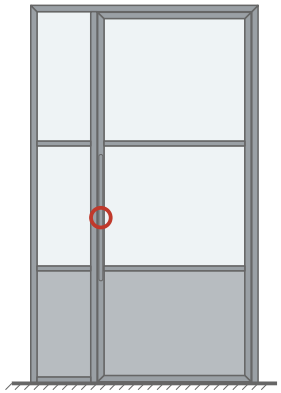


Detail A (1:2): linker uiteinde

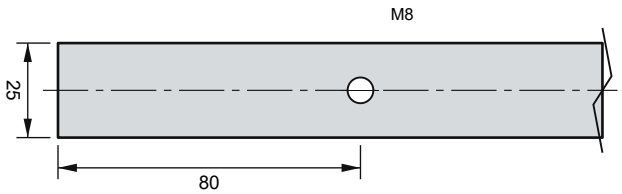


Recht afzagen (90°)

Detail B (1:2): rechter uiteinde

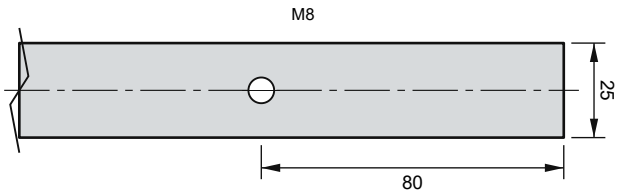

Recht afzagen (90°)

Doorsnede (arcering = materiaal)

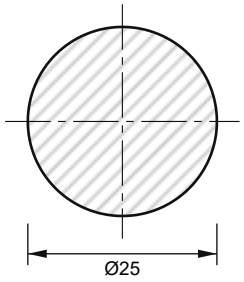

rond Ø25 (1:1)

Bewerking en verbindingen

Bewerking: uiteinden rond slijpen; 2 x M8 op 80 van de uiteinden


Titel: **Pos 16: Greep (voor en achter)**			
Deur: Zijlicht met paneel · opening 1450 x 2400		Tekeningnummer: **TD-50-16**	
Maten en toleranties: mm · ISO 2768-m · eerste hoek	Opgesteld: Ian · laswerken	Uitgifte: 2026-11-10	Blad: 16 / 25

17


1 x Taatsplaat onder

S235, plaat 8 mm · 36 x 220 · 0,5 kg/st

Aanzicht (1:2)

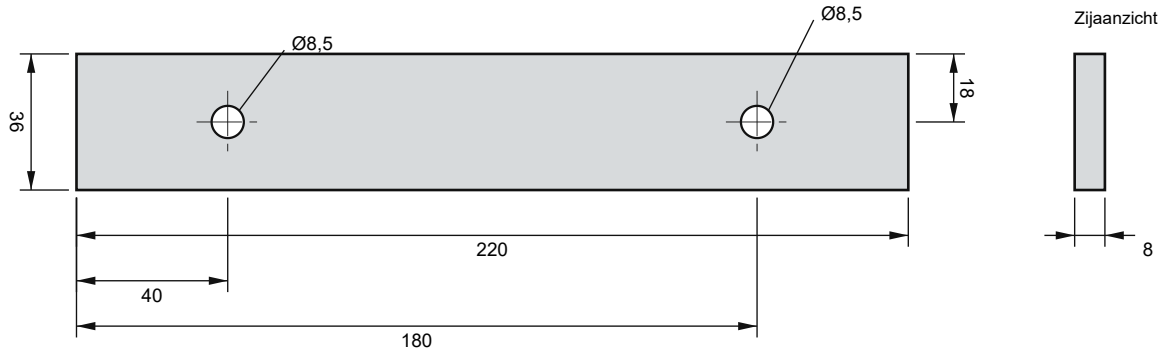

Waar het stuk zit

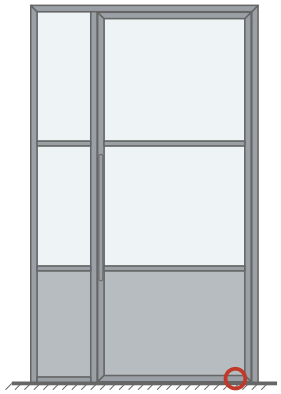

Plaat

S235, plaat 8 mm

36 x 220 x 8 mm

Lasersnijden op de DXF; braam eraf

Bewerking en verbindingen


Bewerking: 2 x Ø8,5 voor het scharnier; in de onderregel gelast

Titel: **Pos 17: Taatsplaat onder**			
Deur: Zijlicht met paneel · opening 1450 x 2400		Tekeningnummer: **TD-50-17**	
Maten en toleranties: mm · ISO 2768-m · eerste hoek	Opgesteld: Ian · laswerken	Uitgifte: 2026-11-10	Blad: 17 / 25

18 1 x Taatsplaat boven

S235, plaat 8 mm · 36 x 140 · 0,32 kg/st


Aanzicht (1:1)

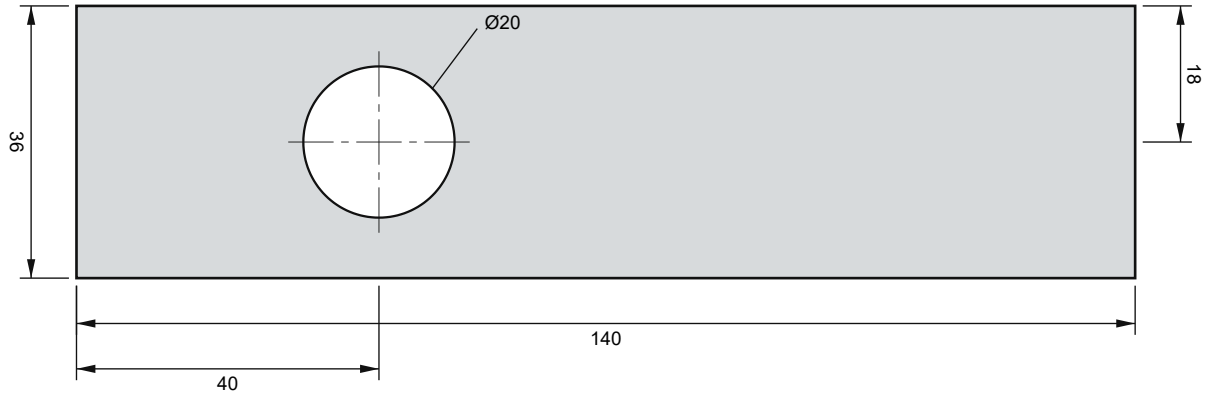

Zijaanzicht



Waar het stuk zit

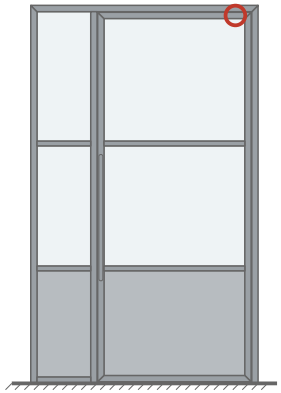

Plaat

S235, plaat 8 mm

36 x 140 x 8 mm

Lasersnijden op de DXF; braam eraf

Bewerking en verbindingen


Bewerking: Ø20 voor de bovenpen; in de bovenregel gelast

Titel: **Pos 18: Taatsplaat boven**			
Deur: Zijlicht met paneel · opening 1450 x 2400		Tekeningnummer: **TD-50-18**	
Maten en toleranties: mm · ISO 2768-m · eerste hoek	Opgesteld: Ian · laswerken	Uitgifte: 2026-11-10	Blad: 18 / 25


19 2 x Greephouder

S235, plaat 10 mm · 25 x 40 · 0,08 kg/st


Aanzicht (2:1)

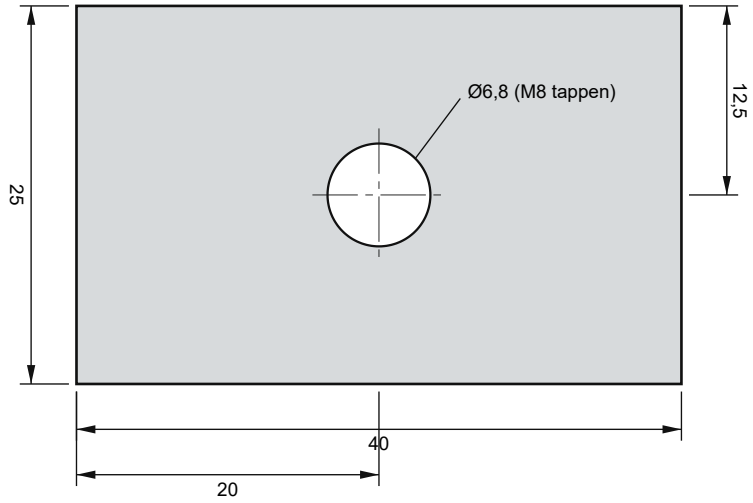

Zijaanzicht

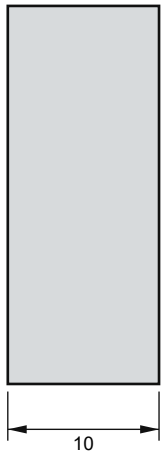

Waar het stuk zit

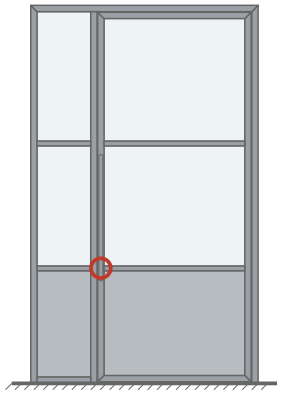

Plaat

S235, plaat 10 mm

25 x 40 x 10 mm

Lasersnijden op de DXF; braam eraf

Bewerking en verbindingen


Bewerking: M8 tappen (boor Ø6,8); op de staander gelast

Titel: **Pos 19: Greephouder**			
Deur: Zijlicht met paneel · opening 1450 x 2400		Tekeningnummer: **TD-50-19**	
Maten en toleranties: mm · ISO 2768-m · eerste hoek	Opgesteld: Ian · laswerken	Uitgifte: 2026-11-10	Blad: 19 / 25

20 1 x Paneel

S235, plaat 3 mm · 890 x 661 · 13,85 kg/st


Aanzicht (1:10)

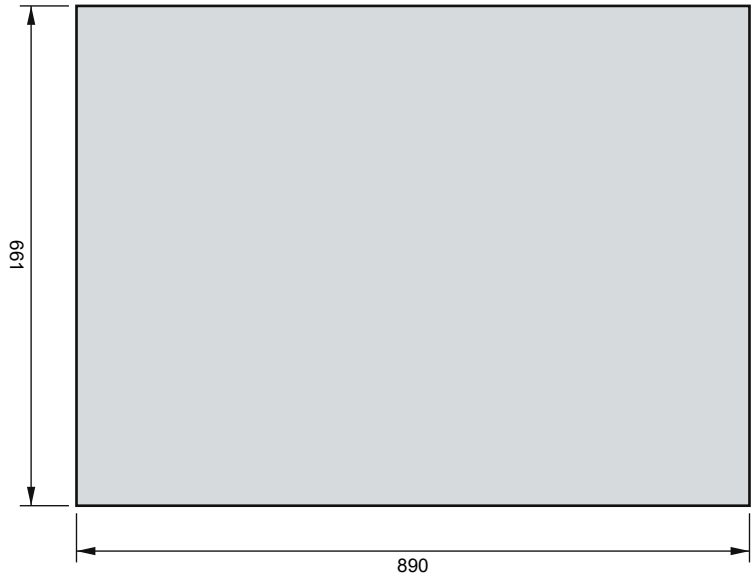

Zijaanzicht



Waar het stuk zit

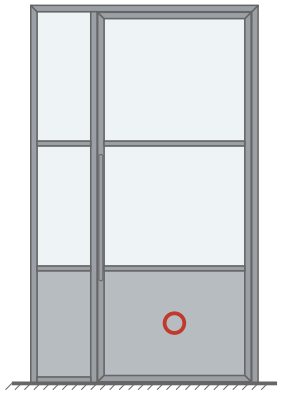

Plaat

S235, plaat 3 mm

661 x 890 x 3 mm

Lasersnijden op de DXF; braam eraf

Bewerking en verbindingen


Bewerking: 1 mm kleiner dan het vak; in het midden van de diepte ingelast

Titel: **Pos 20: Paneel**			
Deur: Zijlicht met paneel · opening 1450 x 2400		Tekeningnummer: **TD-50-20**	
Maten en toleranties: mm · ISO 2768-m · eerste hoek	Opgesteld: Ian · laswerken	Uitgifte: 2026-11-10	Blad: 20 / 25


21 1 x Paneel

S235, plaat 3 mm · 338 x 671 · 5,34 kg/st

Aanzicht (1:10)

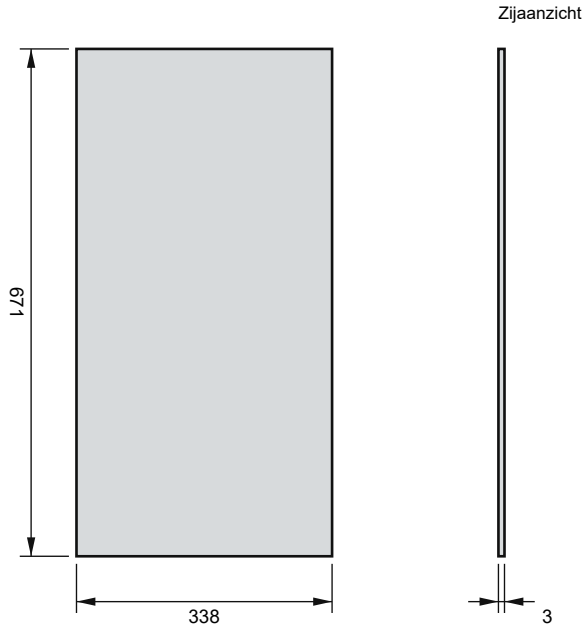

Waar het stuk zit

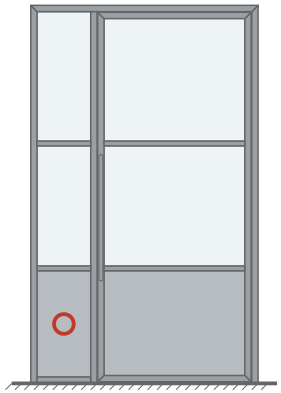

Plaat

S235, plaat 3 mm

671 x 338 x 3 mm

Lasersnijden op de DXF; braam eraf

Bewerking en verbindingen


Bewerking: 1 mm kleiner dan het vak; in het midden van de diepte ingelast

Titel: **Pos 21: Paneel**			
Deur: Zijlicht met paneel · opening 1450 x 2400		Tekeningnummer: **TD-50-21**	
Maten en toleranties: mm · ISO 2768-m · eerste hoek	Opgesteld: Ian · laswerken	Uitgifte: 2026-11-10	Blad: 21 / 25


22 1 x Ruit

gelaagd 44.2 helder · 900 x 769 · 14,4 kg/st

Aanzicht (1:10): daglicht, de ruit is 4 mm groter rondom

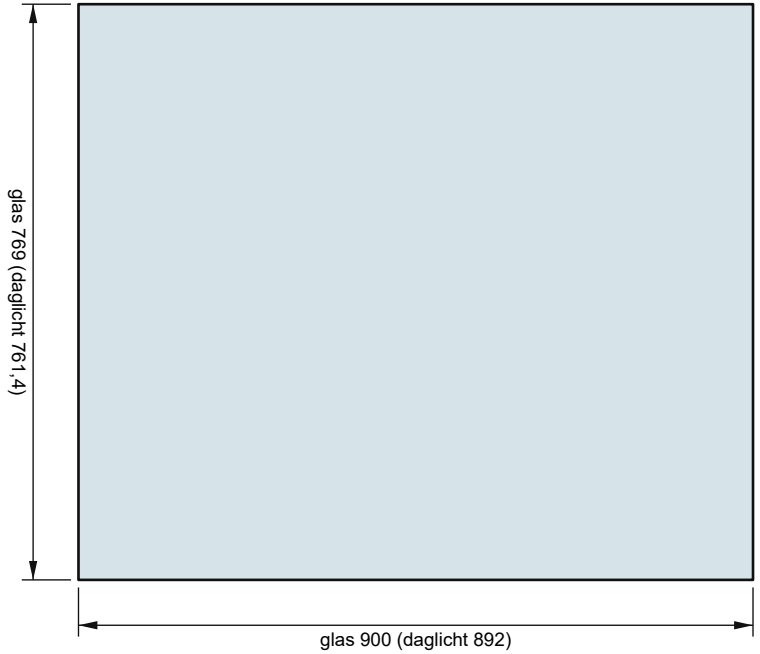

Waar het stuk zit

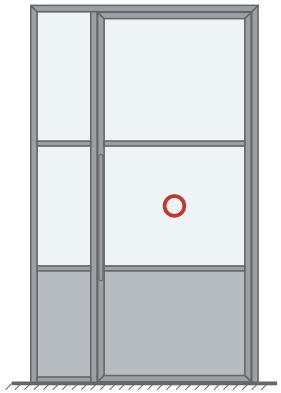

Opbouw (2:1)



gelaagd 44.2 helder

altijd veiligheidsglas (EN 12543 / EN 12150)

Bewerking en verbindingen

Bewerking: veiligheidsglas; glasmaat = daglicht + 4 rondom

Titel: **Pos 22: Ruit**			
Deur: Zijlicht met paneel · opening 1450 x 2400		Tekeningnummer: **TD-50-22**	
Maten en toleranties: mm · ISO 2768-m · eerste hoek	Opgesteld: Ian · laswerken	Uitgifte: 2026-11-10	Blad: 22 / 25


23 1 x Ruit

gelaagd 44.2 helder · 900 x 784 · 14,68 kg/st

Aanzicht (1:10): daglicht, de ruit is 4 mm groter rondom



Waar het stuk zit

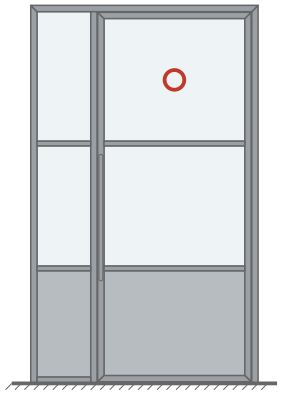

Opbouw (2:1)



gelaagd 44.2 helder

altijd veiligheidsglas (EN 12543 / EN 12150)

Bewerking en verbindingen


Bewerking: veiligheidsglas; glasmaat = daglicht + 4 rondom

Titel: **Pos 23: Ruit**			
Deur: Zijlicht met paneel · opening 1450 x 2400		Tekeningnummer: **TD-50-23**	
Maten en toleranties: mm · ISO 2768-m · eerste hoek	Opgesteld: Ian · laswerken	Uitgifte: 2026-11-10	Blad: 23 / 25


24 1 x Ruit

gelaagd 44.2 helder · 348 x 769 · 5,57 kg/st

Aanzicht (1:10): daglicht, de ruit is 4 mm groter rondom

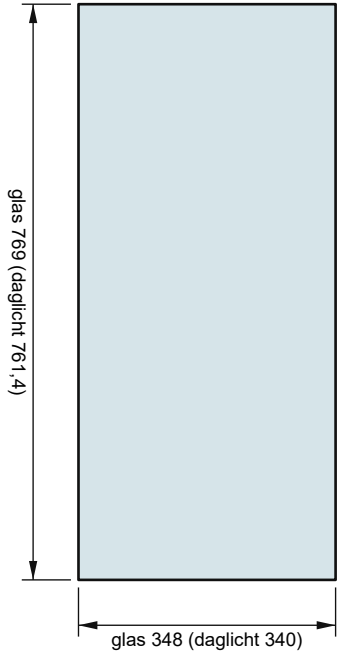

Waar het stuk zit

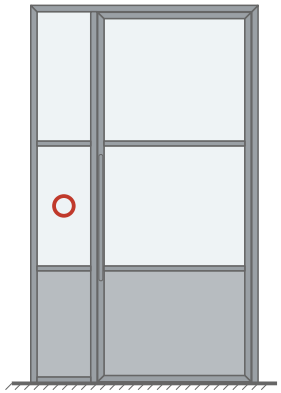

Opbouw (2:1)



gelaagd 44.2 helder

altijd veiligheidsglas (EN 12543 / EN 12150)

Bewerking en verbindingen


Bewerking: veiligheidsglas; glasmaat = daglicht + 4 rondom

Titel: **Pos 24: Ruit**			
Deur: Zijlicht met paneel · opening 1450 x 2400		Tekeningnummer: **TD-50-24**	
Maten en toleranties: mm · ISO 2768-m · eerste hoek	Opgesteld: Ian · laswerken	Uitgifte: 2026-11-10	Blad: 24 / 25


25 1 x Ruit

gelaagd 44.2 helder · 348 x 828 · 5,99 kg/st

Aanzicht (1:10): daglicht, de ruit is 4 mm groter rondom

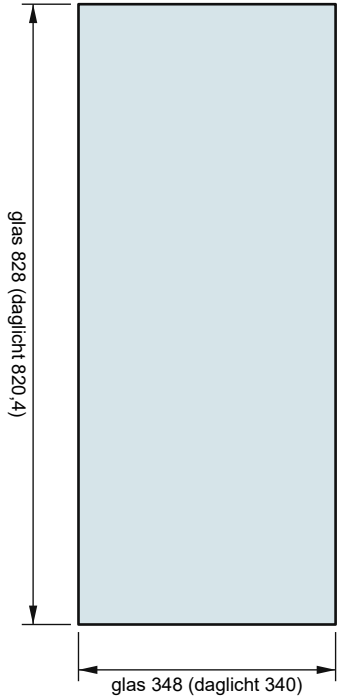

Waar het stuk zit

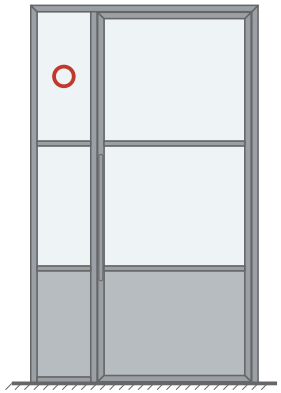

Opbouw (2:1)



gelaagd 44.2 helder

altijd veiligheidsglas (EN 12543 / EN 12150)

Bewerking en verbindingen

Bewerking: veiligheidsglas; glasmaat = daglicht + 4 rondom

Titel: **Pos 25: Ruit**			
Deur: Zijlicht met paneel · opening 1450 x 2400		Tekeningnummer: **TD-50-25**	
Maten en toleranties: mm · ISO 2768-m · eerste hoek	Opgesteld: Ian · laswerken	Uitgifte: 2026-11-10	Blad: 25 / 25