
1


2 x Kozijn: stijl

S235, koker 40x40x2 · L = 2595 · zagen 90°/45° · 5,99 kg/st


Waar het stuk zit

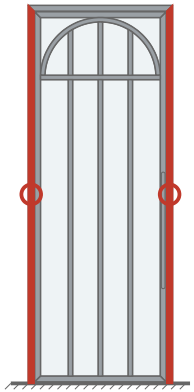

Aanzicht (1:20)

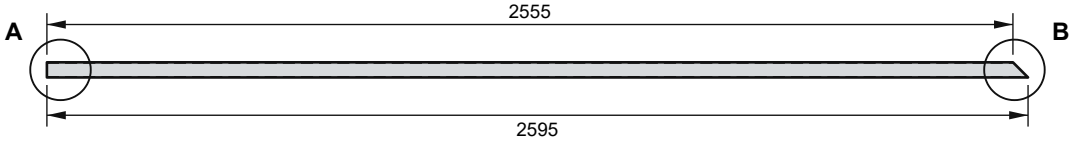


Detail A (1:1): linker uiteinde

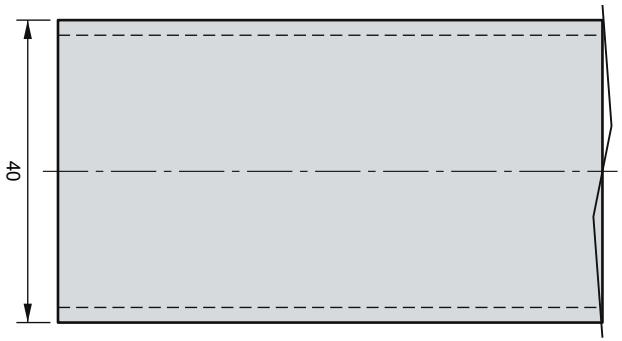


Recht afzagen (90°)

Detail B (1:1): rechter uiteinde

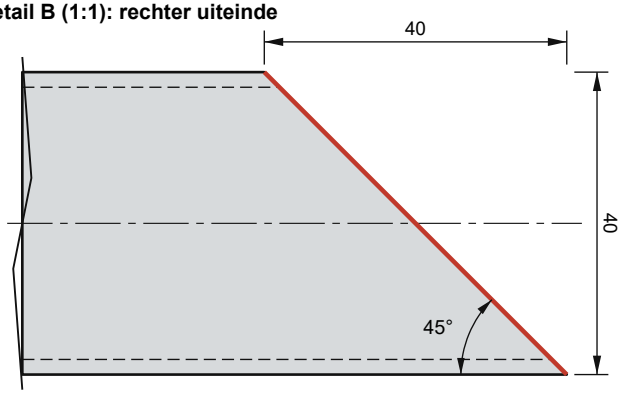

Verstek 45°: lange kant is 40 langer dan de korte

Doorsnede (arcering = materiaal)

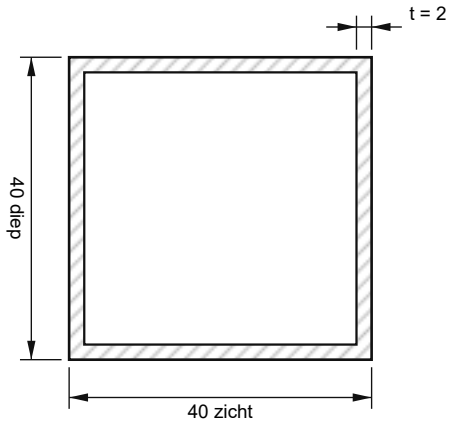

koker 40x40x2 (1:1)

boven = de kant met de greep

Bewerking en verbindingen

Bewerking: recht · verstek 45°


V1: 2 x verstek 45° met pos 2 (Kozijn: bovenregel)

Titel: **Pos 1: Kozijn: stijl**			
Deur: Kathedraal · opening 1000 x 2600		Tekeningnummer: **TD-34-01**	
Maten en toleranties: mm · ISO 2768-m · eerste hoek	Opgesteld: Ian · laswerken	Uitgifte: 2026-11-10	Blad: 1 / 28


2 1 x Kozijn: bovenregel

S235, koker 40x40x2 · L = 990 · zagen 45°/45° · 2,29 kg/st


Aanzicht (1:10)

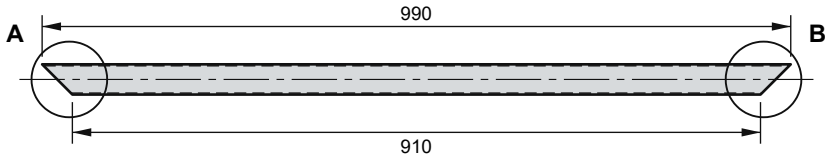

Waar het stuk zit

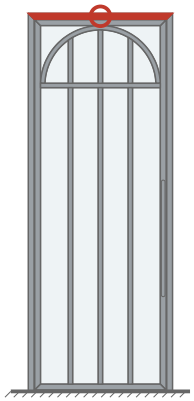


Detail A (1:1): linker uiteinde

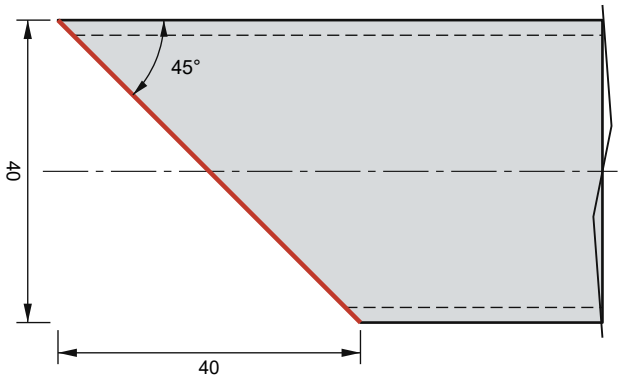


Verstek 45°: lange kant is 40 langer dan de korte

Detail B (1:1): rechter uiteinde

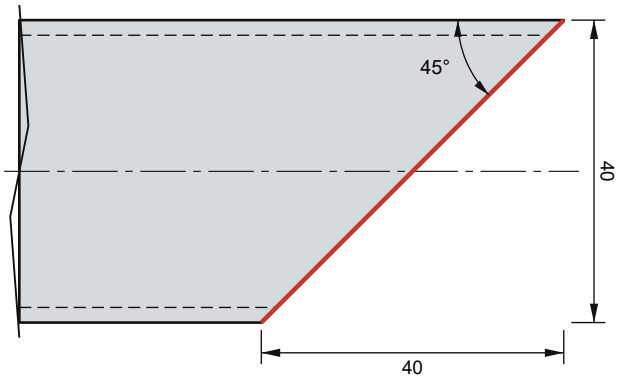

Verstek 45°: lange kant is 40 langer dan de korte

Doorsnede (arcering = materiaal)

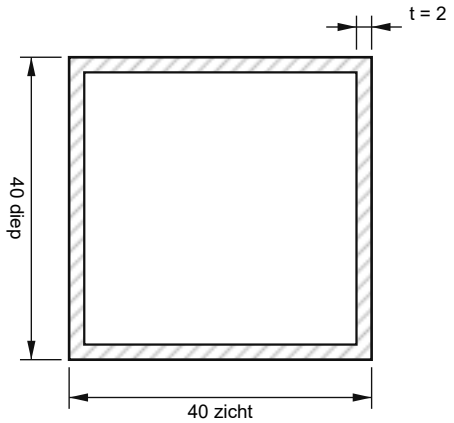

koker 40x40x2 (1:1)

boven = de kant met de greep

Bewerking en verbindingen

Bewerking: verstek 45° · verstek 45°

V1: 2 x verstek 45° met pos 1 (Kozijn: stijl)

Titel: **Pos 2: Kozijn: bovenregel**			
Deur: Kathedraal · opening 1000 x 2600		Tekeningnummer: **TD-34-02**	
Maten en toleranties: mm · ISO 2768-m · eerste hoek	Opgesteld: Ian · laswerken	Uitgifte: 2026-11-10	Blad: 2 / 28


3 2 x Kader: staander

S235, koker 40x40x2 · L = 2541 · zagen 45°/45° · 5,87 kg/st


Aanzicht (1:20)



Waar het stuk zit

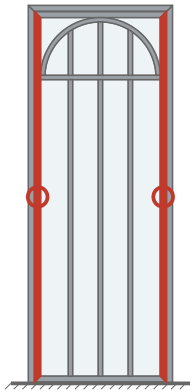


Detail A (1:1): linker uiteinde

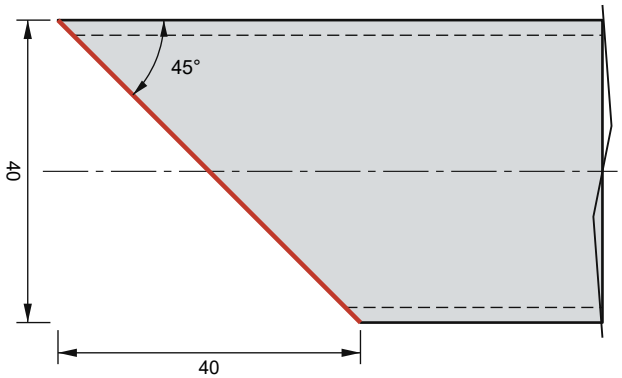


Verstek 45°: lange kant is 40 langer dan de korte

Detail B (1:1): rechter uiteinde

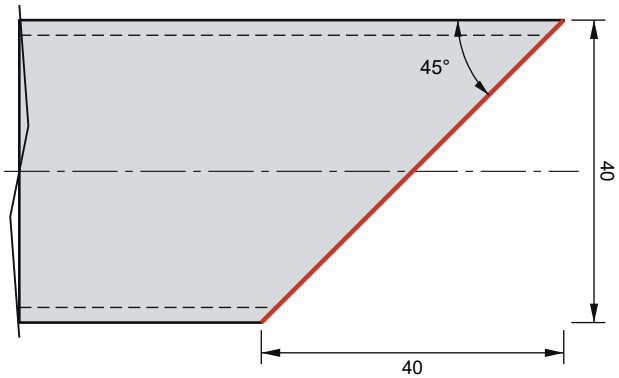

Verstek 45°: lange kant is 40 langer dan de korte

Doorsnede (arcering = materiaal)

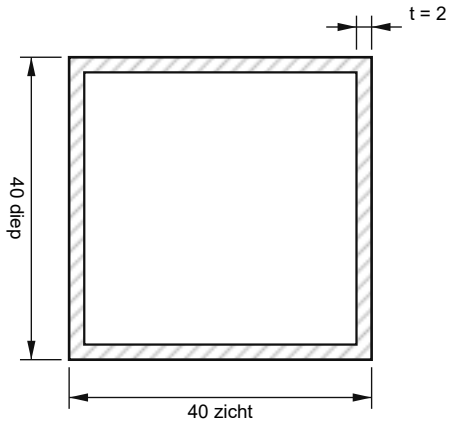

koker 40x40x2 (1:1)

boven = de kant met de greep

Bewerking en verbindingen


Bewerking: verstek 45° · verstek 45°
V2: 4 x verstek 45° met pos 4 (Kader: regel)
T1: 2 x t-verbinding (stomp) met pos 5 (Roede horizontaal: kern)

Titel: **Pos 3: Kader: staander**			
Deur: Kathedraal · opening 1000 x 2600		Tekeningnummer: **TD-34-03**	
Maten en toleranties: mm · ISO 2768-m · eerste hoek	Opgesteld: Ian · laswerken	Uitgifte: 2026-11-10	Blad: 3 / 28


4 2 x Kader: regel

S235, koker 40x40x2 · L = 902 · zagen 45°/45° · 2,08 kg/st


Aanzicht (1:10)

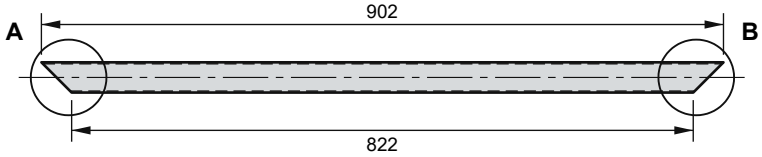

Waar het stuk zit

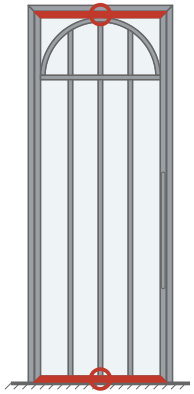


Detail A (1:1): linker uiteinde

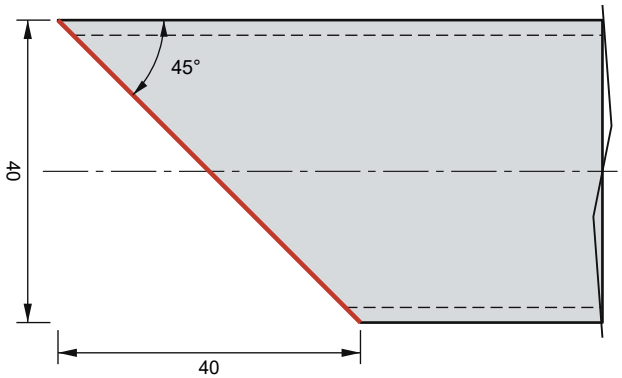


Verstek 45°: lange kant is 40 langer dan de korte

Detail B (1:1): rechter uiteinde

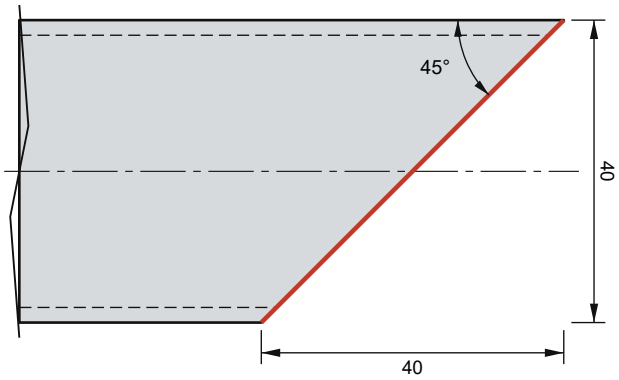

Verstek 45°: lange kant is 40 langer dan de korte

Doorsnede (arcering = materiaal)

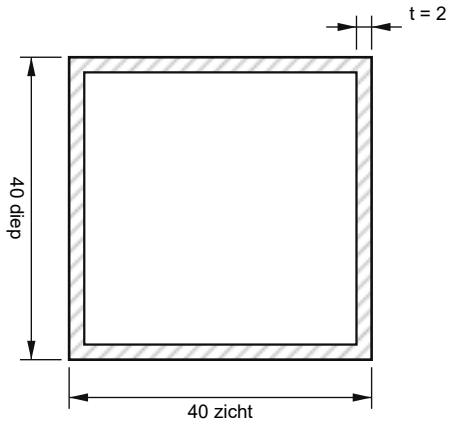

koker 40x40x2 (1:1)

boven = de kant met de greep

Bewerking en verbindingen


Bewerking: verstek 45° · verstek 45°
V2: 4 x verstek 45° met pos 3 (Kader: staander)
T2: 3 x t-verbinding (stomp) met pos 7 (Roede verticaal: kern)

Titel: **Pos 4: Kader: regel**			
Deur: Kathedraal · opening 1000 x 2600		Tekeningnummer: **TD-34-04**	
Maten en toleranties: mm · ISO 2768-m · eerste hoek	Opgesteld: Ian · laswerken	Uitgifte: 2026-11-10	Blad: 4 / 28


5 1 x Roede horizontaal: kern

S235, platstaal 20x10 · L = 822 · zagen 90°/90° · 1,29 kg/st


Waar het stuk zit

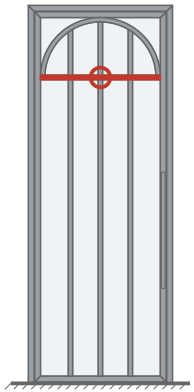

Aanzicht (1:5)

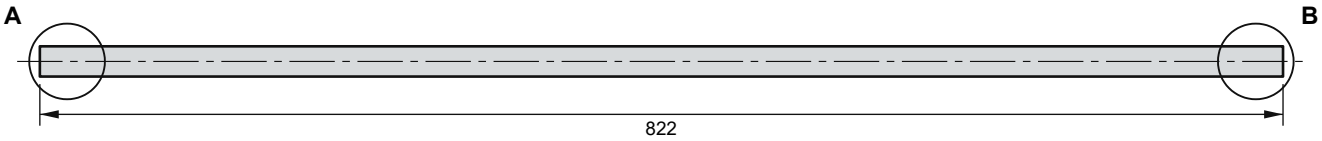


Detail A (2:1): linker uiteinde

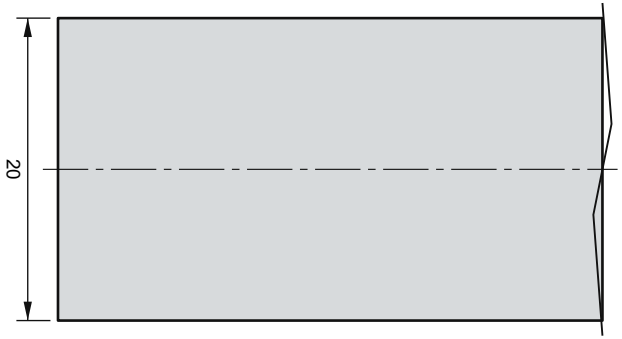


Recht afzagen (90°)

Detail B (2:1): rechter uiteinde

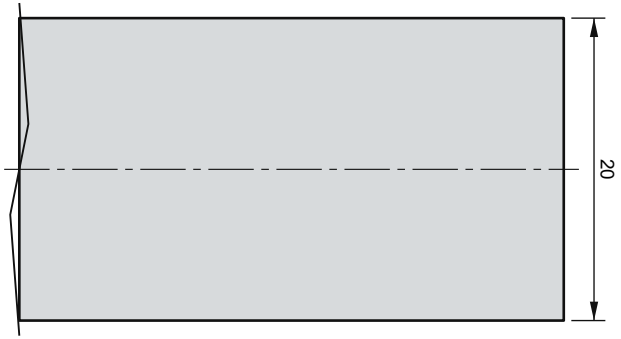

Recht afzagen (90°)

Doorsnede (arcering = materiaal)

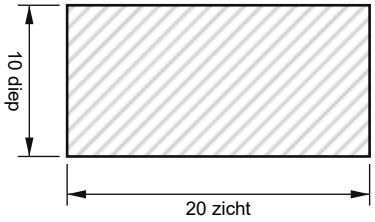

platstaal 20x10 (2:1)

boven = de kant met de greep

Bewerking en verbindingen


Bewerking: recht · recht; M4 om de 250 aan de achterkant
T1: 2 x t-verbinding (stomp) met pos 3 (Kader: staander)
T3: 3 x t-verbinding (stomp) met pos 7 (Roede verticaal: kern)
S1: 2 x schuin tegen de boog met pos 9 (Roede tot in de boog: kern)
S2: 1 x schuin tegen de boog met pos 11 (Roede tot in de boog: kern)
B1: 2 x boog op kalf, poot of kader met pos 19 (Boogroede: kern)

Titel: **Pos 5: Roede horizontaal: kern**			
Deur: Kathedraal · opening 1000 x 2600		Tekeningnummer: **TD-34-05**	
Maten en toleranties: mm · ISO 2768-m · eerste hoek	Opgesteld: Ian · laswerken	Uitgifte: 2026-11-10	Blad: 5 / 28


6 2 x Roede horizontaal: lat voor en achter

S235, platstaal 30x3 · L = 822 · zagen 90°/90° · 0,58 kg/st


Waar het stuk zit

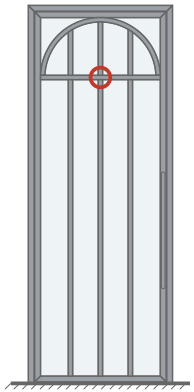

Aanzicht (1:5)

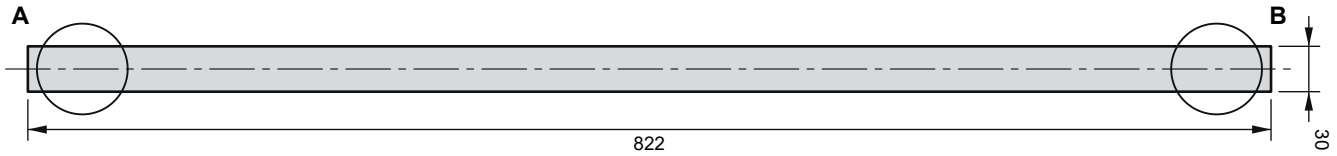


Detail A (1:1): linker uiteinde

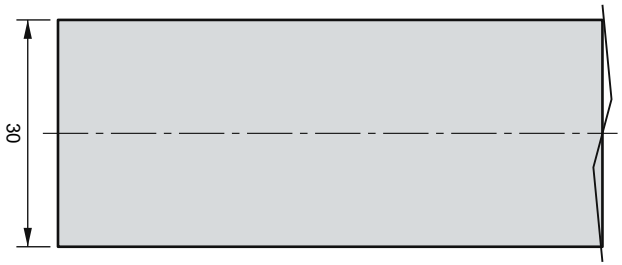


Recht afzagen (90°)

Detail B (1:1): rechter uiteinde

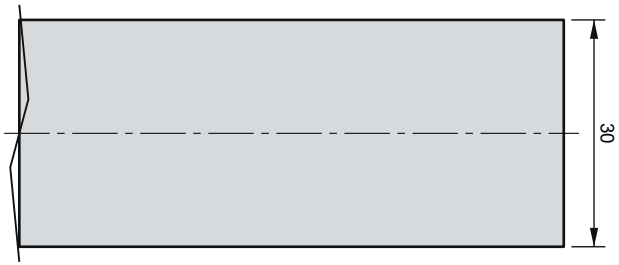

Recht afzagen (90°)

Doorsnede (arcering = materiaal)

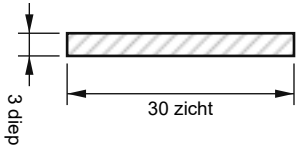

platstaal 30x3 (1:1)

boven = de kant met de greep

Bewerking en verbindingen

Bewerking: recht · recht; voor gelast, achter geschroefd


Hechten om de 150 en lassen (voor) of M4 verzonken om de 250 (achter): zie de werkwijze

Titel: **Pos 6: Roede horizontaal: lat voor en achter**			
Deur: Kathedraal · opening 1000 x 2600		Tekeningnummer: **TD-34-06**	
Maten en toleranties: mm · ISO 2768-m · eerste hoek	Opgesteld: Ian · laswerken	Uitgifte: 2026-11-10	Blad: 6 / 28

7 3 x Roede verticaal: kern

S235, platstaal 20x10 · L = 2035 · zagen 90°/90° · 3,19 kg/st


Waar het stuk zit

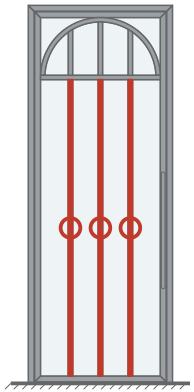

Aanzicht (1:20)




Detail A (2:1): linker uiteinde

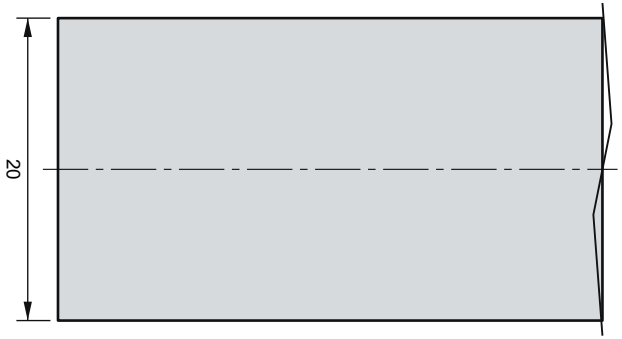


Recht afzagen (90°)

Detail B (2:1): rechter uiteinde

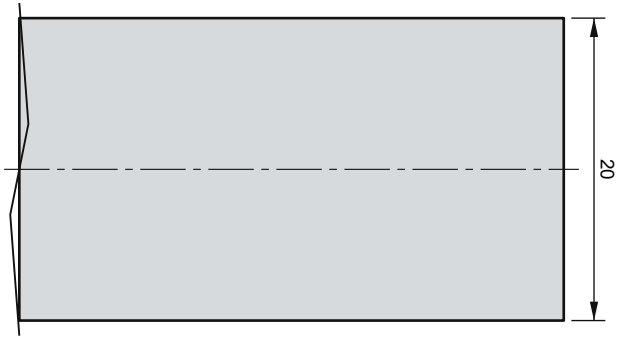

Recht afzagen (90°)

Doorsnede (arcering = materiaal)

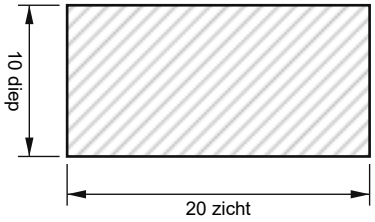

platstaal 20x10 (2:1)

boven = de kant met de greep

Bewerking en verbindingen

Bewerking: recht · recht; M4 om de 250 aan de achterkant
T2: 3 x t-verbinding (stomp) met pos 4 (Kader: regel)
T3: 3 x t-verbinding (stomp) met pos 5 (Roede horizontaal: kern)

Titel: **Pos 7: Roede verticaal: kern**			
Deur: Kathedraal · opening 1000 x 2600		Tekeningnummer: **TD-34-07**	
Maten en toleranties: mm · ISO 2768-m · eerste hoek	Opgesteld: Ian · laswerken	Uitgifte: 2026-11-10	Blad: 7 / 28


8 6 x Roede verticaal: lat voor en achter

S235, platstaal 30x3 · L = 2035 · zagen 90°/90° · 1,44 kg/st


Aanzicht (1:20)



Waar het stuk zit

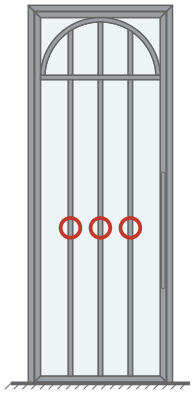


Detail A (1:1): linker uiteinde

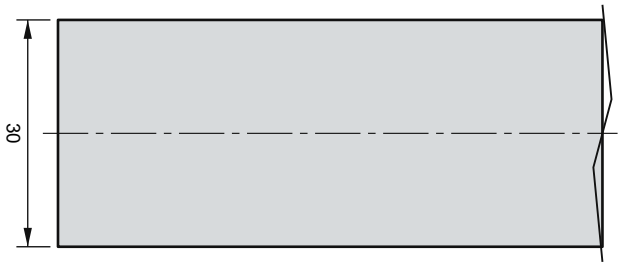


Recht afzagen (90°)

Detail B (1:1): rechter uiteinde

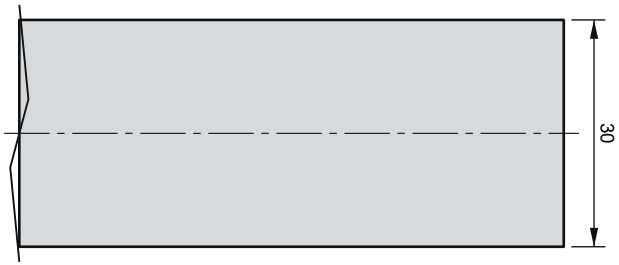

Recht afzagen (90°)

Doorsnede (arcering = materiaal)

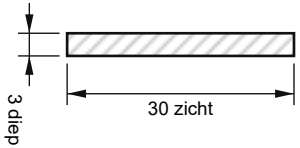

platstaal 30x3 (1:1)

boven = de kant met de greep

Bewerking en verbindingen

Bewerking: recht · recht; voor gelast, achter geschroefd


Hechten om de 150 en lassen (voor) of M4 verzonken om de 250 (achter): zie de werkwijze

Titel: **Pos 8: Roede verticaal: lat voor en achter**			
Deur: Kathedraal · opening 1000 x 2600		Tekeningnummer: **TD-34-08**	
Maten en toleranties: mm · ISO 2768-m · eerste hoek	Opgesteld: Ian · laswerken	Uitgifte: 2026-11-10	Blad: 8 / 28


9 2 x Roede tot in de boog: kern

S235, platstaal 20x10 · L = 312 · zagen 90°/57° · 0,49 kg/st


Waar het stuk zit

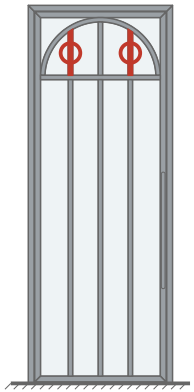

Aanzicht (1:2)

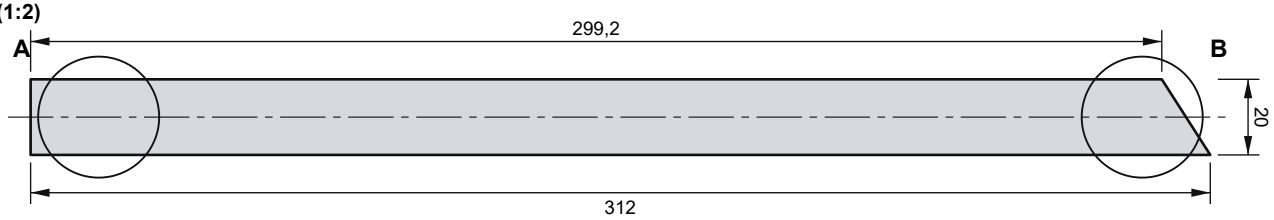


Detail A (2:1): linker uiteinde

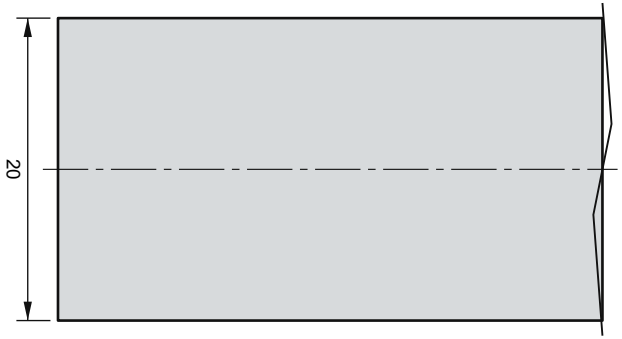


Recht afzagen (90°)

Detail B (2:1): rechter uiteinde

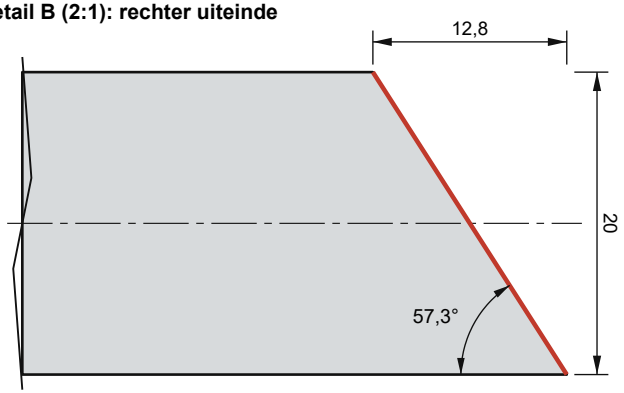

Schuin 57,3°: lange kant is 12,8 langer dan de korte

Doorsnede (arcering = materiaal)

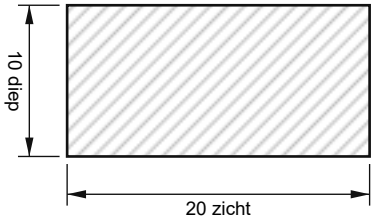

platstaal 20x10 (2:1)

boven = de kant met de greep

Bewerking en verbindingen


Bewerking: recht · schuin 33° (volgens de boog); M4 om de 250 aan de achterkant
S1: 2 x schuin tegen de boog met pos 5 (Roede horizontaal: kern)
S3: 2 x schuin tegen de boog met pos 19 (Boogroede: kern)

Titel: **Pos 9: Roede tot in de boog: kern**			
Deur: Kathedraal · opening 1000 x 2600		Tekeningnummer: **TD-34-09**	
Maten en toleranties: mm · ISO 2768-m · eerste hoek	Opgesteld: Ian · laswerken	Uitgifte: 2026-11-10	Blad: 9 / 28


10 — 4 x Roede tot in de boog: lat voor en achter

S235, platstaal 30x3 · L = 315 · zagen 90°/57° · 0,22 kg/st


Waar het stuk zit

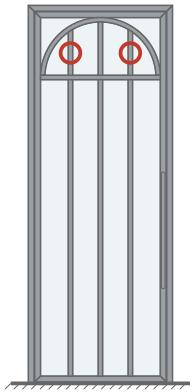

Aanzicht (1:2)

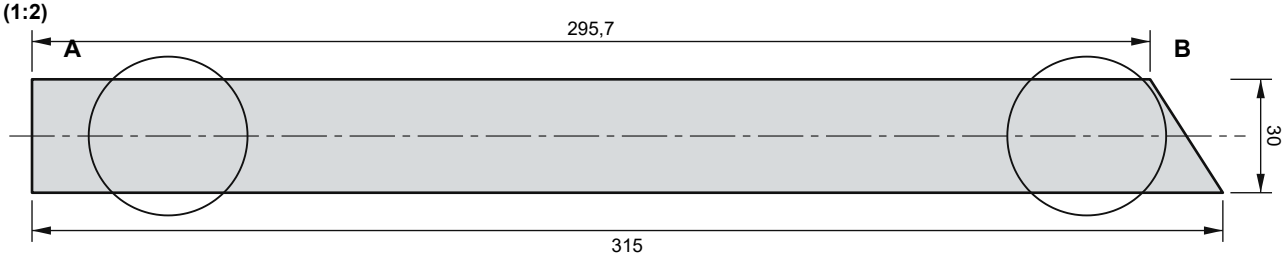


Detail A (1:1): linker uiteinde

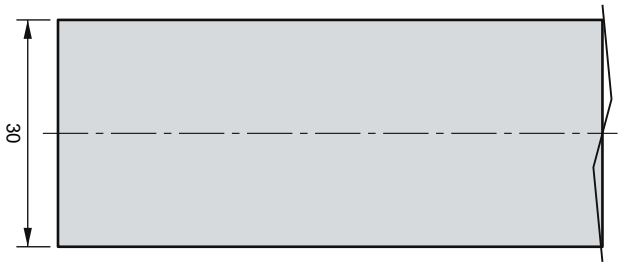


Recht afzagen (90°)

Detail B (1:1): rechter uiteinde

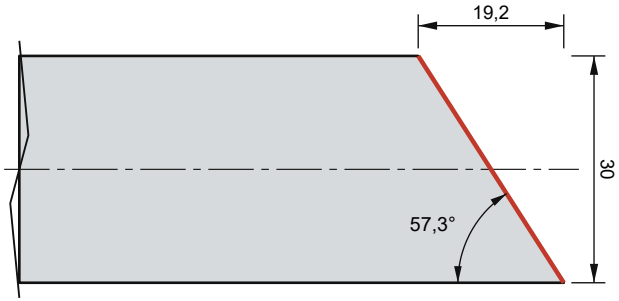

Schuin 57,3°: lange kant is 19,2 langer dan de korte

Doorsnede (arcering = materiaal)

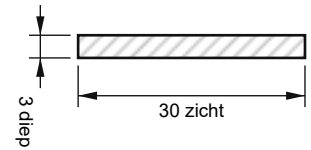

platstaal 30x3 (1:1)

boven = de kant met de greep

Bewerking en verbindingen

Bewerking: recht · schuin 33° (volgens de boog); voor gelast, achter geschroefd


Hechten om de 150 en lassen (voor) of M4 verzonken om de 250 (achter): zie de werkwijze

Titel: **Pos 10: Roede tot in de boog: lat voor en achter**			
Deur: Kathedraal · opening 1000 x 2600		Tekeningnummer: **TD-34-10**	
Maten en toleranties: mm · ISO 2768-m · eerste hoek	Opgesteld: Ian · laswerken	Uitgifte: 2026-11-10	Blad: 10 / 28


11 1 x Roede tot in de boog: kern

S235, platstaal 20x10 · L = 366 · zagen 90°/90° · 0,57 kg/st


Aanzicht (1:5)

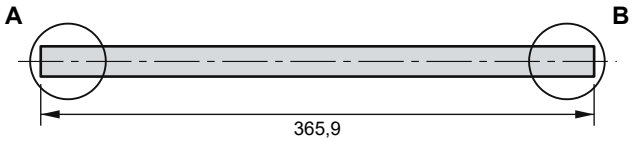

Waar het stuk zit

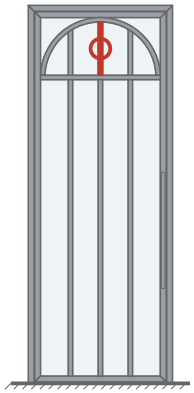


Detail A (2:1): linker uiteinde

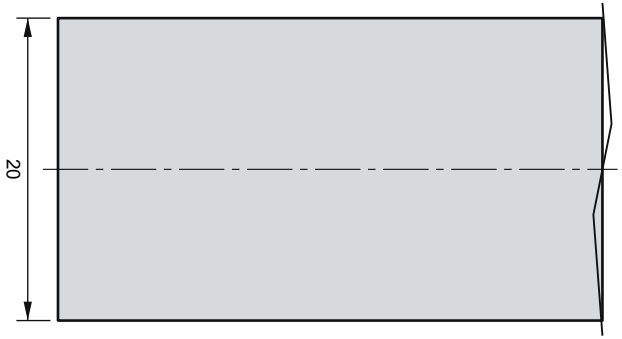


Recht afzagen (90°)

Detail B (2:1): rechter uiteinde

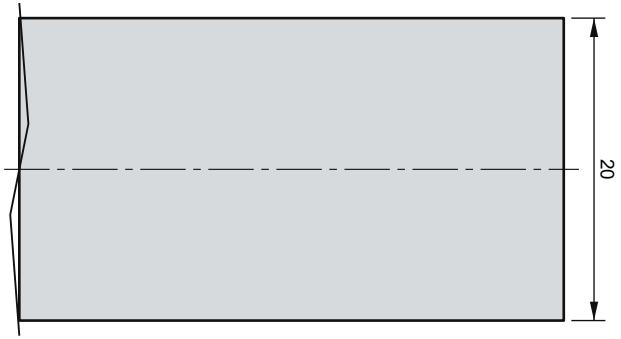

Recht afzagen (90°)

Doorsnede (arcering = materiaal)

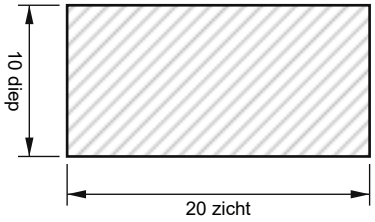

platstaal 20x10 (2:1)

boven = de kant met de greep

Bewerking en verbindingen


Bewerking: recht · recht; M4 om de 250 aan de achterkant
S2: 1 x schuin tegen de boog met pos 5 (Roede horizontaal: kern)
S4: 1 x schuin tegen de boog met pos 19 (Boogroede: kern)

Titel: **Pos 11: Roede tot in de boog: kern**			
Deur: Kathedraal · opening 1000 x 2600		Tekeningnummer: **TD-34-11**	
Maten en toleranties: mm · ISO 2768-m · eerste hoek	Opgesteld: Ian · laswerken	Uitgifte: 2026-11-10	Blad: 11 / 28


12 2 x Roede tot in de boog: lat voor en achter

S235, platstaal 30x3 · L = 366 · zagen 90°/90° · 0,26 kg/st


Waar het stuk zit

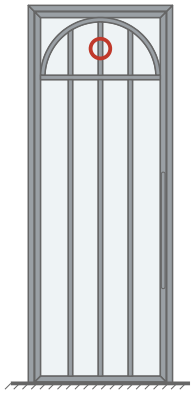

Aanzicht (1:5)

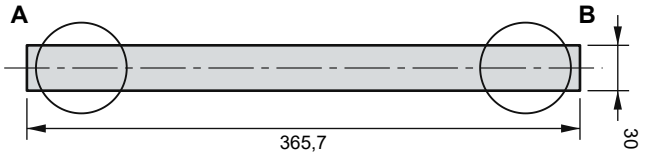


Detail A (1:1): linker uiteinde

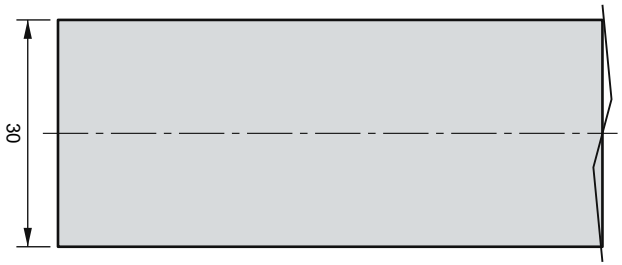


Recht afzagen (90°)

Detail B (1:1): rechter uiteinde

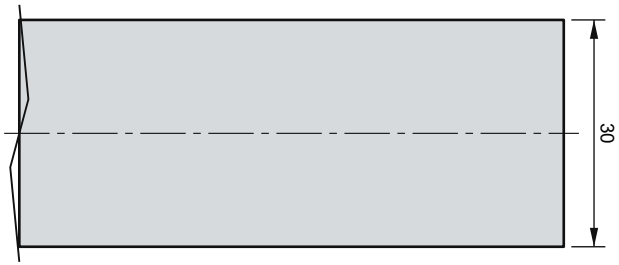

Recht afzagen (90°)

Doorsnede (arcering = materiaal)

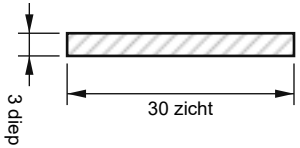

platstaal 30x3 (1:1)

boven = de kant met de greep

Bewerking en verbindingen

Bewerking: recht · recht; voor gelast, achter geschroefd

Hechten om de 150 en lassen (voor) of M4 verzonken om de 250 (achter): zie de werkwijze

Titel: **Pos 12: Roede tot in de boog: lat voor en achter**			
Deur: Kathedraal · opening 1000 x 2600		Tekeningnummer: **TD-34-12**	
Maten en toleranties: mm · ISO 2768-m · eerste hoek	Opgesteld: Ian · laswerken	Uitgifte: 2026-11-10	Blad: 12 / 28


13 4 x Glaslat

S235, platstaal 15x4 · L = 411 · 0,19 kg/st


Aanzicht (1:5)



Waar het stuk zit

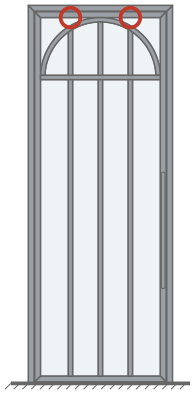


Detail A (2:1): linker uiteinde

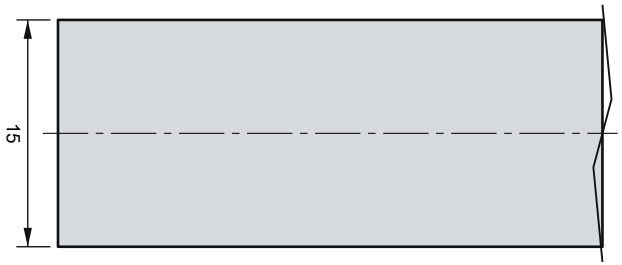

Recht afzagen (90°)

Detail B (2:1): rechter uiteinde

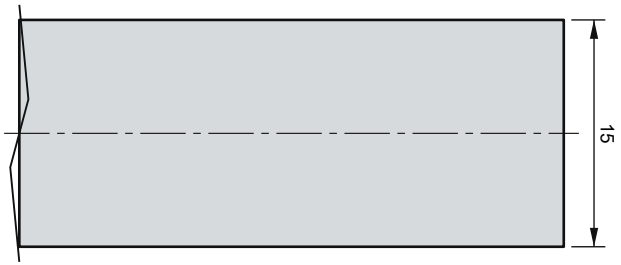

Recht afzagen (90°)

Doorsnede (arcering = materiaal)



platstaal 15x4 (2:1)

boven = de kant met de greep

Bewerking en verbindingen

Bewerking: recht; voor gelast, achter geschroefd (M4 verzonken om de 250)


Hechten om de 150 en lassen (voor) of M4 verzonken om de 250 (achter): zie de werkwijze

Titel: **Pos 13: Glaslat**			
Deur: Kathedraal · opening 1000 x 2600		Tekeningnummer: **TD-34-13**	
Maten en toleranties: mm · ISO 2768-m · eerste hoek	Opgesteld: Ian · laswerken	Uitgifte: 2026-11-10	Blad: 13 / 28


14 4 x Glaslat

S235, platstaal 15x4 · L = 396 · 0,19 kg/st


Aanzicht (1:5)

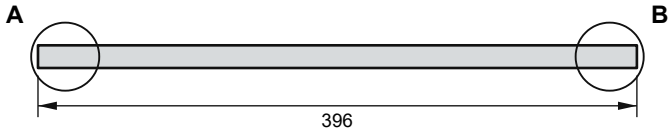

Waar het stuk zit

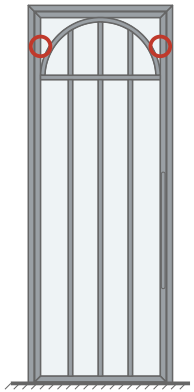


Detail A (2:1): linker uiteinde

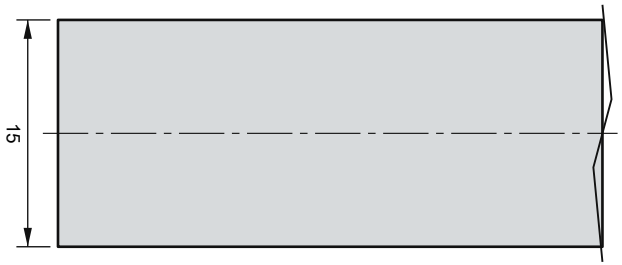

Recht afzagen (90°)

Detail B (2:1): rechter uiteinde

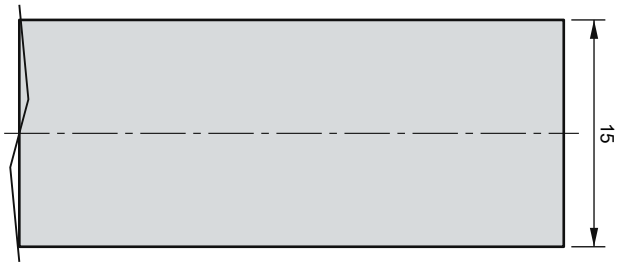

Recht afzagen (90°)

Doorsnede (arcering = materiaal)



platstaal 15x4 (2:1)

boven = de kant met de greep

Bewerking en verbindingen

Bewerking: recht; voor gelast, achter geschroefd (M4 verzonken om de 250)


Hechten om de 150 en lassen (voor) of M4 verzonken om de 250 (achter): zie de werkwijze

Titel: **Pos 14: Glaslat**			
Deur: Kathedraal · opening 1000 x 2600		Tekeningnummer: **TD-34-14**	
Maten en toleranties: mm · ISO 2768-m · eerste hoek	Opgesteld: Ian · laswerken	Uitgifte: 2026-11-10	Blad: 14 / 28


15 4 x Glaslat

S235, platstaal 15x4 · L = 191 · 0,09 kg/st


Aanzicht (1:2)

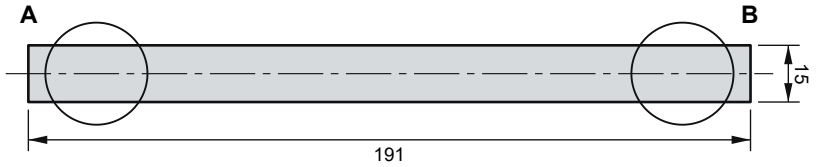

Waar het stuk zit

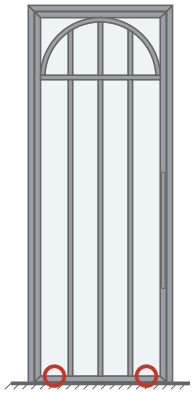


Detail A (2:1): linker uiteinde

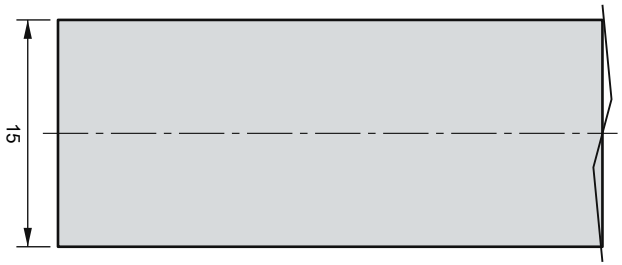

Recht afzagen (90°)

Detail B (2:1): rechter uiteinde

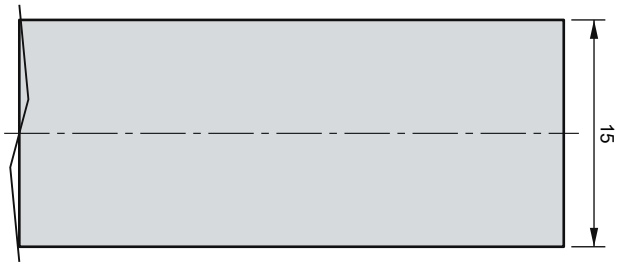

Recht afzagen (90°)

Doorsnede (arcering = materiaal)



platstaal 15x4 (2:1)

boven = de kant met de greep

Bewerking en verbindingen

Bewerking: recht; voor gelast, achter geschroefd (M4 verzonken om de 250)

Hechten om de 150 en lassen (voor) of M4 verzonken om de 250 (achter): zie de werkwijze

Titel: **Pos 15: Glaslat**			
Deur: Kathedraal · opening 1000 x 2600		Tekeningnummer: **TD-34-15**	
Maten en toleranties: mm · ISO 2768-m · eerste hoek	Opgesteld: Ian · laswerken	Uitgifte: 2026-11-10	Blad: 15 / 28


16 4 x Glaslat

S235, platstaal 15x4 · L = 2035 · 0,96 kg/st


Aanzicht (1:20)



Waar het stuk zit

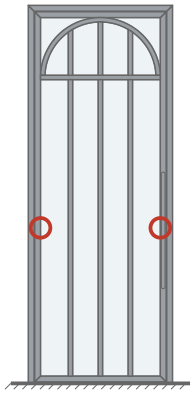


Detail A (2:1): linker uiteinde

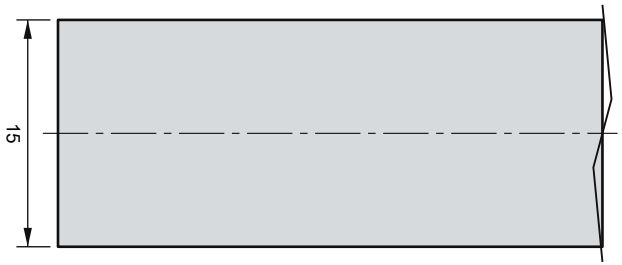

Recht afzagen (90°)

Detail B (2:1): rechter uiteinde

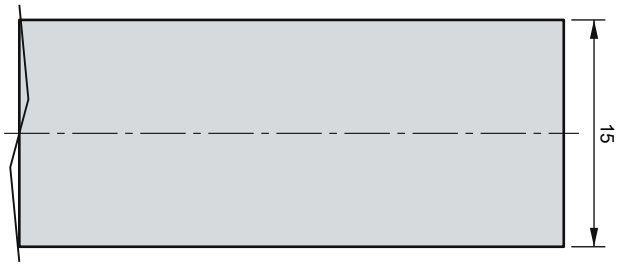

Recht afzagen (90°)

Doorsnede (arcering = materiaal)



platstaal 15x4 (2:1)

boven = de kant met de greep

Bewerking en verbindingen

Bewerking: recht; voor gelast, achter geschroefd (M4 verzonken om de 250)


Hechten om de 150 en lassen (voor) of M4 verzonken om de 250 (achter): zie de werkwijze

Titel: **Pos 16: Glaslat**			
Deur: Kathedraal · opening 1000 x 2600		Tekeningnummer: **TD-34-16**	
Maten en toleranties: mm · ISO 2768-m · eerste hoek	Opgesteld: Ian · laswerken	Uitgifte: 2026-11-10	Blad: 16 / 28


17 4 x Glaslat

S235, platstaal 15x4 · L = 176 · 0,08 kg/st


Waar het stuk zit

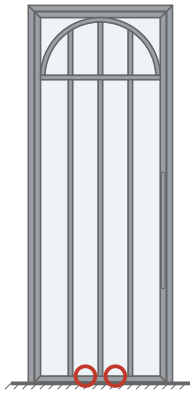

Aanzicht (1:1)

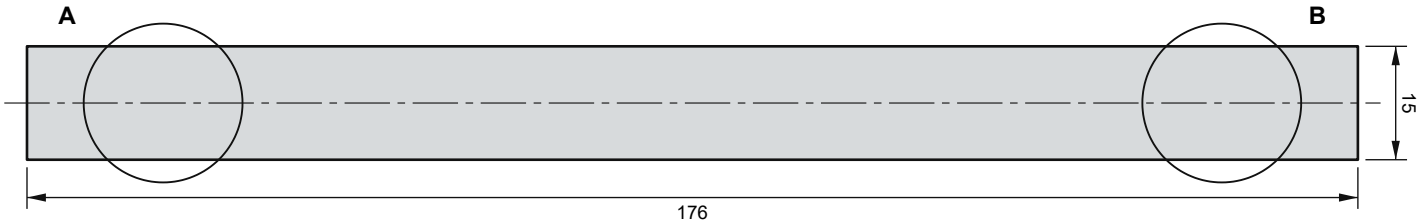


Detail A (2:1): linker uiteinde

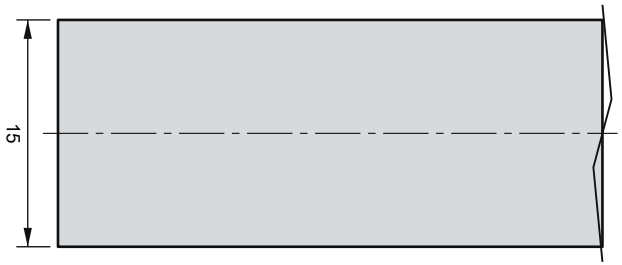

Recht afzagen (90°)

Detail B (2:1): rechter uiteinde

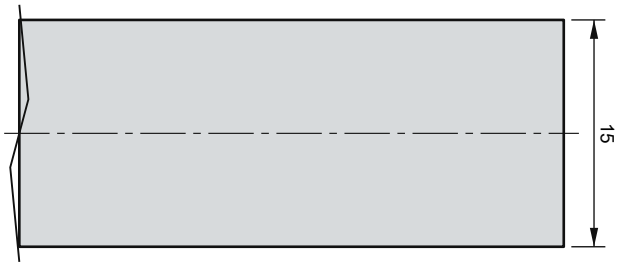

Recht afzagen (90°)

Doorsnede (arcering = materiaal)



platstaal 15x4 (2:1)

boven = de kant met de greep

Bewerking en verbindingen


Bewerking: recht; voor gelast, achter geschroefd (M4 verzonken om de 250)
Hechten om de 150 en lassen (voor) of M4 verzonken om de 250 (achter): zie de werkwijze

Titel: **Pos 17: Glaslat**			
Deur: Kathedraal · opening 1000 x 2600		Tekeningnummer: **TD-34-17**	
Maten en toleranties: mm · ISO 2768-m · eerste hoek	Opgesteld: Ian · laswerken	Uitgifte: 2026-11-10	Blad: 17 / 28


18 2 x Greep (voor en achter)

S235, rond Ø25 · L = 800 · 3,08 kg/st


Waar het stuk zit

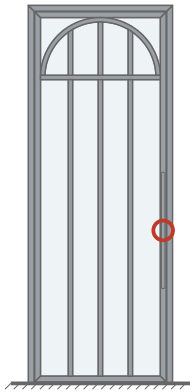

Aanzicht (1:5)

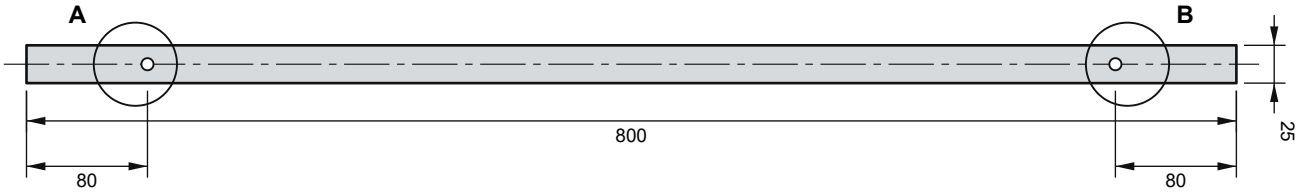


Detail A (1:2): linker uiteinde

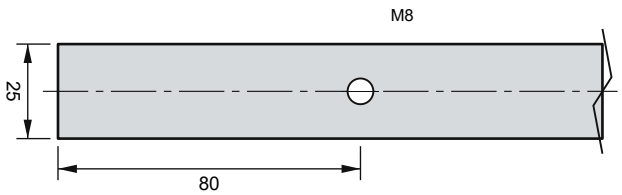


Recht afzagen (90°)

Detail B (1:2): rechter uiteinde

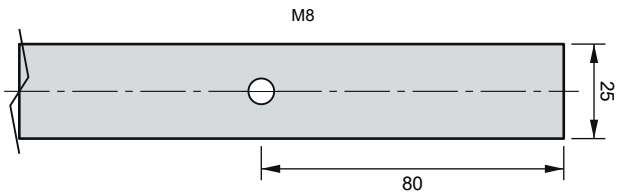

Recht afzagen (90°)

Doorsnede (arcering = materiaal)

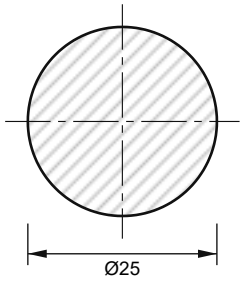

rond Ø25 (1:1)

Bewerking en verbindingen


Bewerking: uiteinden rond slijpen; 2 x M8 op 80 van de uiteinden

Titel: **Pos 18: Greep (voor en achter)**			
Deur: Kathedraal · opening 1000 x 2600		Tekeningnummer: **TD-34-18**	
Maten en toleranties: mm · ISO 2768-m · eerste hoek	Opgesteld: Ian · laswerken	Uitgifte: 2026-11-10	Blad: 18 / 28


19 1 x Boogroede: kern

S235, plaat 10 mm · R 396 x 20, 175.7° · 1,91 kg/st


Aanzicht (1:5), lasergesneden uit plaat 10 mm

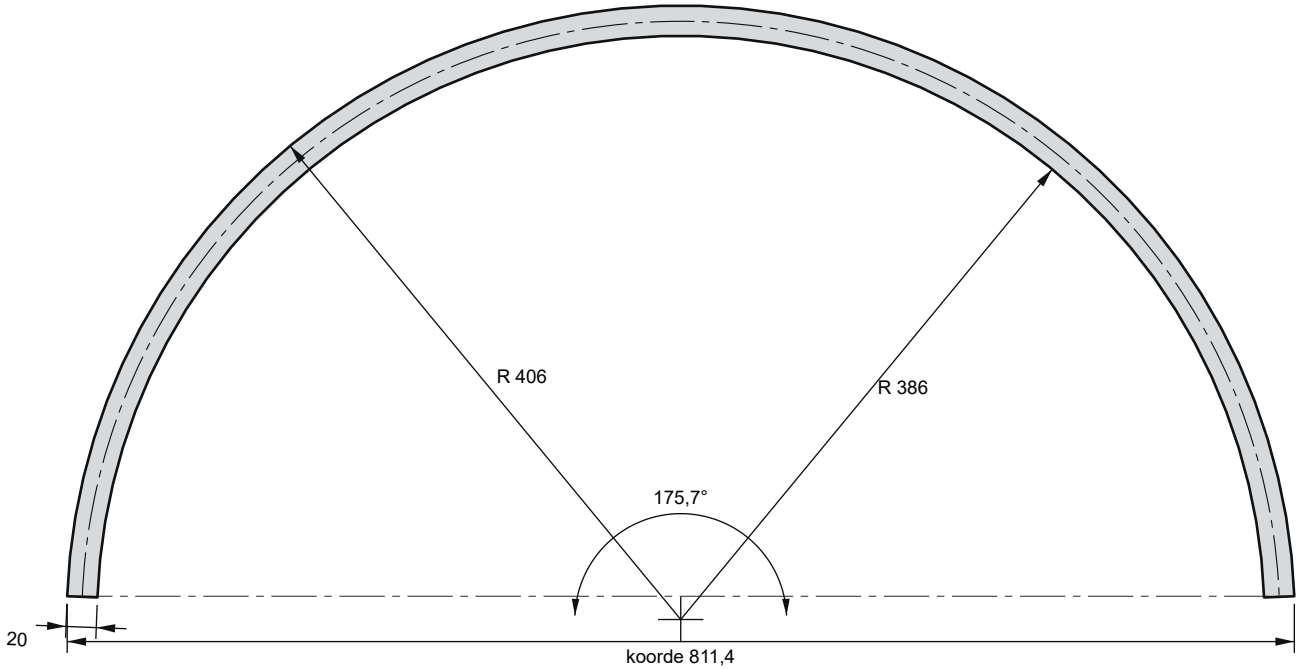

Waar het stuk zit

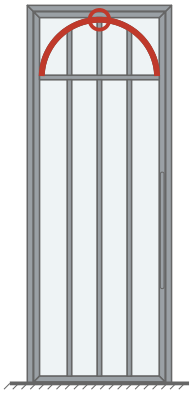

Doorsnede (lagen)

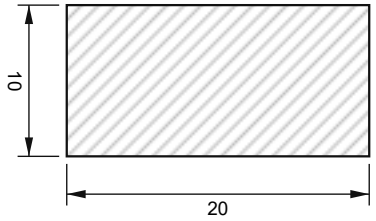

2× · één plaat

Bewerking en verbindingen


Bewerking: op de mal 1:1 leggen en hechten
S3: 2 x schuin tegen de boog met pos 9 (Roede tot in de boog: kern)
S4: 1 x schuin tegen de boog met pos 11 (Roede tot in de boog: kern)
B1: 2 x boog op kalf, poot of kader met pos 5 (Roede horizontaal: kern)

Titel: **Pos 19: Boogroede: kern**			
Deur: Kathedraal · opening 1000 x 2600		Tekeningnummer: **TD-34-19**	
Maten en toleranties: mm · ISO 2768-m · eerste hoek	Opgesteld: Ian · laswerken	Uitgifte: 2026-11-10	Blad: 19 / 28


20 2 x Boogroede: lat voor en achter

S235, plaat 3 mm · R 396 x 30, 175.7° · 0,86 kg/st


Aanzicht (1:5), lasergesneden uit plaat 3 mm

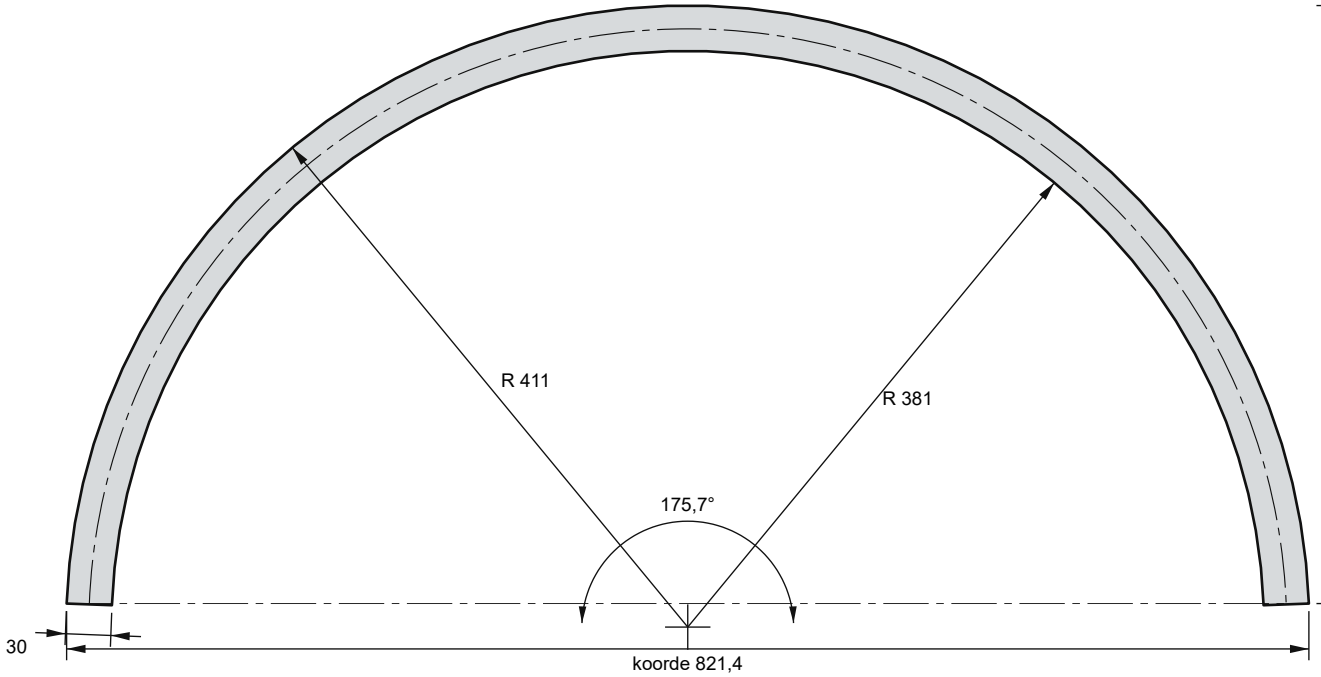

Waar het stuk zit

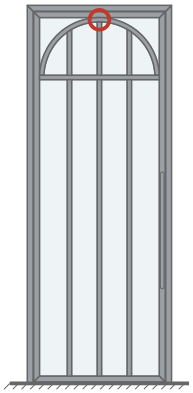

Doorsnede (lagen)

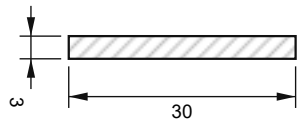

1:1 · één plaat

Bewerking en verbindingen


Bewerking: voor gelast, achter geschroefd

Titel: **Pos 20: Boogroede: lat voor en achter**			
Deur: Kathedraal · opening 1000 x 2600		Tekeningnummer: **TD-34-20**	
Maten en toleranties: mm · ISO 2768-m · eerste hoek	Opgesteld: Ian · laswerken	Uitgifte: 2026-11-10	Blad: 20 / 28


21 1 x Taatsplaat onder

S235, plaat 8 mm · 36 x 220 · 0,5 kg/st

Aanzicht (1:2)

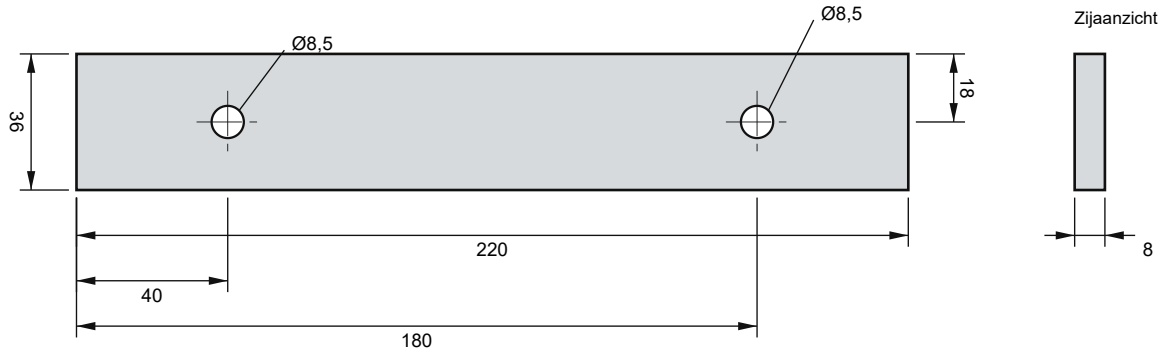

Waar het stuk zit

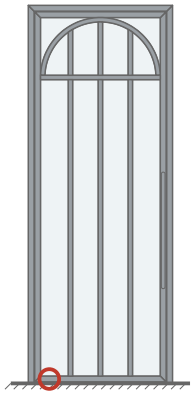

Plaat

S235, plaat 8 mm

36 x 220 x 8 mm

Lasersnijden op de DXF; braam eraf

Bewerking en verbindingen


Bewerking: 2 x Ø8,5 voor het scharnier; in de onderregel gelast

Titel: **Pos 21: Taatsplaat onder**			
Deur: Kathedraal · opening 1000 x 2600		Tekeningnummer: **TD-34-21**	
Maten en toleranties: mm · ISO 2768-m · eerste hoek	Opgesteld: Ian · laswerken	Uitgifte: 2026-11-10	Blad: 21 / 28

22 1 x Taatsplaat boven

S235, plaat 8 mm · 36 x 140 · 0,32 kg/st

Aanzicht (1:1)

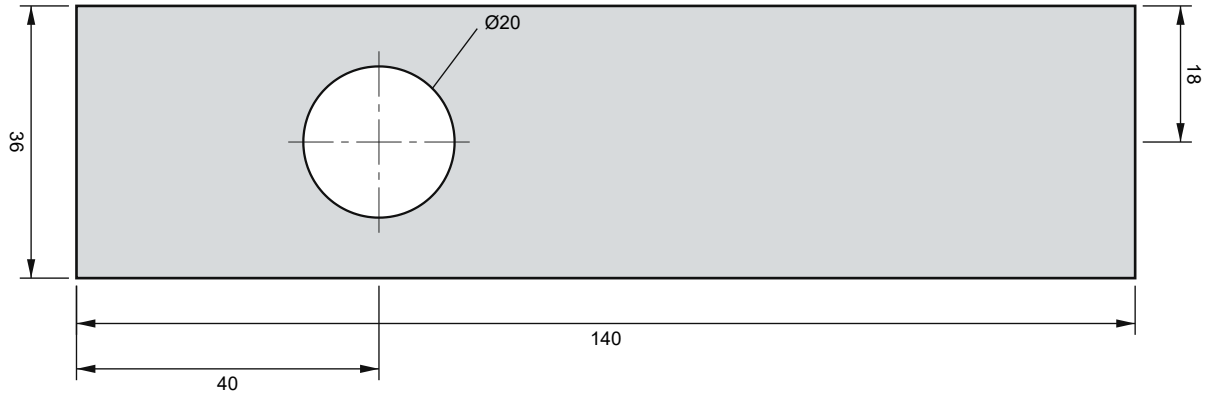

Zijaanzicht




Plaat

S235, plaat 8 mm

36 x 140 x 8 mm

Lasersnijden op de DXF; braam eraf

Waar het stuk zit

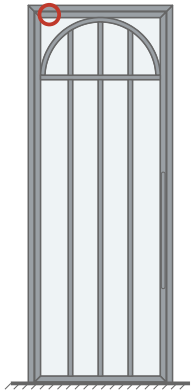

Bewerking en verbindingen


Bewerking: Ø20 voor de bovenpen; in de bovenregel gelast

Titel: **Pos 22: Taatsplaat boven**			
Deur: Kathedraal · opening 1000 x 2600		Tekeningnummer: **TD-34-22**	
Maten en toleranties: mm · ISO 2768-m · eerste hoek	Opgesteld: Ian · laswerken	Uitgifte: 2026-11-10	Blad: 22 / 28


23 2 x Greephouder

S235, plaat 10 mm · 25 x 40 · 0,08 kg/st


Aanzicht (2:1)

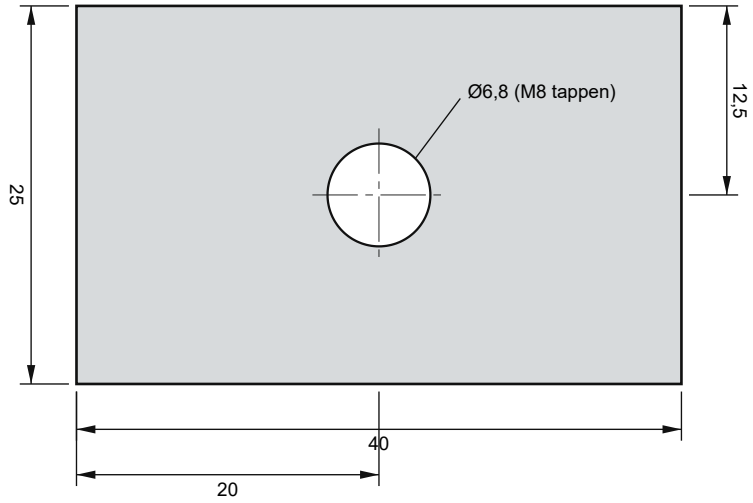

Zijaanzicht

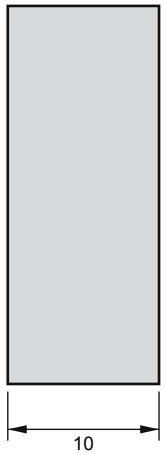

Waar het stuk zit

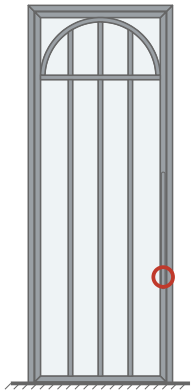

Plaat

S235, plaat 10 mm

25 x 40 x 10 mm

Lasersnijden op de DXF; braam eraf

Bewerking en verbindingen


Bewerking: M8 tappen (boor Ø6,8); op de staander gelast

Titel: **Pos 23: Greephouder**			
Deur: Kathedraal · opening 1000 x 2600		Tekeningnummer: **TD-34-23**	
Maten en toleranties: mm · ISO 2768-m · eerste hoek	Opgesteld: Ian · laswerken	Uitgifte: 2026-11-10	Blad: 23 / 28


24 2 x Ruit met vorm (DXF)

gelaagd 44.2 helder · 419 x 404 · 0,9 kg/st

Aanzicht (1:5): daglicht, de ruit is 4 mm groter rondom

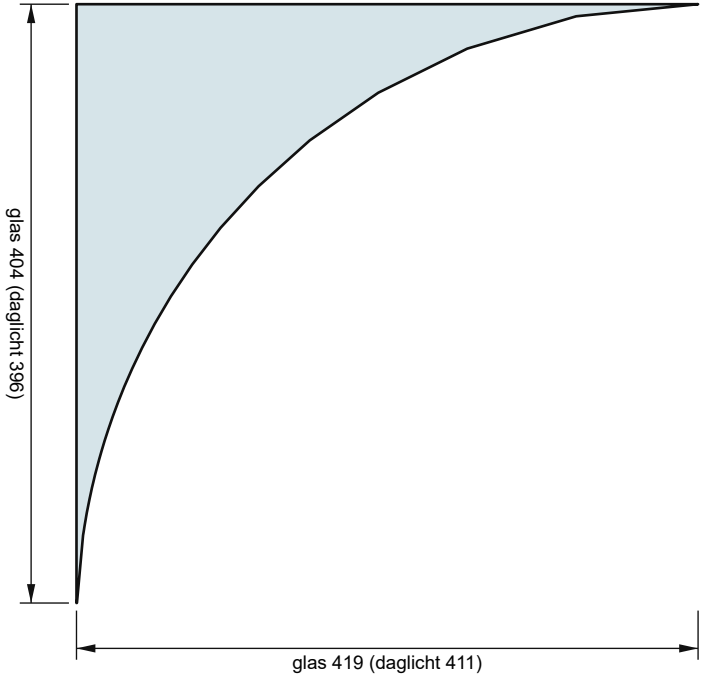

Waar het stuk zit

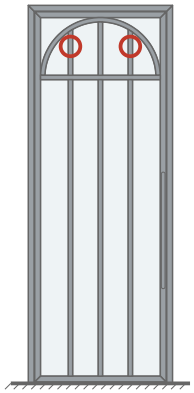

Opbouw (2:1)



gelaagd 44.2 helder

altijd veiligheidsglas (EN 12543 / EN 12150)

Bewerking en verbindingen


Bewerking: veiligheidsglas; snijden op de DXF (daglicht + 4 rondom)

Titel: **Pos 24: Ruit met vorm (DXF)**			
Deur: Kathedraal · opening 1000 x 2600		Tekeningnummer: **TD-34-24**	
Maten en toleranties: mm · ISO 2768-m · eerste hoek	Opgesteld: Ian · laswerken	Uitgifte: 2026-11-10	Blad: 24 / 28


25 2 x Ruit

gelaagd 44.2 helder · 199 x 2043 · 8,43 kg/st

Aanzicht (1:20): daglicht, de ruit is 4 mm groter rondom

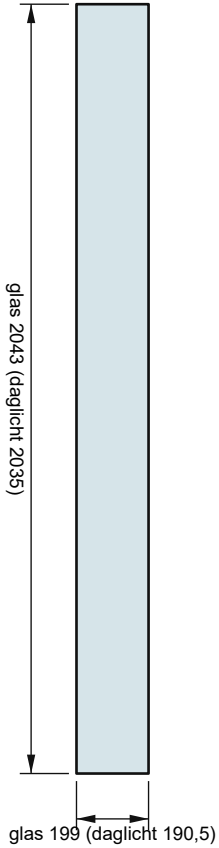

Waar het stuk zit

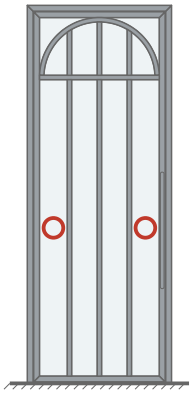

Opbouw (2:1)



gelaagd 44.2 helder

altijd veiligheidsglas (EN 12543 / EN 12150)

Bewerking en verbindingen


Bewerking: veiligheidsglas; glasmaat = daglicht + 4 rondom

Titel: **Pos 25: Ruit**			
Deur: Kathedraal · opening 1000 x 2600		Tekeningnummer: **TD-34-25**	
Maten en toleranties: mm · ISO 2768-m · eerste hoek	Opgesteld: Ian · laswerken	Uitgifte: 2026-11-10	Blad: 25 / 28


26 2 x Ruit

gelaagd 44.2 helder · 184 x 2043 · 7,8 kg/st

Aanzicht (1:20): daglicht, de ruit is 4 mm groter rondom

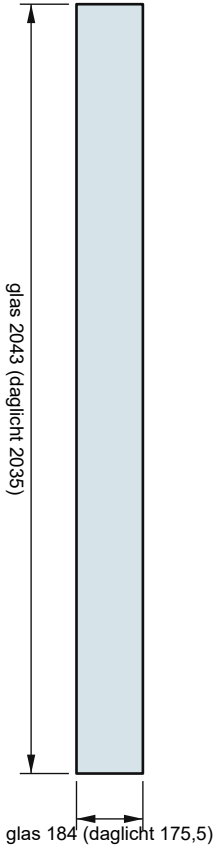

Waar het stuk zit

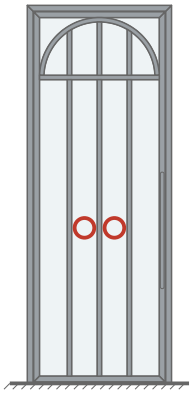

Opbouw (2:1)



gelaagd 44.2 helder

altijd veiligheidsglas (EN 12543 / EN 12150)

Bewerking en verbindingen


Bewerking: veiligheidsglas; glasmaat = daglicht + 4 rondom

Titel: **Pos 26: Ruit**			
Deur: Kathedraal · opening 1000 x 2600		Tekeningnummer: **TD-34-26**	
Maten en toleranties: mm · ISO 2768-m · eerste hoek	Opgesteld: Ian · laswerken	Uitgifte: 2026-11-10	Blad: 26 / 28


27 2 x Ruit met vorm (DXF)

gelaagd 44.2 helder · 168 x 304 · 0,75 kg/st

Aanzicht (1:5): daglicht, de ruit is 4 mm groter rondom

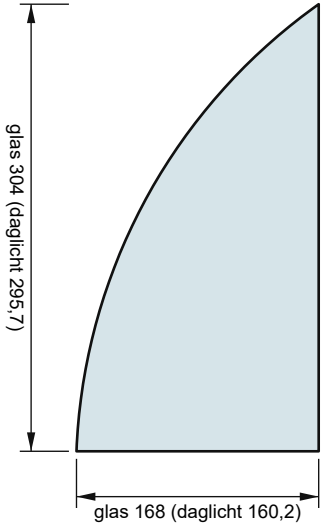

Waar het stuk zit

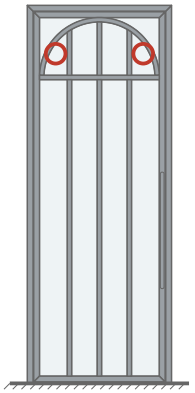

Opbouw (2:1)



gelaagd 44.2 helder

altijd veiligheidsglas (EN 12543 / EN 12150)

Bewerking en verbindingen


Bewerking: veiligheidsglas; snijden op de DXF (daglicht + 4 rondom)

Titel			
Pos 27: Ruit met vorm (DXF)			
Deur		Tekeningnummer	
Kathedraal · opening 1000 x 2600		**TD-34-27**	
Maten en toleranties	Opgesteld	Uitgifte	Blad
mm · ISO 2768-m · eerste hoek	Ian · laswerken	2026-11-10	27 / 28


28 2 x Ruit met vorm (DXF)

gelaagd 44.2 helder · 184 x 374 · 1,36 kg/st

Aanzicht (1:5): daglicht, de ruit is 4 mm groter rondom

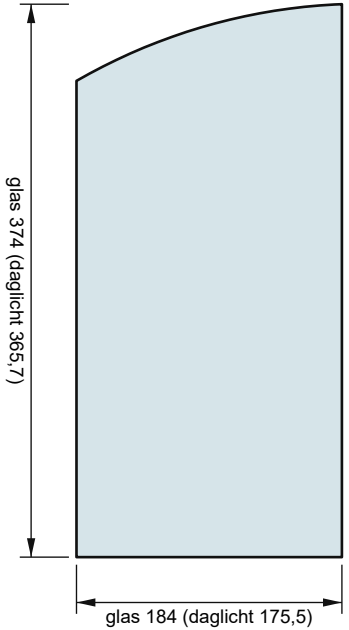

Waar het stuk zit

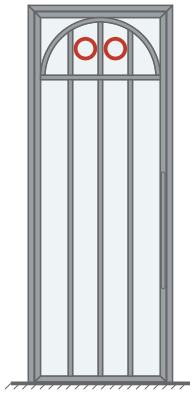

Opbouw (2:1)



gelaagd 44.2 helder

altijd veiligheidsglas (EN 12543 / EN 12150)

Bewerking en verbindingen

Bewerking: veiligheidsglas; snijden op de DXF (daglicht + 4 rondom)

Titel: **Pos 28: Ruit met vorm (DXF)**			
Deur: Kathedraal · opening 1000 x 2600		Tekeningnummer: **TD-34-28**	
Maten en toleranties: mm · ISO 2768-m · eerste hoek	Opgesteld: Ian · laswerken	Uitgifte: 2026-11-10	Blad: 28 / 28