

1 2 x Kozijn: stijl

S235, koker 40x40x2 · L = 2595 · zagen 90°/45° · 5,99 kg/st


Waar het stuk zit

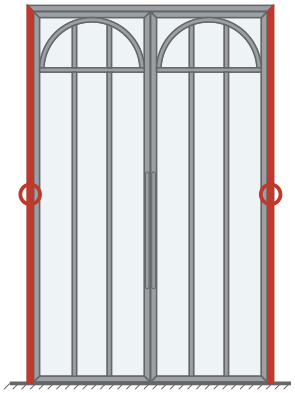

Aanzicht (1:20)

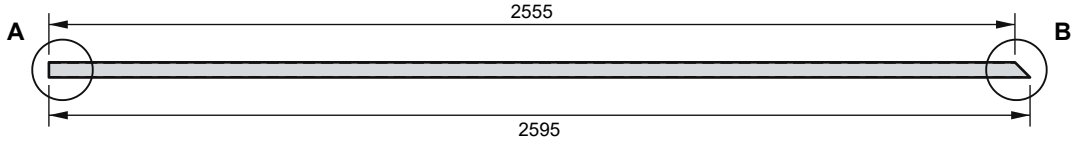


Detail A (1:1): linker uiteinde

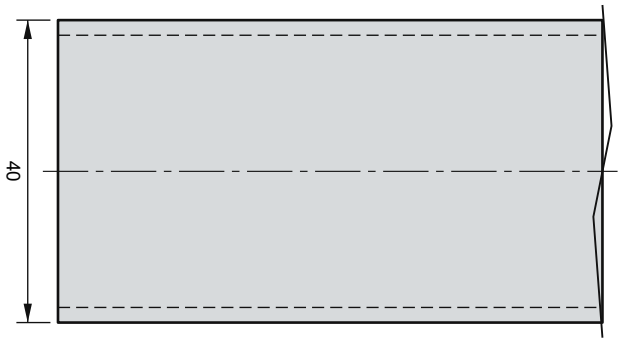


Recht afzagen (90°)

Detail B (1:1): rechter uiteinde

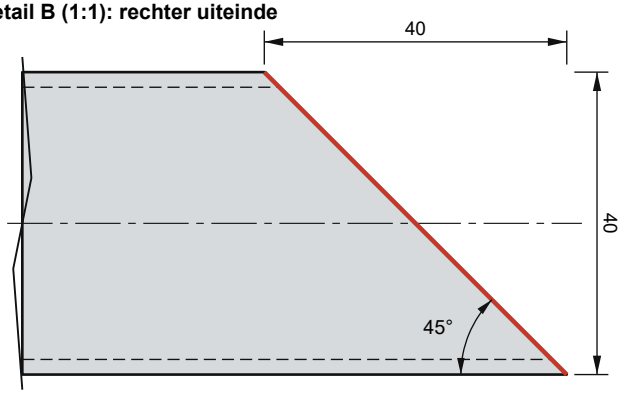

Verstek 45°: lange kant is 40 langer dan de korte

Doorsnede (arcering = materiaal)

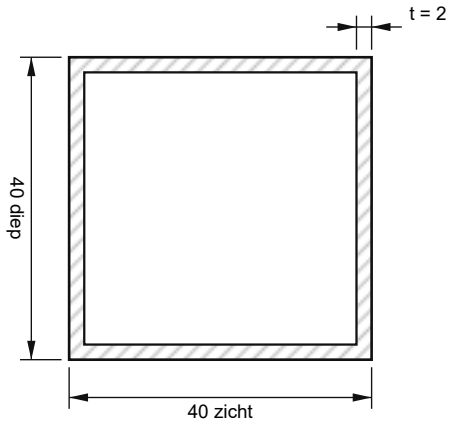

koker 40x40x2 (1:1)

boven = de kant met de greep

Bewerking en verbindingen

Bewerking: recht · verstek 45°


V1: 2 x verstek 45° met pos 2 (Kozijn: bovenregel)

Titel: **Pos 1: Kozijn: stijl**			
Deur: Dubbele kathedraal · opening 1700 x 2600		Tekeningnummer: **TD-89-01**	
Maten en toleranties: mm · ISO 2768-m · eerste hoek	Opgesteld: Ian · laswerken	Uitgifte: 2026-11-10	Blad: 1 / 26


2 1 x Kozijn: bovenregel

S235, koker 40x40x2 · L = 1690 · zagen 45°/45° · 3,9 kg/st


Waar het stuk zit

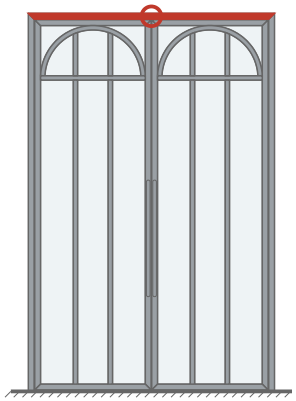

Aanzicht (1:10)

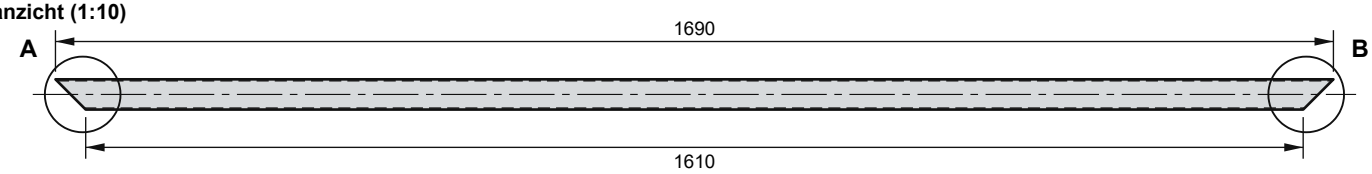


Detail A (1:1): linker uiteinde

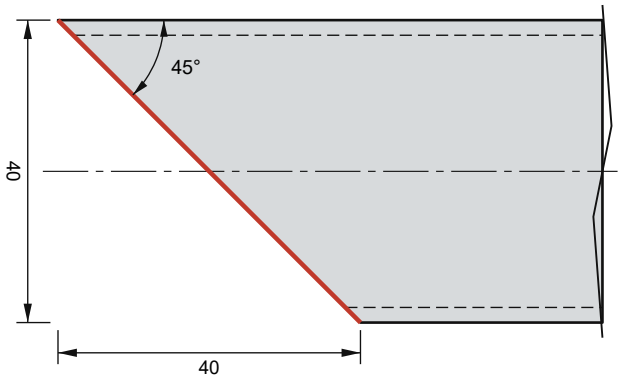


Verstek 45°: lange kant is 40 langer dan de korte

Detail B (1:1): rechter uiteinde

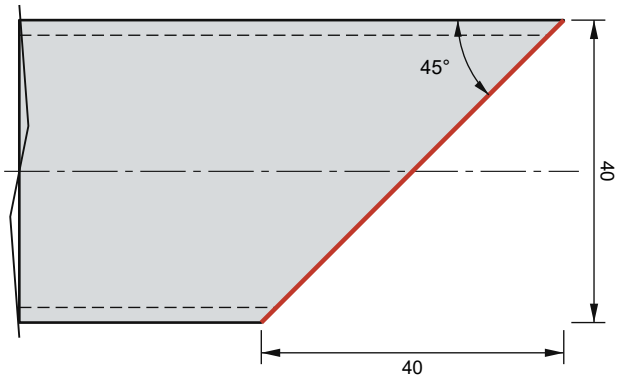

Verstek 45°: lange kant is 40 langer dan de korte

Doorsnede (arcering = materiaal)

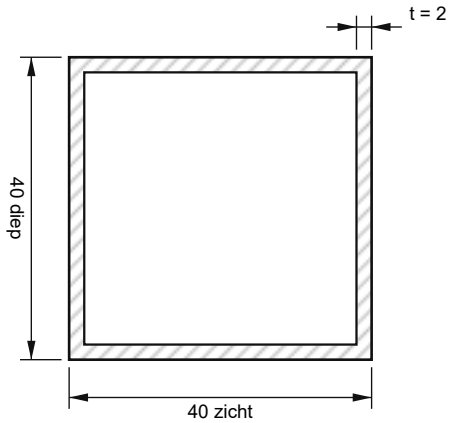

koker 40x40x2 (1:1)

boven = de kant met de greep

Bewerking en verbindingen

Bewerking: verstek 45° · verstek 45°

V1: 2 x verstek 45° met pos 1 (Kozijn: stijl)

Titel: **Pos 2: Kozijn: bovenregel**			
Deur: Dubbele kathedraal · opening 1700 x 2600		Tekeningnummer: **TD-89-02**	
Maten en toleranties: mm · ISO 2768-m · eerste hoek	Opgesteld: Ian · laswerken	Uitgifte: 2026-11-10	Blad: 2 / 26


3 4 x Kader: staander

S235, koker 40x40x2 · L = 2541 · zagen 45°/45° · 5,87 kg/st


Aanzicht (1:20)



Waar het stuk zit

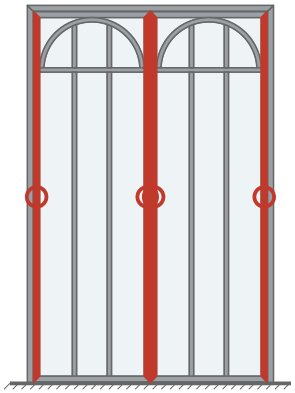


Detail A (1:1): linker uiteinde

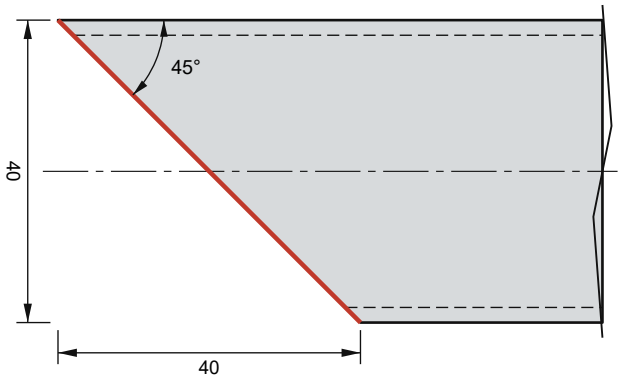


Verstek 45°: lange kant is 40 langer dan de korte

Detail B (1:1): rechter uiteinde

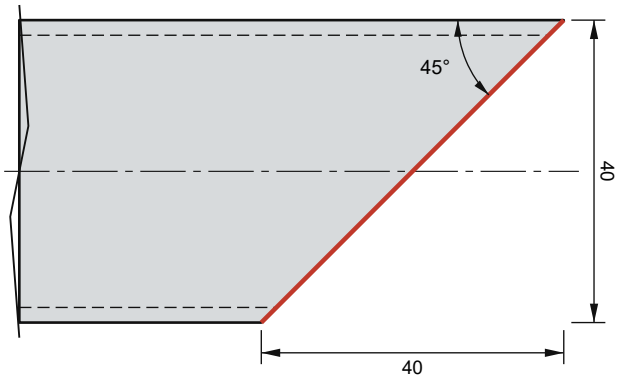

Verstek 45°: lange kant is 40 langer dan de korte

Doorsnede (arcering = materiaal)

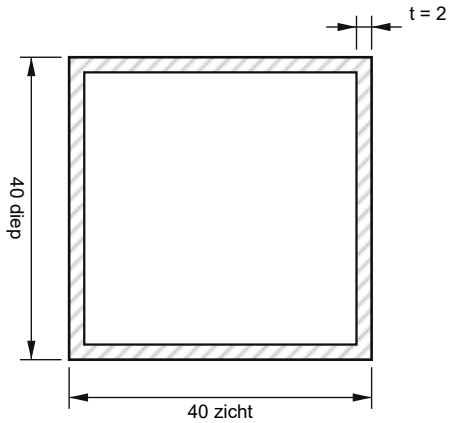

koker 40x40x2 (1:1)

boven = de kant met de greep

Bewerking en verbindingen


Bewerking: verstek 45° · verstek 45°
V2: 8 x verstek 45° met pos 4 (Kader: regel)
T1: 4 x t-verbinding (stomp) met pos 5 (Roede horizontaal: kern)

Titel: **Pos 3: Kader: staander**			
Deur: Dubbele kathedraal · opening 1700 x 2600		Tekeningnummer: **TD-89-03**	
Maten en toleranties: mm · ISO 2768-m · eerste hoek	Opgesteld: Ian · laswerken	Uitgifte: 2026-11-10	Blad: 3 / 26


4 x Kader: regel

S235, koker 40x40x2 · L = 799 · zagen 45°/45° · 1,85 kg/st


Aanzicht (1:5)

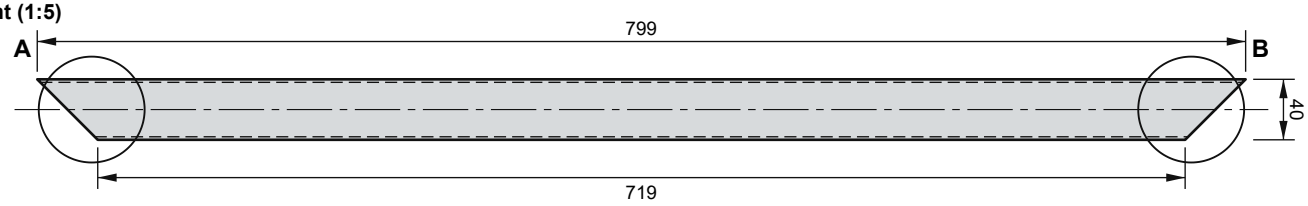

Waar het stuk zit

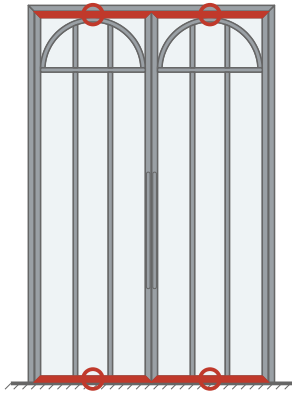


Detail A (1:1): linker uiteinde

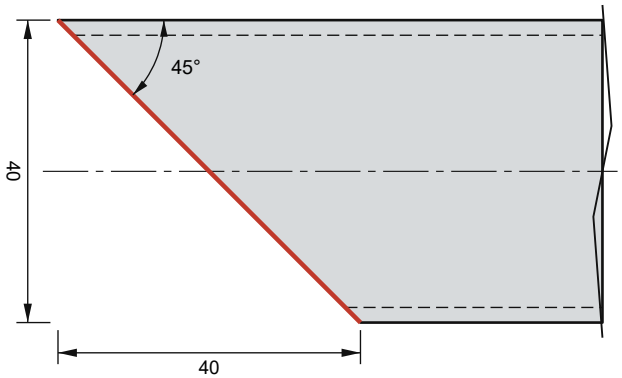


Verstek 45°: lange kant is 40 langer dan de korte

Detail B (1:1): rechter uiteinde

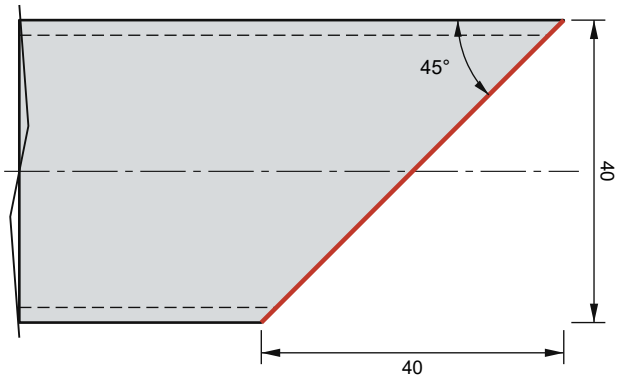

Verstek 45°: lange kant is 40 langer dan de korte

Doorsnede (arcering = materiaal)

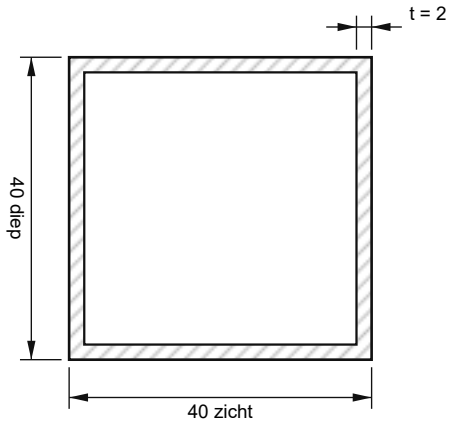

koker 40x40x2 (1:1)

boven = de kant met de greep

Bewerking en verbindingen

Bewerking: verstek 45° · verstek 45°
V2: 8 x verstek 45° met pos 3 (Kader: staander)
T2: 4 x t-verbinding (stomp) met pos 7 (Roede verticaal: kern)

Titel: **Pos 4: Kader: regel**			
Deur: Dubbele kathedraal · opening 1700 x 2600		Tekeningnummer: **TD-89-04**	
Maten en toleranties: mm · ISO 2768-m · eerste hoek	Opgesteld: Ian · laswerken	Uitgifte: 2026-11-10	Blad: 4 / 26

5


2 x Roede horizontaal: kern

S235, platstaal 20x10 · L = 719 · zagen 90°/90° · 1,13 kg/st


Aanzicht (1:5)



Waar het stuk zit

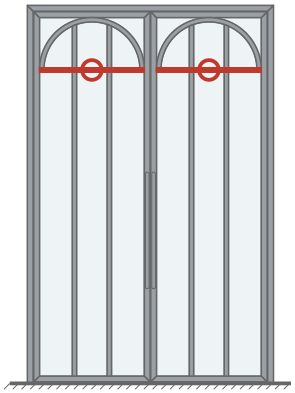


Detail A (2:1): linker uiteinde

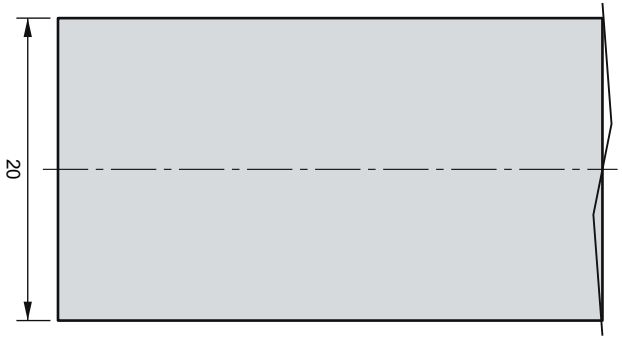


Recht afzagen (90°)

Detail B (2:1): rechter uiteinde

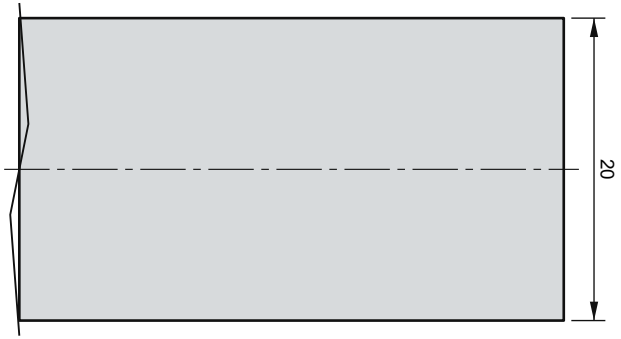

Recht afzagen (90°)

Doorsnede (arcering = materiaal)

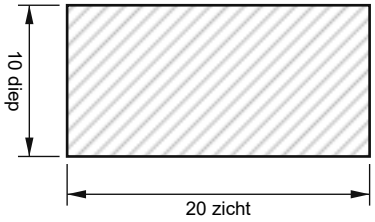

platstaal 20x10 (2:1)

boven = de kant met de greep

Bewerking en verbindingen


Bewerking: recht · recht; M4 om de 250 aan de achterkant
T1: 4 x t-verbinding (stomp) met pos 3 (Kader: staander)
T3: 4 x t-verbinding (stomp) met pos 7 (Roede verticaal: kern)
S1: 4 x schuin tegen de boog met pos 9 (Roede tot in de boog: kern)
B1: 4 x boog op kalf, poot of kader met pos 17 (Boogroede: kern)

Titel: **Pos 5: Roede horizontaal: kern**			
Deur: Dubbele kathedraal · opening 1700 x 2600		Tekeningnummer: **TD-89-05**	
Maten en toleranties: mm · ISO 2768-m · eerste hoek	Opgesteld: Ian · laswerken	Uitgifte: 2026-11-10	Blad: 5 / 26


6 4 x Roede horizontaal: lat voor en achter

S235, platstaal 30x3 · L = 719 · zagen 90°/90° · 0,51 kg/st


Aanzicht (1:5)

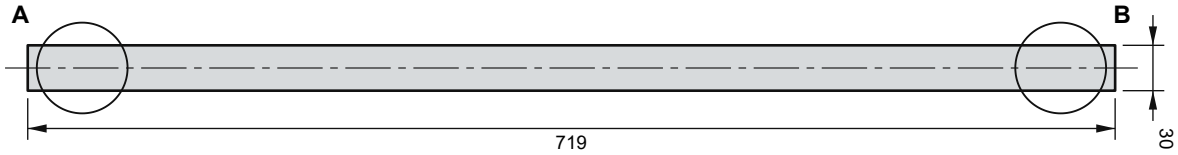

Waar het stuk zit

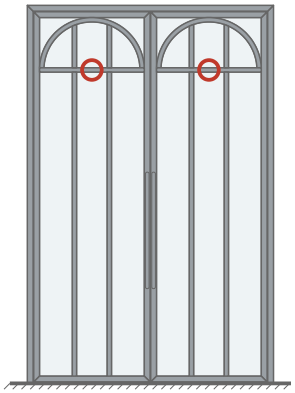


Detail A (1:1): linker uiteinde

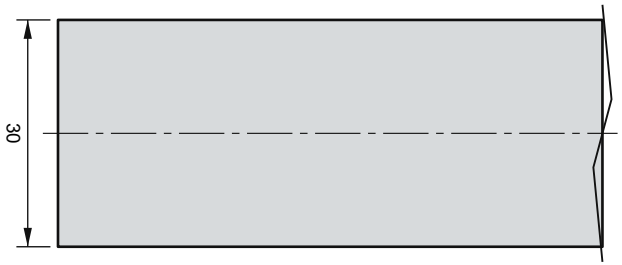


Recht afzagen (90°)

Detail B (1:1): rechter uiteinde

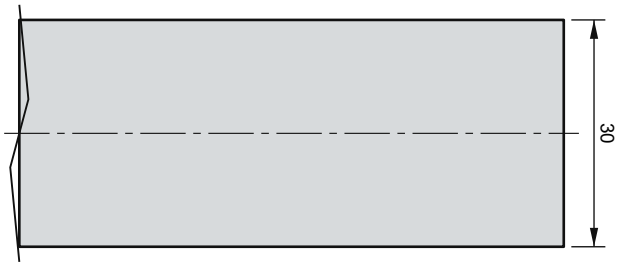

Recht afzagen (90°)

Doorsnede (arcering = materiaal)

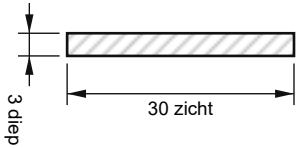

platstaal 30x3 (1:1)

boven = de kant met de greep

Bewerking en verbindingen

Bewerking: recht · recht; voor gelast, achter geschroefd


Hechten om de 150 en lassen (voor) of M4 verzonken om de 250 (achter): zie de werkwijze

Titel: **Pos 6: Roede horizontaal: lat voor en achter**			
Deur: Dubbele kathedraal · opening 1700 x 2600		Tekeningnummer: **TD-89-06**	
Maten en toleranties: mm · ISO 2768-m · eerste hoek	Opgesteld: Ian · laswerken	Uitgifte: 2026-11-10	Blad: 6 / 26

7 4 x Roede verticaal: kern

S235, platstaal 20x10 · L = 2087 · zagen 90°/90° · 3,28 kg/st


Waar het stuk zit

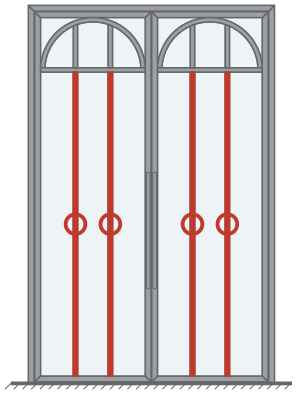

Aanzicht (1:20)




Detail A (2:1): linker uiteinde

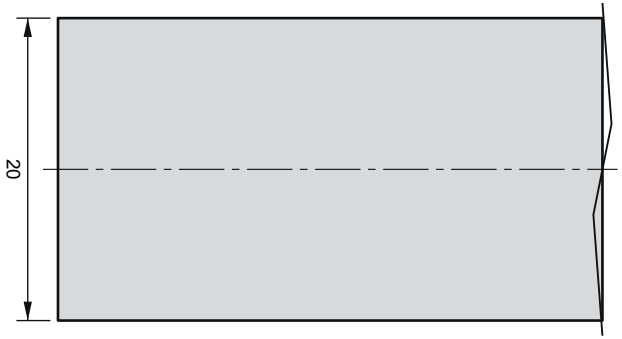


Recht afzagen (90°)

Detail B (2:1): rechter uiteinde

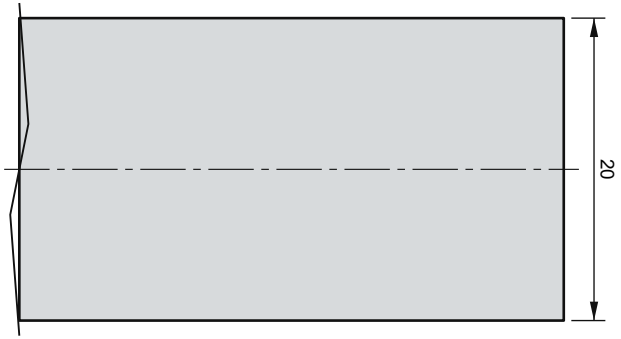

Recht afzagen (90°)

Doorsnede (arcering = materiaal)

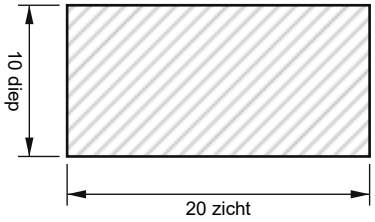

platstaal 20x10 (2:1)

boven = de kant met de greep

Bewerking en verbindingen

Bewerking: recht · recht; M4 om de 250 aan de achterkant
T2: 4 x t-verbinding (stomp) met pos 4 (Kader: regel)
T3: 4 x t-verbinding (stomp) met pos 5 (Roede horizontaal: kern)

Titel: **Pos 7: Roede verticaal: kern**			
Deur: Dubbele kathedraal · opening 1700 x 2600		Tekeningnummer: **TD-89-07**	
Maten en toleranties: mm · ISO 2768-m · eerste hoek	Opgesteld: Ian · laswerken	Uitgifte: 2026-11-10	Blad: 7 / 26

8 x Roede verticaal: lat voor en achter


8

S235, platstaal 30x3 · L = 2087 · zagen 90°/90° · 1,48 kg/st


Aanzicht (1:20)



Waar het stuk zit

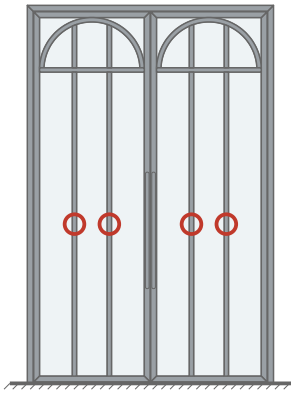


Detail A (1:1): linker uiteinde

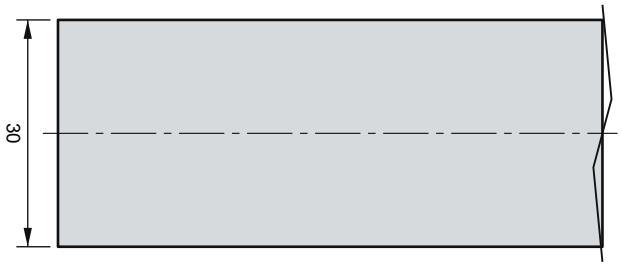


Recht afzagen (90°)

Detail B (1:1): rechter uiteinde

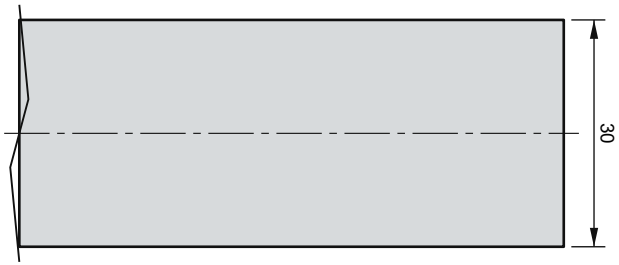

Recht afzagen (90°)

Doorsnede (arcering = materiaal)

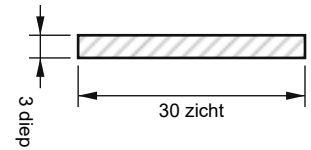

platstaal 30x3 (1:1)

boven = de kant met de greep

Bewerking en verbindingen

Bewerking: recht · recht; voor gelast, achter geschroefd


Hechten om de 150 en lassen (voor) of M4 verzonken om de 250 (achter): zie de werkwijze

Titel: **Pos 8: Roede verticaal: lat voor en achter**			
Deur: Dubbele kathedraal · opening 1700 x 2600		Tekeningnummer: **TD-89-08**	
Maten en toleranties: mm · ISO 2768-m · eerste hoek	Opgesteld: Ian · laswerken	Uitgifte: 2026-11-10	Blad: 8 / 26


9 4 x Roede tot in de boog: kern

S235, platstaal 20x10 · L = 296 · zagen 90°/69° · 0,46 kg/st


Waar het stuk zit

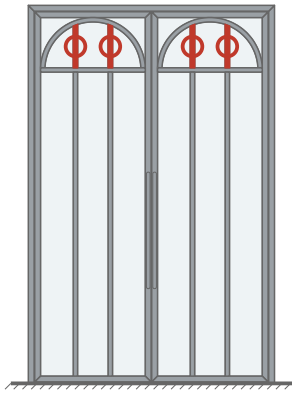

Aanzicht (1:2)

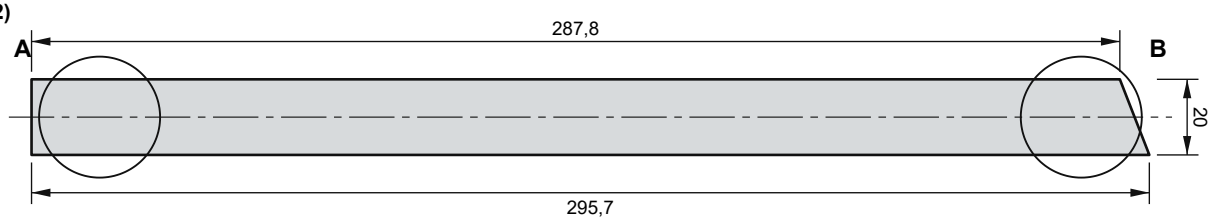


Detail A (2:1): linker uiteinde

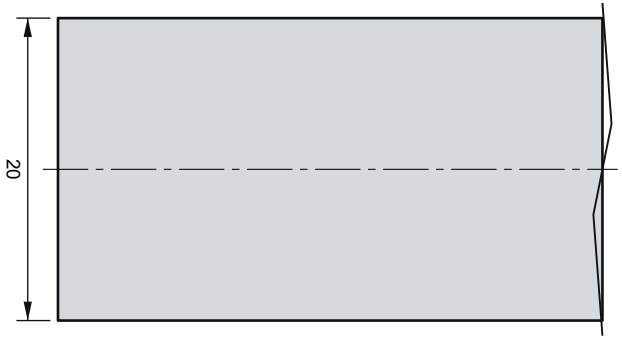


Recht afzagen (90°)

Detail B (2:1): rechter uiteinde

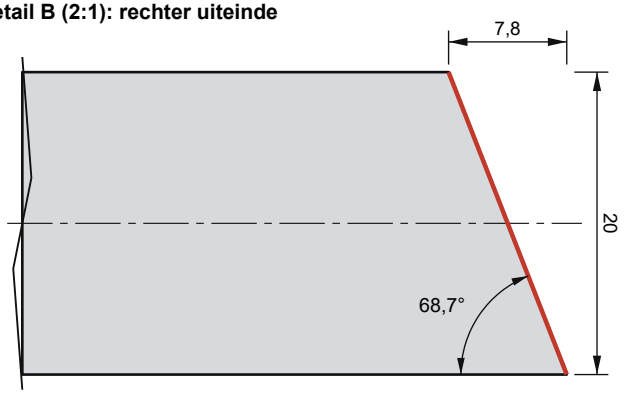

Schuin 68,7°: lange kant is 7,8 langer dan de korte

Doorsnede (arcering = materiaal)

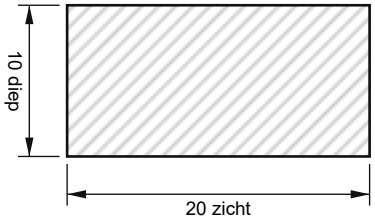

platstaal 20x10 (2:1)

boven = de kant met de greep

Bewerking en verbindingen


Bewerking: recht · schuin 21° (volgens de boog); M4 om de 250 aan de achterkant
S1: 4 x schuin tegen de boog met pos 5 (Roede horizontaal: kern)
S2: 4 x schuin tegen de boog met pos 17 (Boogroede: kern)

Titel: **Pos 9: Roede tot in de boog: kern**			
Deur: Dubbele kathedraal · opening 1700 x 2600		Tekeningnummer: **TD-89-09**	
Maten en toleranties: mm · ISO 2768-m · eerste hoek	Opgesteld: Ian · laswerken	Uitgifte: 2026-11-10	Blad: 9 / 26


10 8 x Roede tot in de boog: lat voor en achter

S235, platstaal 30x3 · L = 297 · zagen 90°/69° · 0,21 kg/st


Waar het stuk zit

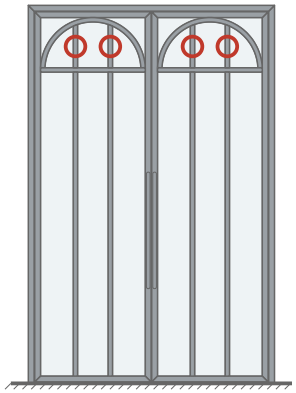

Aanzicht (1:2)

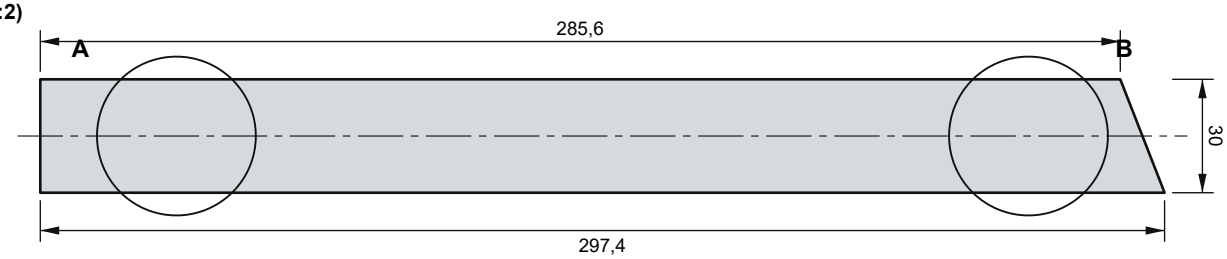


Detail A (1:1): linker uiteinde

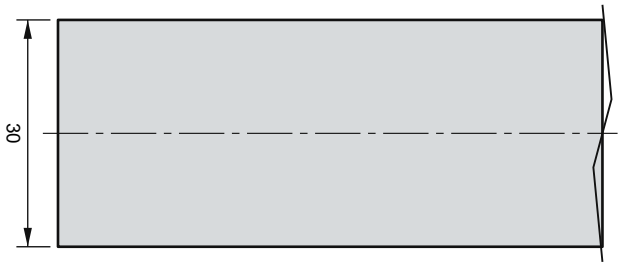


Recht afzagen (90°)

Detail B (1:1): rechter uiteinde

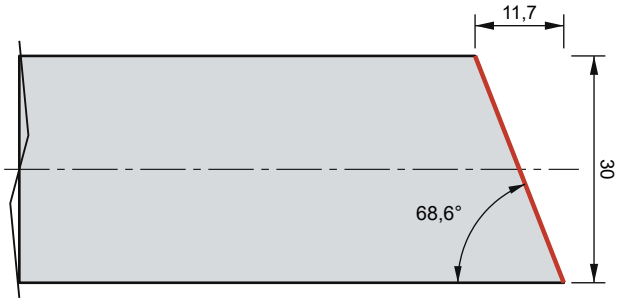

Schuin 68,6°: lange kant is 11,7 langer dan de korte

Doorsnede (arcering = materiaal)

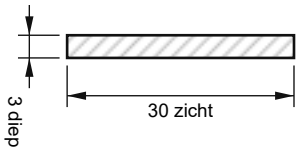

platstaal 30x3 (1:1)

boven = de kant met de greep

Bewerking en verbindingen

Bewerking: recht · schuin 21° (volgens de boog); voor gelast, achter geschroefd


Hechten om de 150 en lassen (voor) of M4 verzonken om de 250 (achter): zie de werkwijze

Titel: **Pos 10: Roede tot in de boog: lat voor en achter**			
Deur: Dubbele kathedraal · opening 1700 x 2600		Tekeningnummer: **TD-89-10**	
Maten en toleranties: mm · ISO 2768-m · eerste hoek	Opgesteld: Ian · laswerken	Uitgifte: 2026-11-10	Blad: 10 / 26


11 8 x Glaslat

S235, platstaal 15x4 · L = 360 · 0,17 kg/st


Aanzicht (1:2)

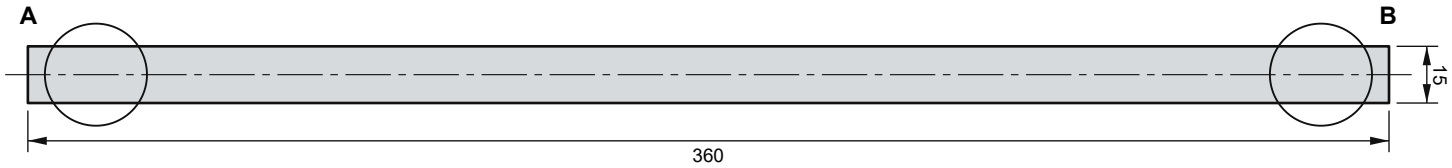

Waar het stuk zit

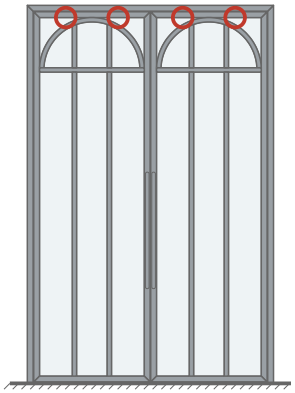


Detail A (2:1): linker uiteinde

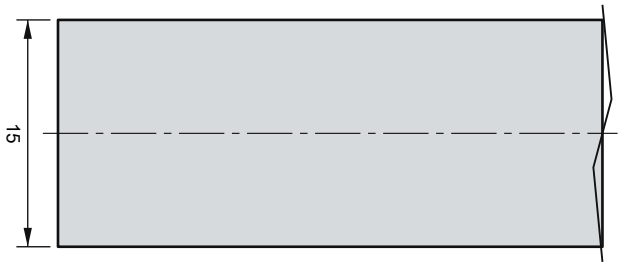

Recht afzagen (90°)

Detail B (2:1): rechter uiteinde

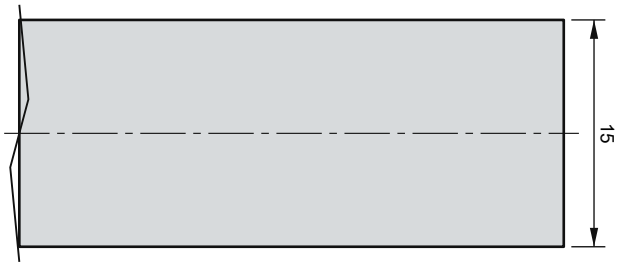

Recht afzagen (90°)

Doorsnede (arcering = materiaal)



platstaal 15x4 (2:1)

boven = de kant met de greep

Bewerking en verbindingen

Bewerking: recht; voor gelast, achter geschroefd (M4 verzonken om de 250)


Hechten om de 150 en lassen (voor) of M4 verzonken om de 250 (achter): zie de werkwijze

Titel: **Pos 11: Glaslat**			
Deur: Dubbele kathedraal · opening 1700 x 2600		Tekeningnummer: **TD-89-11**	
Maten en toleranties: mm · ISO 2768-m · eerste hoek	Opgesteld: Ian · laswerken	Uitgifte: 2026-11-10	Blad: 11 / 26


12 8 x Glaslat

S235, platstaal 15x4 · L = 345 · 0,16 kg/st


Aanzicht (1:2)

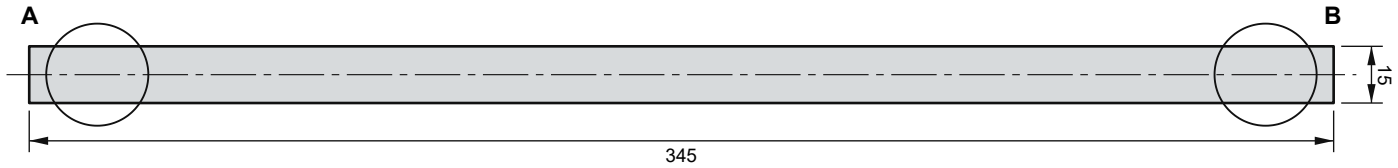

Waar het stuk zit

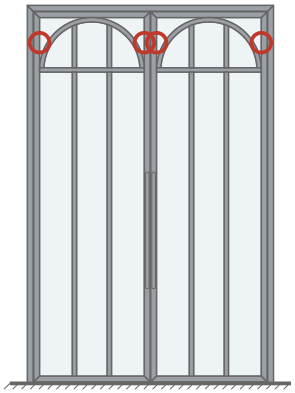


Detail A (2:1): linker uiteinde

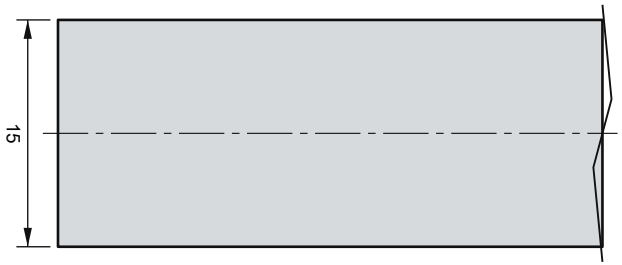

Recht afzagen (90°)

Detail B (2:1): rechter uiteinde

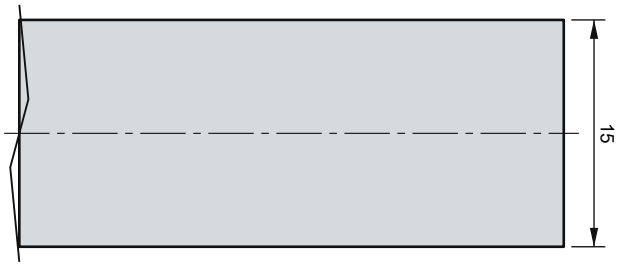

Recht afzagen (90°)

Doorsnede (arcering = materiaal)



platstaal 15x4 (2:1)

boven = de kant met de greep

Bewerking en verbindingen


Bewerking: recht; voor gelast, achter geschroefd (M4 verzonken om de 250)
Hechten om de 150 en lassen (voor) of M4 verzonken om de 250 (achter): zie de werkwijze

Titel: **Pos 12: Glaslat**			
Deur: Dubbele kathedraal · opening 1700 x 2600		Tekeningnummer: **TD-89-12**	
Maten en toleranties: mm · ISO 2768-m · eerste hoek	Opgesteld: Ian · laswerken	Uitgifte: 2026-11-10	Blad: 12 / 26


13 8 x Glaslat

S235, platstaal 15x4 · L = 225 · 0,11 kg/st


Aanzicht (1:2)

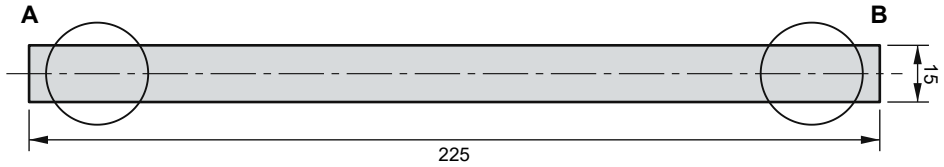

Waar het stuk zit

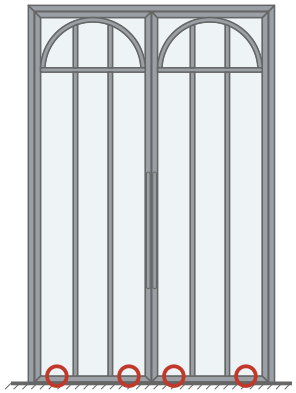


Detail A (2:1): linker uiteinde

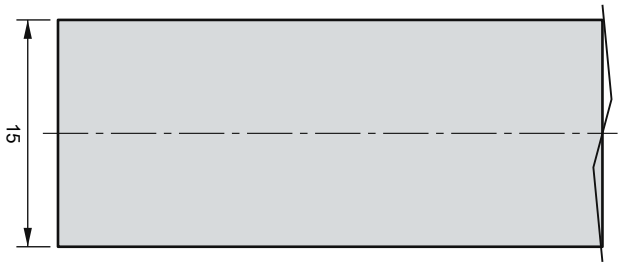

Recht afzagen (90°)

Detail B (2:1): rechter uiteinde

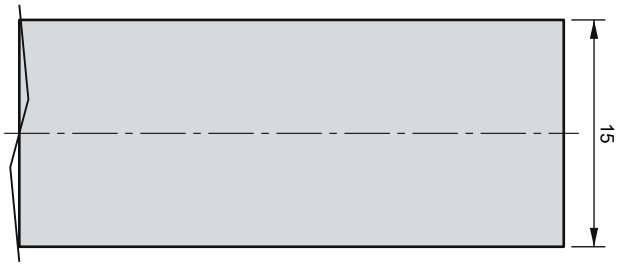

Recht afzagen (90°)

Doorsnede (arcering = materiaal)



platstaal 15x4 (2:1)

boven = de kant met de greep

Bewerking en verbindingen

Bewerking: recht; voor gelast, achter geschroefd (M4 verzonken om de 250)
Hechten om de 150 en lassen (voor) of M4 verzonken om de 250 (achter): zie de werkwijze

Titel: **Pos 13: Glaslat**			
Deur: Dubbele kathedraal · opening 1700 x 2600		Tekeningnummer: **TD-89-13**	
Maten en toleranties: mm · ISO 2768-m · eerste hoek	Opgesteld: Ian · laswerken	Uitgifte: 2026-11-10	Blad: 13 / 26


14 8 x Glaslat

S235, platstaal 15x4 · L = 2087 · 0,98 kg/st


Aanzicht (1:20)



Waar het stuk zit

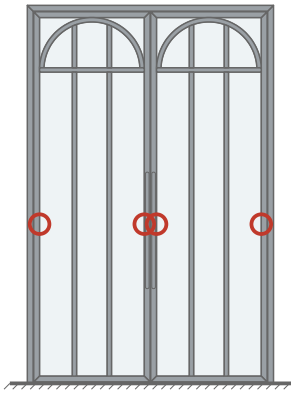


Detail A (2:1): linker uiteinde

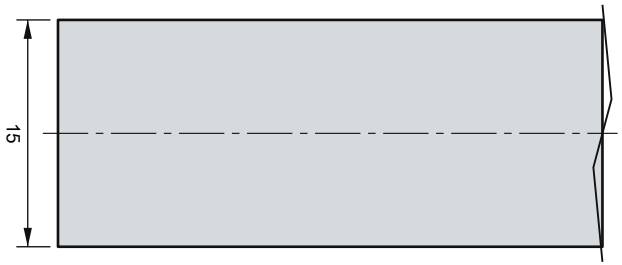

Recht afzagen (90°)

Detail B (2:1): rechter uiteinde

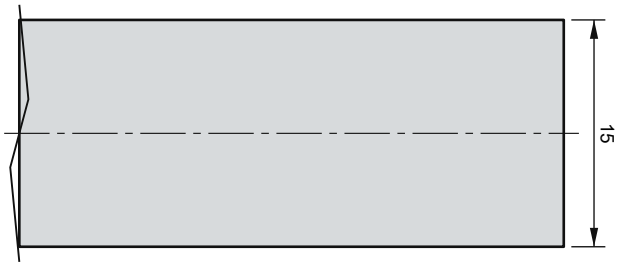

Recht afzagen (90°)

Doorsnede (arcering = materiaal)



platstaal 15x4 (2:1)

boven = de kant met de greep

Bewerking en verbindingen


Bewerking: recht; voor gelast, achter geschroefd (M4 verzonken om de 250)
Hechten om de 150 en lassen (voor) of M4 verzonken om de 250 (achter): zie de werkwijze

Titel: **Pos 14: Glaslat**			
Deur: Dubbele kathedraal · opening 1700 x 2600		Tekeningnummer: **TD-89-14**	
Maten en toleranties: mm · ISO 2768-m · eerste hoek	Opgesteld: Ian · laswerken	Uitgifte: 2026-11-10	Blad: 14 / 26


15 4 x Glaslat

S235, platstaal 15x4 · L = 210 · 0,1 kg/st


Aanzicht (1:2)

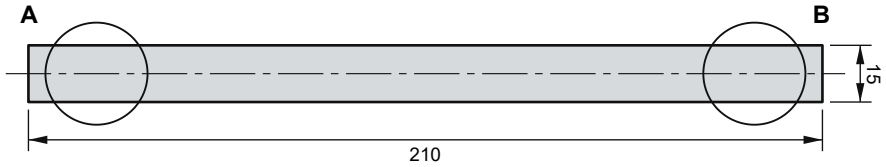

Waar het stuk zit

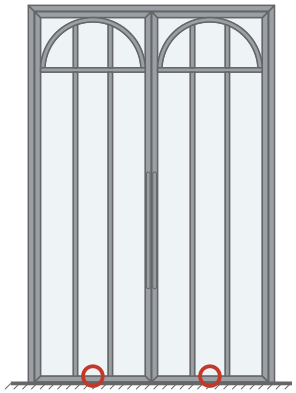


Detail A (2:1): linker uiteinde

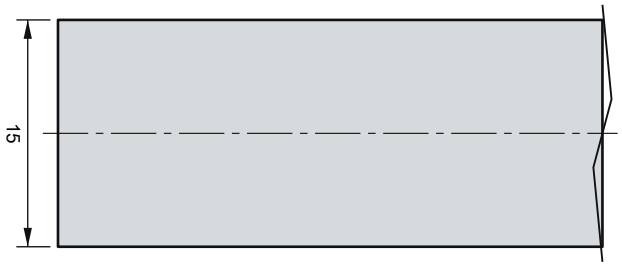

Recht afzagen (90°)

Detail B (2:1): rechter uiteinde

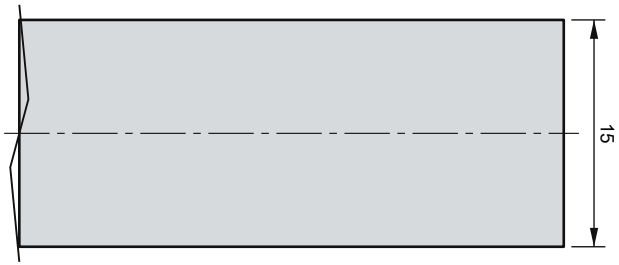

Recht afzagen (90°)

Doorsnede (arcering = materiaal)



platstaal 15x4 (2:1)

boven = de kant met de greep

Bewerking en verbindingen

Bewerking: recht; voor gelast, achter geschroefd (M4 verzonken om de 250)


Hechten om de 150 en lassen (voor) of M4 verzonken om de 250 (achter): zie de werkwijze

Titel: **Pos 15: Glaslat**			
Deur: Dubbele kathedraal · opening 1700 x 2600		Tekeningnummer: **TD-89-15**	
Maten en toleranties: mm · ISO 2768-m · eerste hoek	Opgesteld: Ian · laswerken	Uitgifte: 2026-11-10	Blad: 15 / 26


16 4 x Greep (voor en achter)

S235, rond Ø25 · L = 800 · 3,08 kg/st


Waar het stuk zit

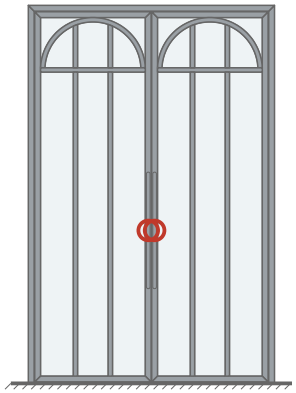

Aanzicht (1:5)

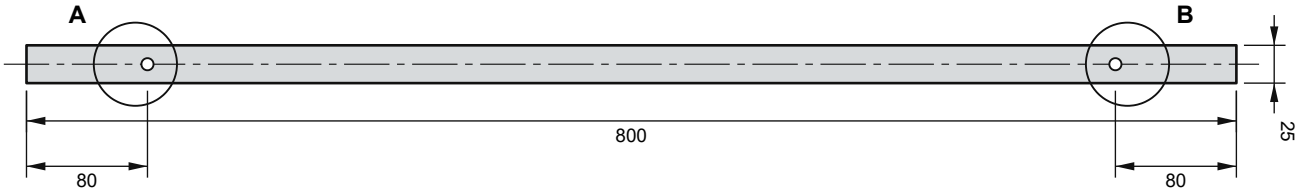


Detail A (1:2): linker uiteinde

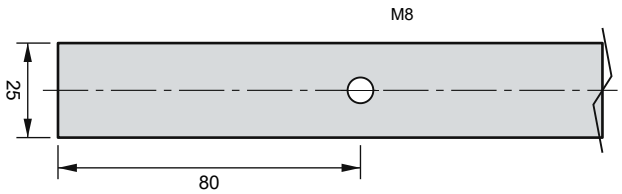


Recht afzagen (90°)

Detail B (1:2): rechter uiteinde

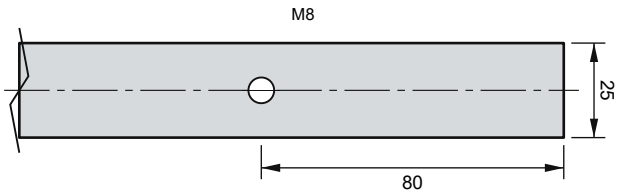

Recht afzagen (90°)

Doorsnede (arcering = materiaal)

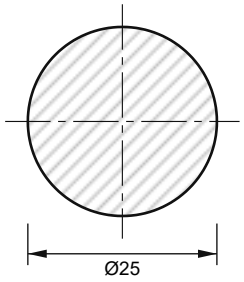

rond Ø25 (1:1)

Bewerking en verbindingen


Bewerking: uiteinden rond slijpen; 2 x M8 op 80 van de uiteinden

Titel: **Pos 16: Greep (voor en achter)**			
Deur: Dubbele kathedraal · opening 1700 x 2600		Tekeningnummer: **TD-89-16**	
Maten en toleranties: mm · ISO 2768-m · eerste hoek	Opgesteld: Ian · laswerken	Uitgifte: 2026-11-10	Blad: 16 / 26


17 2 x Boogroede: kern

S235, plaat 10 mm · R 344.5 x 20, 175° · 1,65 kg/st


Aanzicht (1:5), lasergesneden uit plaat 10 mm

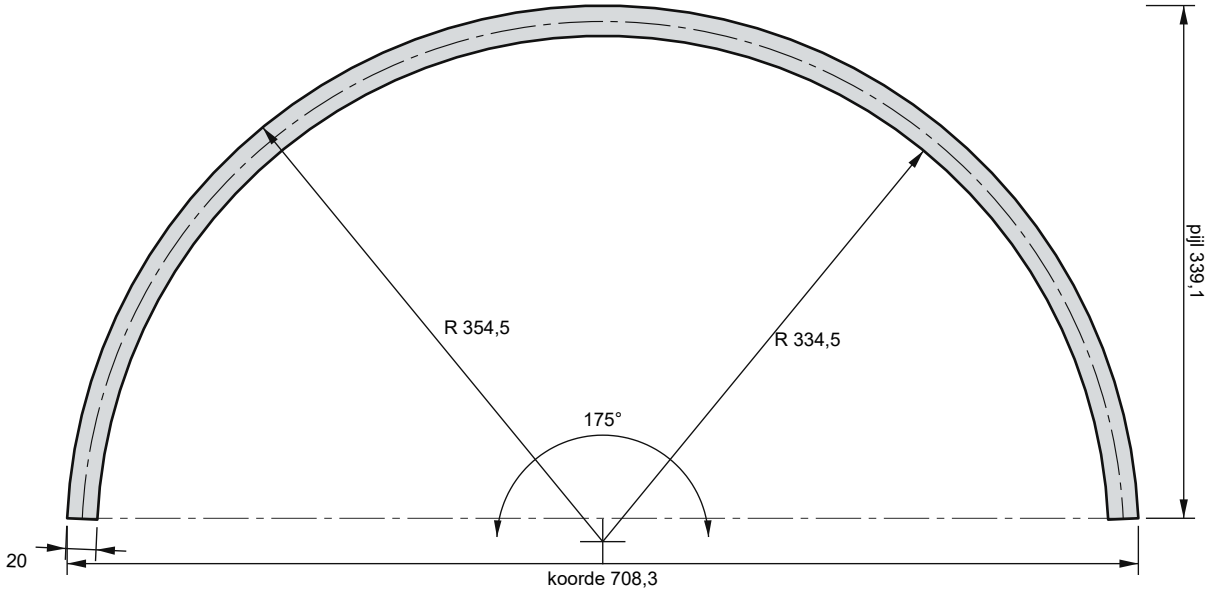

Waar het stuk zit

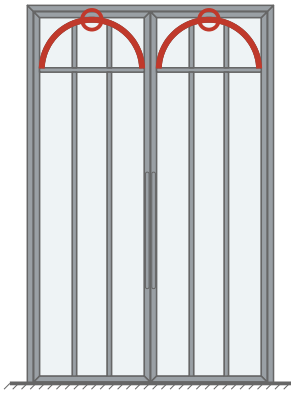

Doorsnede (lagen)

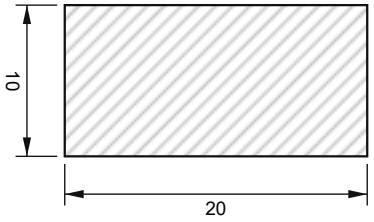

2:1 · één plaat

Bewerking en verbindingen


Bewerking: op de mal 1:1 leggen en hechten
S2: 4 x schuin tegen de boog met pos 9 (Roede tot in de boog: kern)
B1: 4 x boog op kalf, poot of kader met pos 5 (Roede horizontaal: kern)

Titel: **Pos 17: Boogroede: kern**			
Deur: Dubbele kathedraal · opening 1700 x 2600		Tekeningnummer: **TD-89-17**	
Maten en toleranties: mm · ISO 2768-m · eerste hoek	Opgesteld: Ian · laswerken	Uitgifte: 2026-11-10	Blad: 17 / 26


18 4 x Boogroede: lat voor en achter

S235, plaat 3 mm · R 344.5 x 30, 175° · 0,74 kg/st


Aanzicht (1:5), lasergesneden uit plaat 3 mm

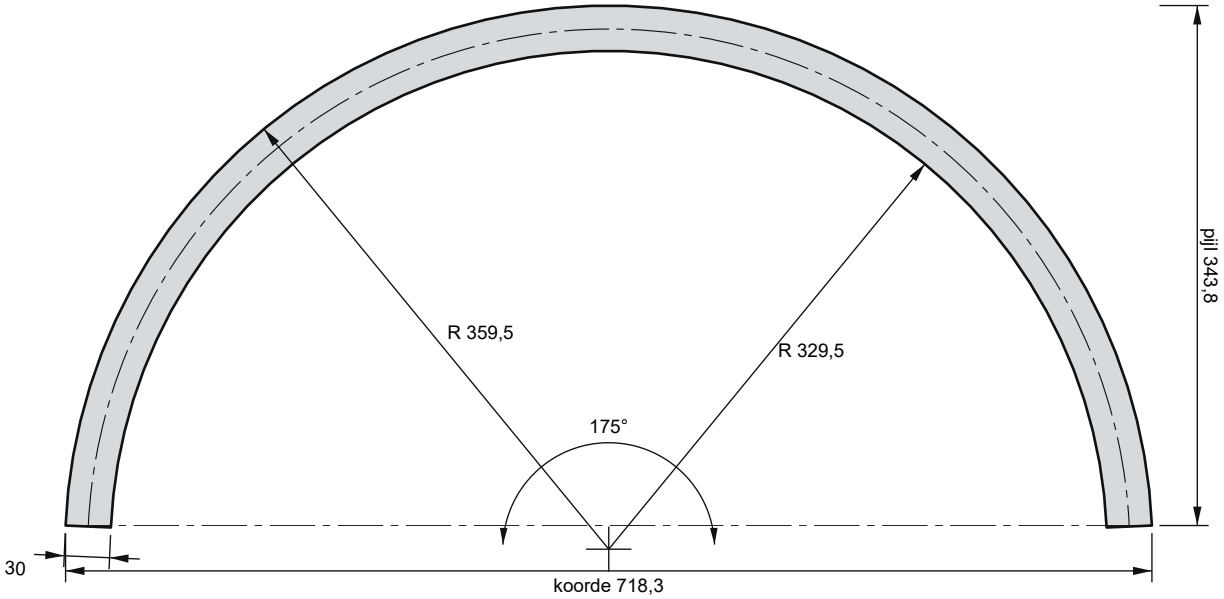

Waar het stuk zit

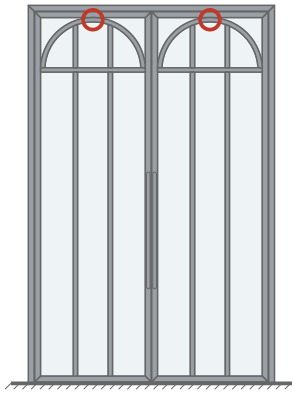

Doorsnede (lagen)

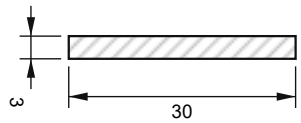

1:1 · één plaat

Bewerking en verbindingen


Bewerking: voor gelast, achter geschroefd

Titel: **Pos 18: Boogroede: lat voor en achter**			
Deur: Dubbele kathedraal · opening 1700 x 2600		Tekeningnummer: **TD-89-18**	
Maten en toleranties: mm · ISO 2768-m · eerste hoek	Opgesteld: Ian · laswerken	Uitgifte: 2026-11-10	Blad: 18 / 26


19 2 x Taatsplaat onder

S235, plaat 8 mm · 36 x 220 · 0,5 kg/st

Aanzicht (1:2)

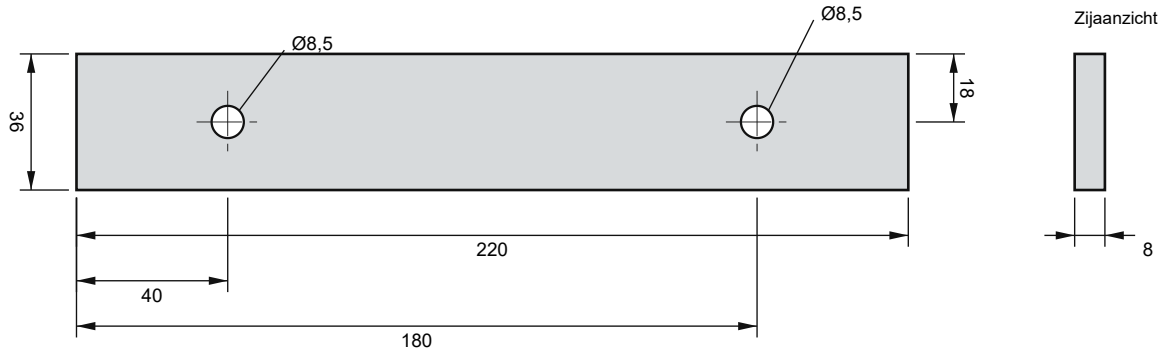

Waar het stuk zit

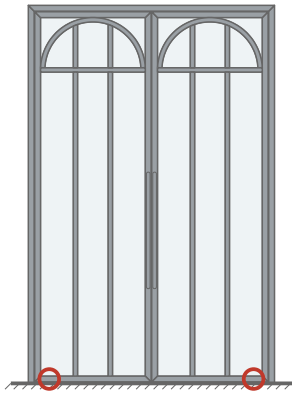

Plaat

S235, plaat 8 mm

36 x 220 x 8 mm

Lasersnijden op de DXF; braam eraf

Bewerking en verbindingen


Bewerking: 2 x Ø8,5 voor het scharnier; in de onderregel gelast

Titel: **Pos 19: Taatsplaat onder**			
Deur: Dubbele kathedraal · opening 1700 x 2600		Tekeningnummer: **TD-89-19**	
Maten en toleranties: mm · ISO 2768-m · eerste hoek	Opgesteld: Ian · laswerken	Uitgifte: 2026-11-10	Blad: 19 / 26

20 2 x Taatsplaat boven

S235, plaat 8 mm · 36 x 140 · 0,32 kg/st

Aanzicht (1:1)

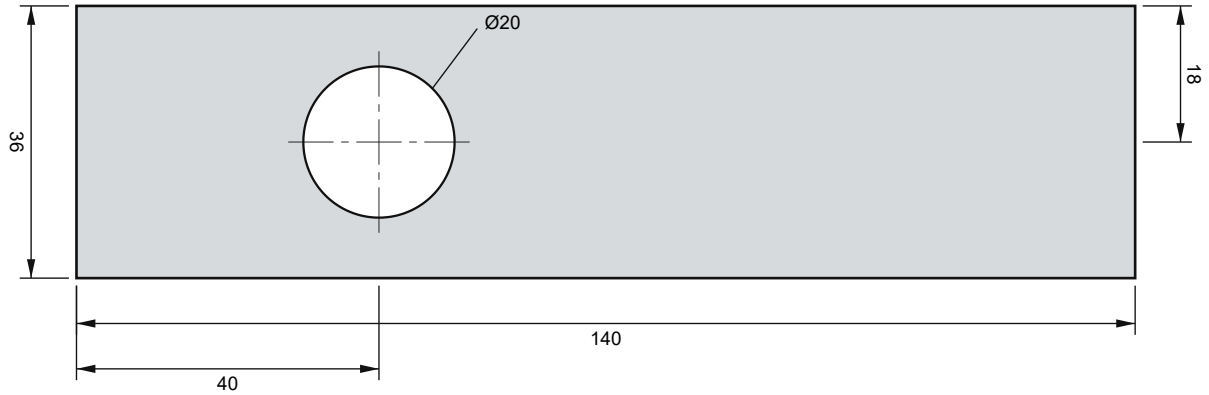

Zijaanzicht




Plaat

S235, plaat 8 mm

36 x 140 x 8 mm

Lasersnijden op de DXF; braam eraf

Waar het stuk zit

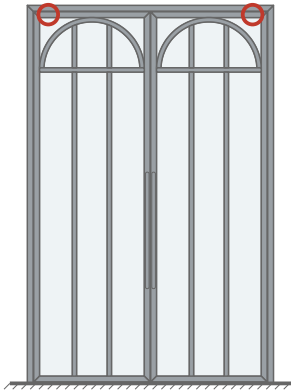

Bewerking en verbindingen


Bewerking: Ø20 voor de bovenpen; in de bovenregel gelast

Titel: **Pos 20: Taatsplaat boven**			
Deur: Dubbele kathedraal · opening 1700 x 2600		Tekeningnummer: **TD-89-20**	
Maten en toleranties: mm · ISO 2768-m · eerste hoek	Opgesteld: Ian · laswerken	Uitgifte: 2026-11-10	Blad: 20 / 26


21 4 x Greephouder

S235, plaat 10 mm · 25 x 40 · 0,08 kg/st


Aanzicht (2:1)

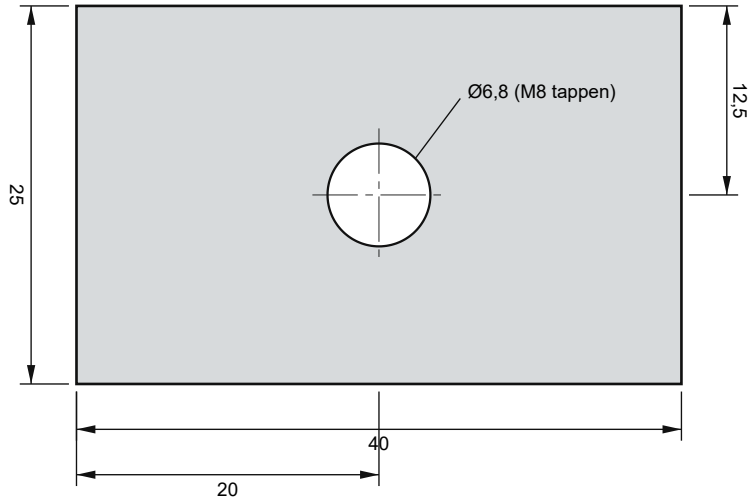

Zijaanzicht

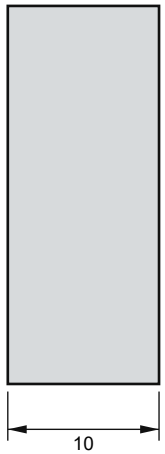

Waar het stuk zit

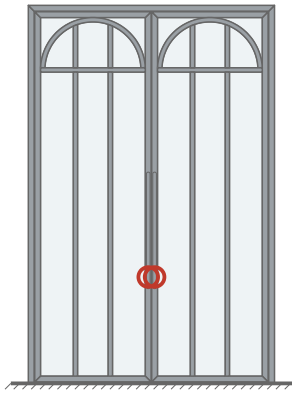

Plaat

S235, plaat 10 mm

25 x 40 x 10 mm

Lasersnijden op de DXF; braam eraf

Bewerking en verbindingen


Bewerking: M8 tappen (boor Ø6,8); op de staander gelast

Titel: **Pos 21: Greephouder**			
Deur: Dubbele kathedraal · opening 1700 x 2600		Tekeningnummer: **TD-89-21**	
Maten en toleranties: mm · ISO 2768-m · eerste hoek	Opgesteld: Ian · laswerken	Uitgifte: 2026-11-10	Blad: 21 / 26


22 4 x Ruit met vorm (DXF)

gelaagd 44.2 helder · 368 x 353 · 0,7 kg/st

Aanzicht (1:5): daglicht, de ruit is 4 mm groter rondom

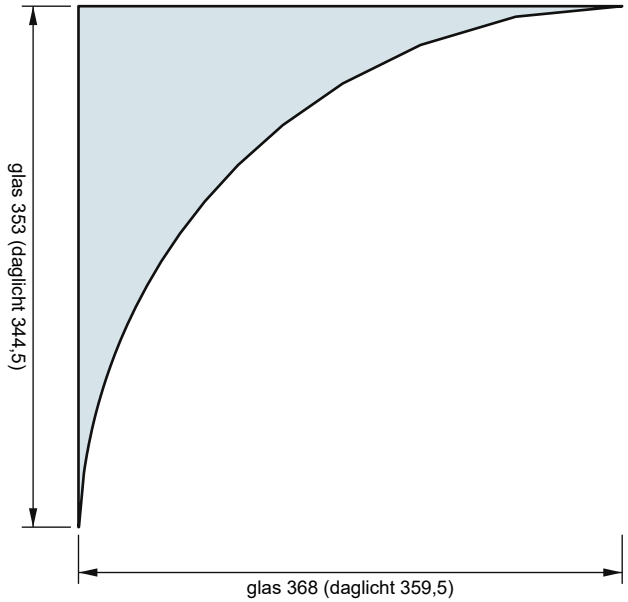

Waar het stuk zit

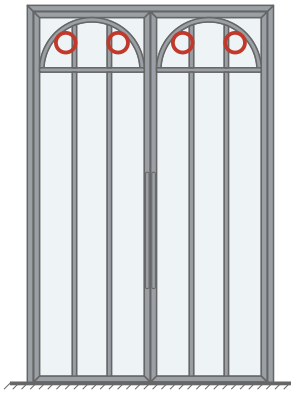

Opbouw (2:1)



gelaagd 44.2 helder

altijd veiligheidsglas (EN 12543 / EN 12150)

Bewerking en verbindingen


Bewerking: veiligheidsglas; snijden op de DXF (daglicht + 4 rondom)

Titel			
Pos 22: Ruit met vorm (DXF)			
Deur		Tekeningnummer	
Dubbele kathedraal · opening 1700 x 2600		**TD-89-22**	
Maten en toleranties	Opgesteld	Uitgifte	Blad
mm · ISO 2768-m · eerste hoek	Ian · laswerken	2026-11-10	22 / 26


23 4 x Ruit

gelaagd 44.2 helder · 233 x 2095 · 10,13 kg/st

Aanzicht (1:20): daglicht, de ruit is 4 mm groter rondom

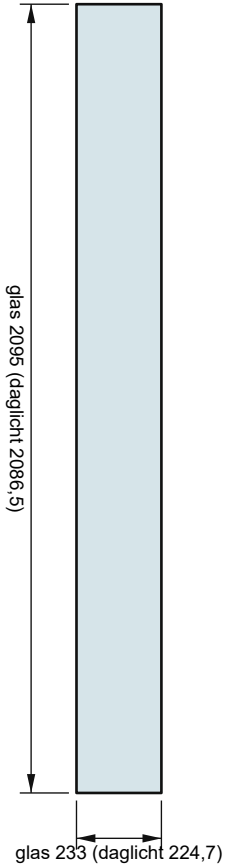

Waar het stuk zit

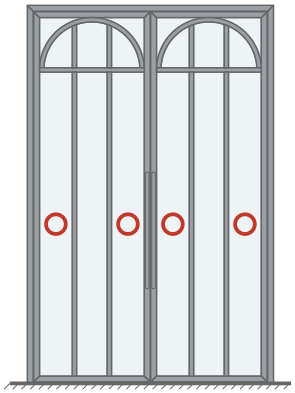

Opbouw (2:1)



gelaagd 44.2 helder

altijd veiligheidsglas (EN 12543 / EN 12150)

Bewerking en verbindingen


Bewerking: veiligheidsglas; glasmaat = daglicht + 4 rondom

Titel: **Pos 23: Ruit**			
Deur: Dubbele kathedraal · opening 1700 x 2600		Tekeningnummer: **TD-89-23**	
Maten en toleranties: mm · ISO 2768-m · eerste hoek	Opgesteld: Ian · laswerken	Uitgifte: 2026-11-10	Blad: 23 / 26


24 2 x Ruit

gelaagd 44.2 helder · 218 x 2095 · 9,48 kg/st

Aanzicht (1:20): daglicht, de ruit is 4 mm groter rondom

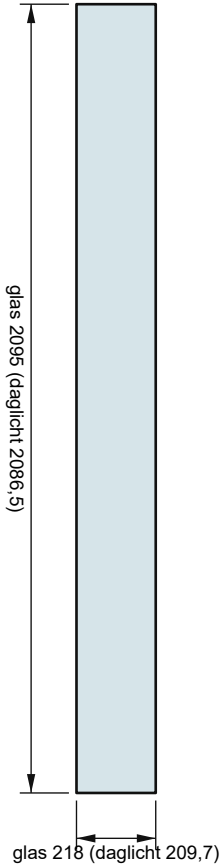

Waar het stuk zit

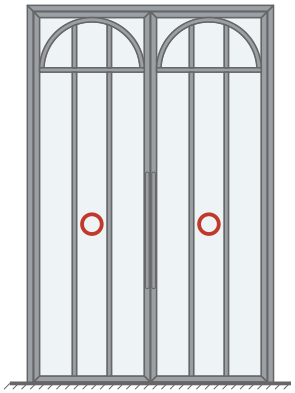

Opbouw (2:1)



gelaagd 44.2 helder

altijd veiligheidsglas (EN 12543 / EN 12150)

Bewerking en verbindingen


Bewerking: veiligheidsglas; glasmaat = daglicht + 4 rondom

Titel: **Pos 24: Ruit**			
Deur: Dubbele kathedraal · opening 1700 x 2600		Tekeningnummer: **TD-89-24**	
Maten en toleranties: mm · ISO 2768-m · eerste hoek	Opgesteld: Ian · laswerken	Uitgifte: 2026-11-10	Blad: 24 / 26


25 4 x Ruit met vorm (DXF)

gelaagd 44.2 helder · 202 x 294 · 0,9 kg/st

Aanzicht (1:5): daglicht, de ruit is 4 mm groter rondom

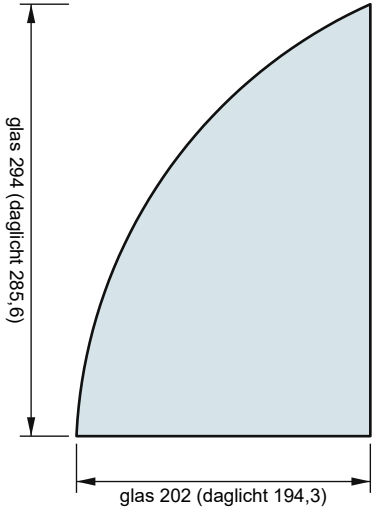

Waar het stuk zit

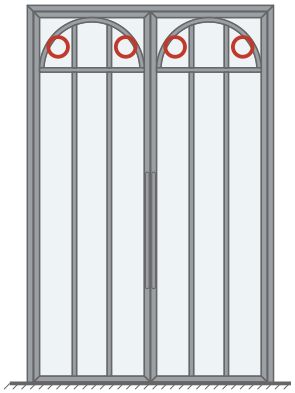

Opbouw (2:1)



gelaagd 44.2 helder

altijd veiligheidsglas (EN 12543 / EN 12150)

Bewerking en verbindingen


Bewerking: veiligheidsglas; snijden op de DXF (daglicht + 4 rondom)

Titel			
Pos 25: Ruit met vorm (DXF)			
Deur		Tekeningnummer	
Dubbele kathedraal · opening 1700 x 2600		**TD-89-25**	
Maten en toleranties	Opgesteld	Uitgifte	Blad
mm · ISO 2768-m · eerste hoek	Ian · laswerken	2026-11-10	25 / 26


26 2 x Ruit met vorm (DXF)

gelaagd 44.2 helder · 218 x 323 · 1,43 kg/st

Aanzicht (1:5): daglicht, de ruit is 4 mm groter rondom

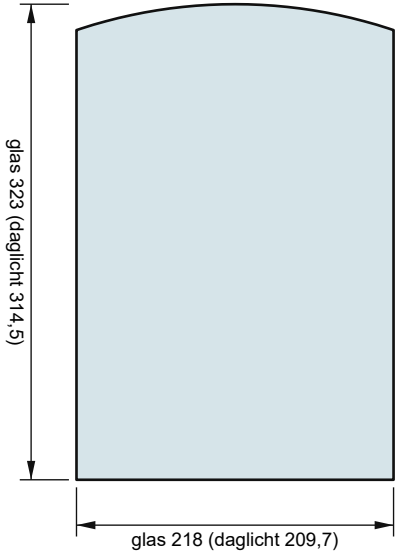

Waar het stuk zit

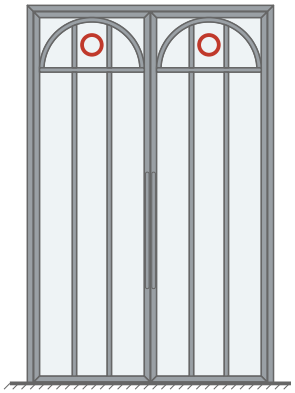

Opbouw (2:1)



gelaagd 44.2 helder

altijd veiligheidsglas (EN 12543 / EN 12150)

Bewerking en verbindingen

Bewerking: veiligheidsglas; snijden op de DXF (daglicht + 4 rondom)

Titel			
Pos 26: Ruit met vorm (DXF)			
Deur		Tekeningnummer	
Dubbele kathedraal · opening 1700 x 2600		**TD-89-26**	
Maten en toleranties	Opgesteld	Uitgifte	Blad
mm · ISO 2768-m · eerste hoek	Ian · laswerken	2026-11-10	26 / 26